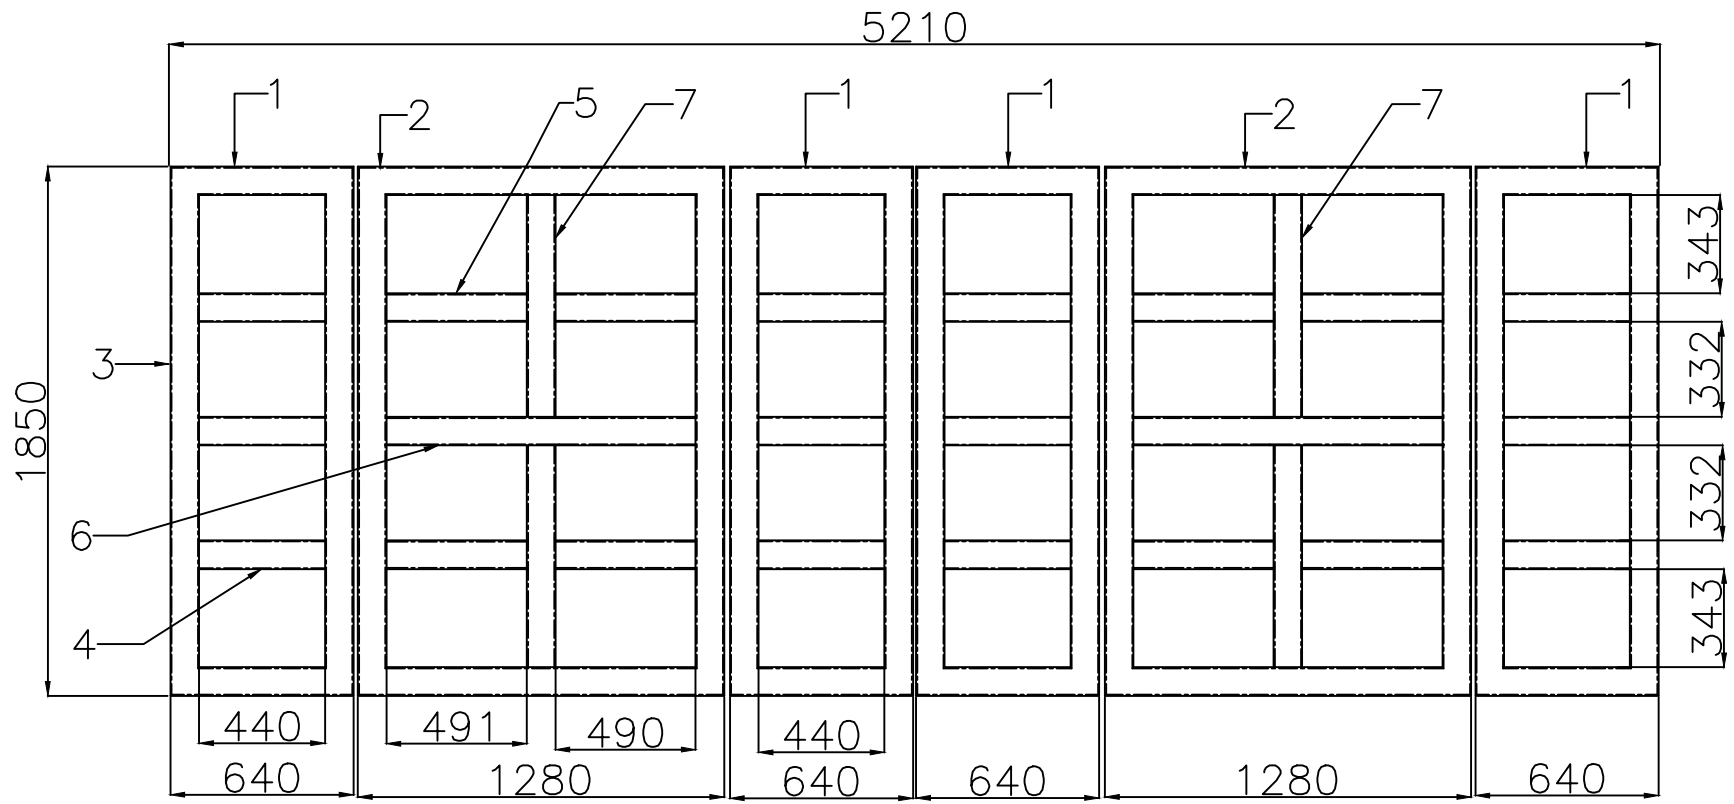

SR. NO.	DESCRIPTION	SPECIFICATION	QTY
1	RECT. TUBE	150 X 100 X 4, 645 LENGTH	8 NOS
2	RECT. TUBE	150 X 100 X 4, 1290 LENGTH	4 NOS
3	RECT. TUBE	150 X 100 X 4, 1850 LENGTH	12 NOS
4	SQ. TUBE	100 X 100 X 3, 445 LENGTH	12 NOS
5	SQ. TUBE	100 X 100 X 3, 496 LENGTH	8 NOS
6	SQ. TUBE	100 X 100 X 3, 1090 LENGTH	2 NOS
7	SQ. TUBE	100 X 100 X 3, 775 LENGTH	4 NOS

This drawing & design is the property of NIHVA TECHNOLOGIES. Not to be sold or copied to any other concern.

TITLE
SLIDING AND FOLDING GATE LEAF STRUCTURE

	NAME	SIGN	DATE
DRAWN	G.P.		30.08.21
CHECK	A.K.		30.08.21
APPRD.	V.T.		30.08.21

If any queries contact : design@nihva.com

ALL DIMENSION ARE IN mm

NIHVA
NIHVA TECHNOLOGIES PVT. LTD.

NIHVA TECHNOLOGIES PVT. LTD. PUNE
Tel : 020 66304033
Email:- info@nihva.com
Website:- www.nihva.com

CLIENT - HAIMAVATHY PROPERTIES PVT. LTD.
LOCATION - MUMBAI
PRODUCT - SLIDING & FOLDING GATE 5500 X 2000
NIHVA\21-22\VDR\0137 REV- 00
SCALE: NTS SHEET: 01 OF 01