


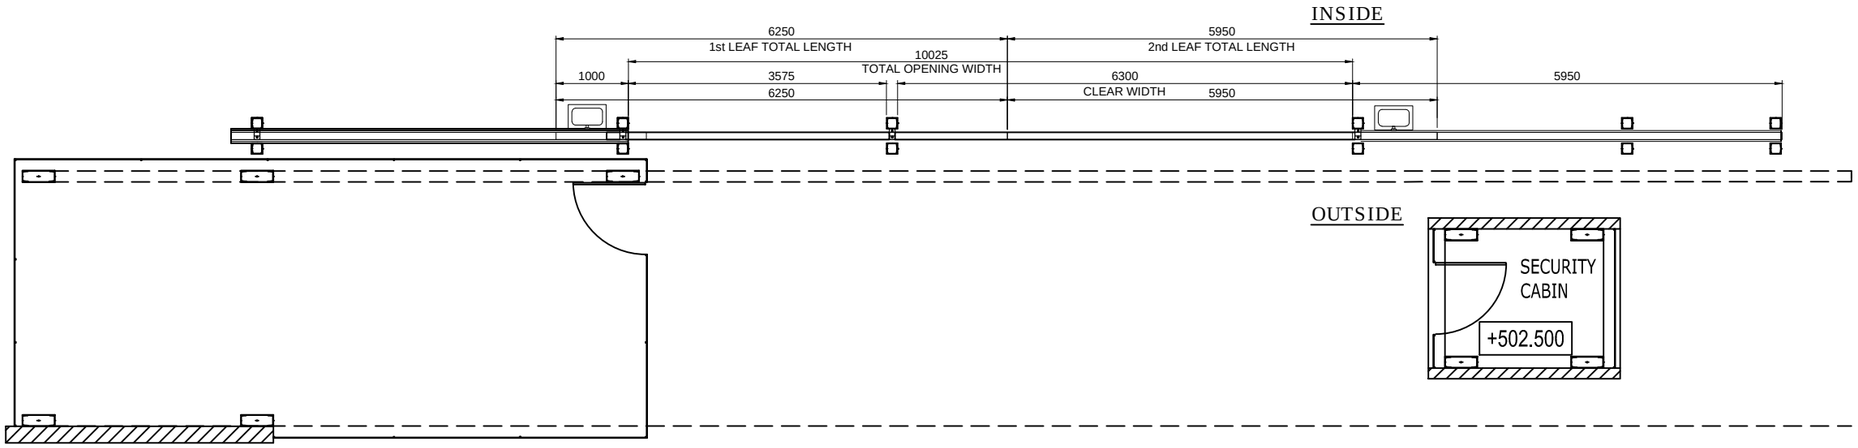


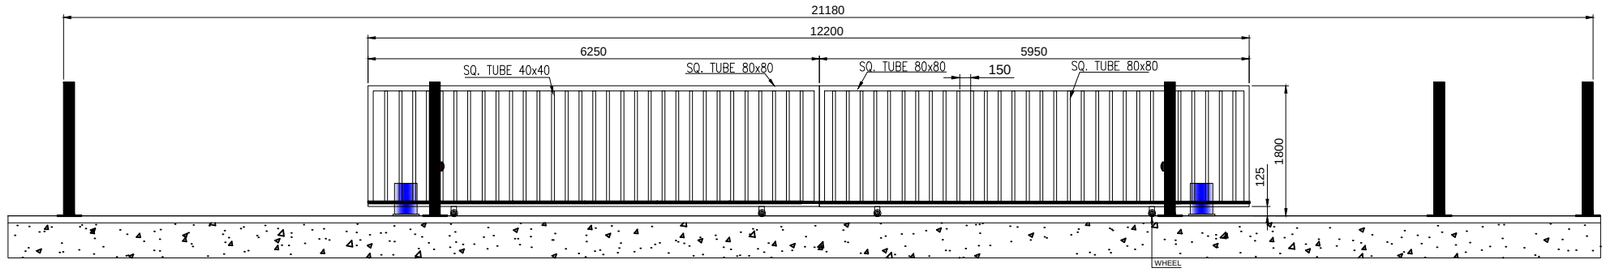

VIEW FROM OUTSIDE

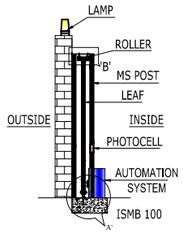

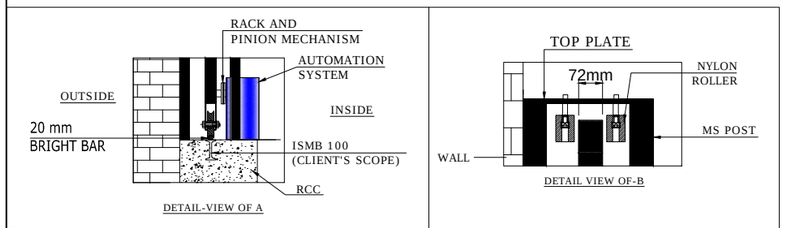

DETAIL-VIEW OF A

DETAIL VIEW OF-B

SR NO	TUBE SPECIFICATION	
1	72X72 mm MS TUBE	OUTER FRAME
2	40X40 mm MS TUBE	INNER PATTERN
3	GAP BETWEEN TUBES	150mm
4	MS SHEET	MS SHEET
5	72X72 mm MS TUBE	FOR POST

TOLERANCE:- ± 10mm

CLEAR WIDTH (CW)	CLEAR HEIGHT (CH)	QUANTITY
10025mm	1800mm	1 NOS

DIMENSION :

CLEAR WIDTH	CLEAR HEIGHT	QUANTITY
10025mm	1800mm	1 NOS

MATERIAL: MS

THICKNESS :

NOTE-
1. ALL REQUIRED CIVIL WORK WILL BE IN CLIENTS SCOPE.

NIHVA
NIHVA TECHNOLOGIES PVT. LTD.
Website:- www.nihva.com
NIHVA TECHNOLOGIES PVT. LTD. PUNE
Email:- info@nihva.com
TEL :020 66304033

TITLE:

AUTOMATIC BI-PARTING SLIDING GATE

CLIENT'S APPROVAL :

CLIENT - SANDVIK

PROJECT -

SITE LOCATION :- DAPODI, PUNE

DWG. NO. : NIHVA/18-19/0231

SCALE: NTS		WT:	SHEET: 1 OF 1
	NAME	SIGN	DATE
DRAWN	A.K.		10.01.19
CHECK	P.A.		10.01.19
APPROVED	R.D		10.01.19

IF ANY QUERIES CONTACT:- design@nihva.com

NOTE: ALL DIMENSIONS ARE IN mm

THIS DRAWING & DESIGN IS THE PROPERTY OF NIHVA TECHNOLOGIES. NOT TO BE SOLD OR COPIED TO ANY OTHER CONCERN.