

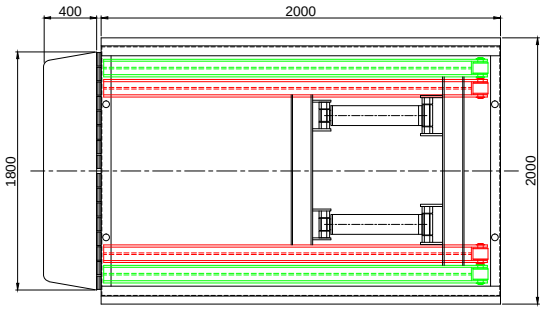



PLAN VIEW

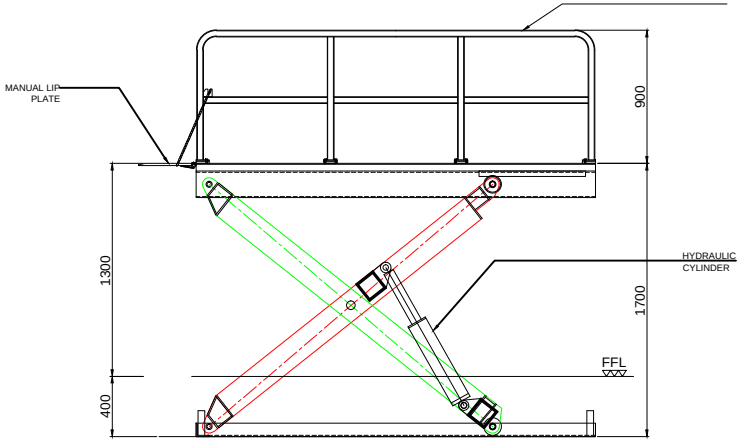


FRONT VIEW - OPEN POSITION

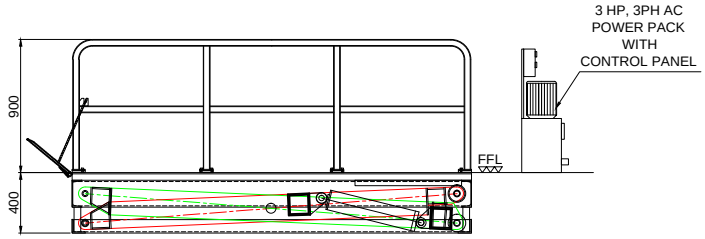

FRONT VIEW - SHUT POSITION

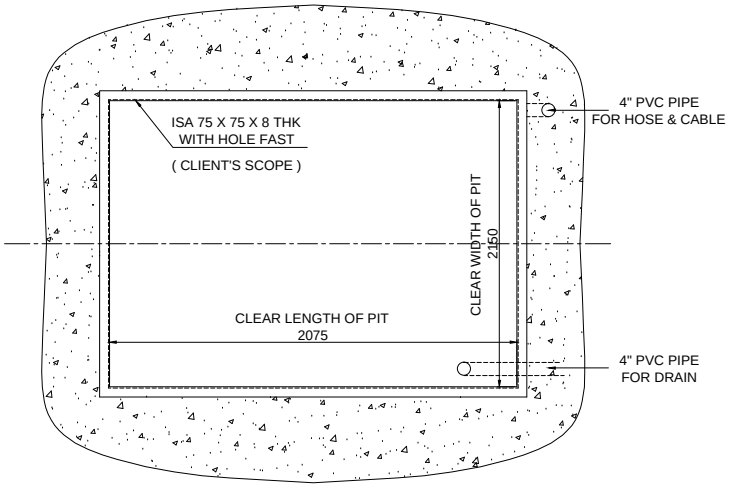

TOP VIEW OF PIT

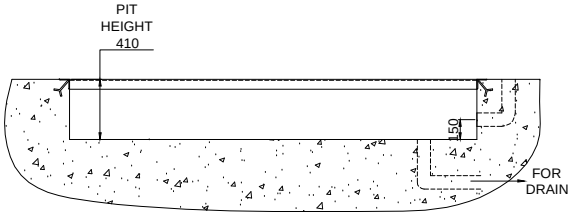

FRONT VIEW OF PIT

TOLERANCE - ±10mm

CAPACITY	2 TON
PLATFORM SIZE	2000 (L) X 2000(W)
POWER PACK	3 HP, 3 PH
SHUT HEIGHT	400 MM
LIFT HEIGHT	1300 MM
OPEN HEIGHT	1700 MM

This drawing & designing is the property of NIHVA TECHNOLOGIES. Not be sold or copy to any other concern.

TITLE: ELECTRO-HYDRAULIC SCISSOR LIFT

NIHVA TECHNOLOGIES PVT. LTD.
NIHVA TECHNOLOGY PVT. LTD. PUNE
Tel : 020 66304033
Email:- info@nihva.com
Website:- www.nihva.com

	SIGN	DATE
DRAWN	SIDDHESHWAR	25.1.2021
CHECK	SIDDHESHWAR	25.1.2021
REV.		
APPROVAL		

CLIENT - TOPBAND INDIA PVT LTD
PROJECT -
SITE -
DWG. NO. : NIHVA/20-21/0142
If any queries contact : nihvacare@nihva.com
SCALE: NTS | WT: | SHEET: 01 OF 01
ALL DIMENSION ARE IN mm