

A1 DO NOT SCALE DRAWING. CHECK ALL DIMENSIONS ON SITE.
ALL RIGHTS RESERVED.
INTEGRATED DESIGN ASSOCIATES INDIA PVT. LTD.

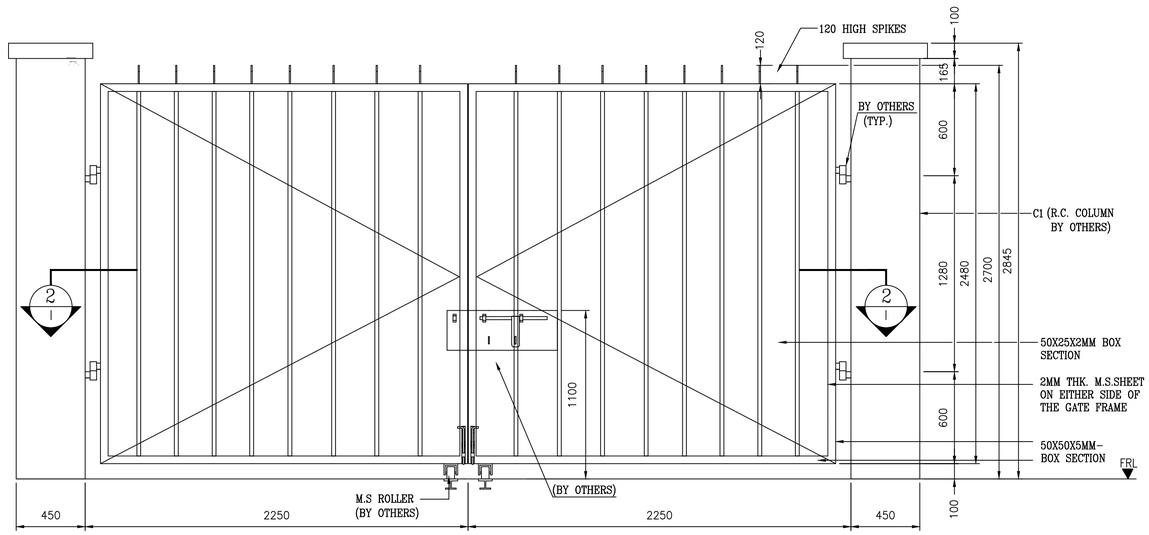

ELEVATION - A

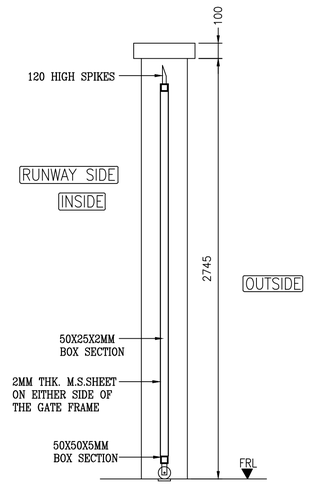


SECTION 1-1


IMPORTANT NOTES

STEEL NOTES:

1. ALL DIMENSIONS ARE IN MILLIMETERS AND ALL ELEVATIONS ARE IN METERS UNLESS NOTED OTHERWISE.
2. DO NOT SCALE OFF FROM THE DRAWINGS.
3. ALL WELD SHALL BE 4 MM FILLET WELDS UNLESS NOTED OTHERWISE.
4. ALL CONNECTIONS ARE FILED WELD.

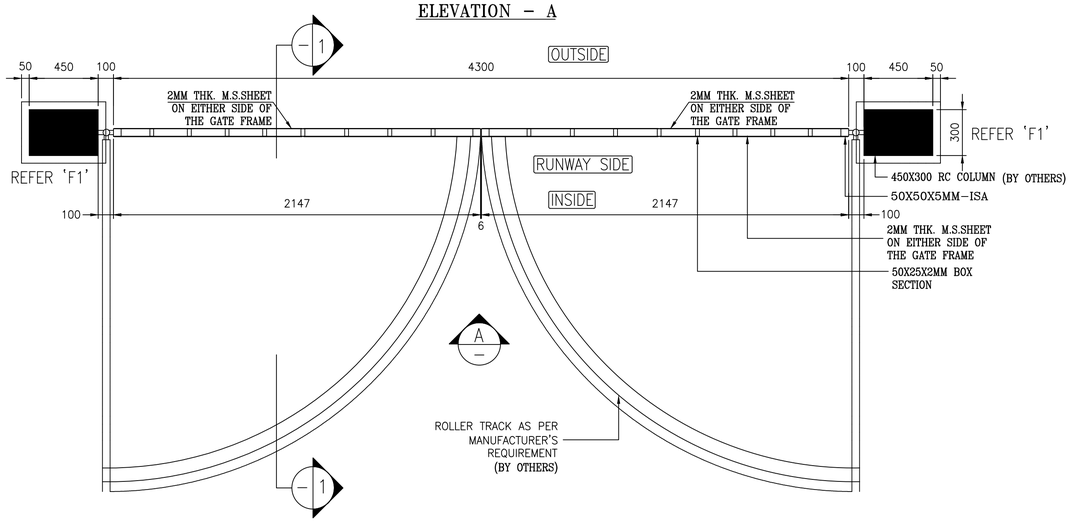


PLAN

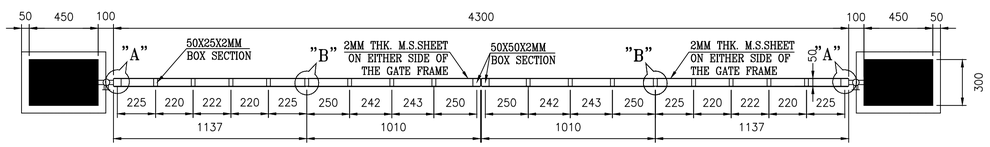

SECTION 2-2

1. CUSTOMER TO CHECK & CONFIRM ALL DIMENSIONS.
2. CUSTOMER PLEASE CHECK & UPDATE CLOUDED AREA.

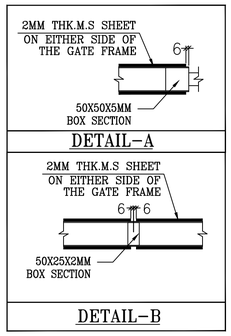

NORTH


GENERAL NOTES:

- Architectural Drawing shows equipment space holders only, for equipment layout please refer to individual service drawing.
- Refer Structural Drawings for Plinth Setting out
- For Boom Barrier, Mechanical Bollards and Security gates, kindly refer to seperate drawings (By Others)
- For door/window/louver details and schedules, refer to detail drawing.

REV	DATE	DESCRIPTION

		NAME	SIGN	DATE
DSGN				
DRWN				
CHKD				
APPD				

KEY PLAN:
SCALE 1:75000
NORTH

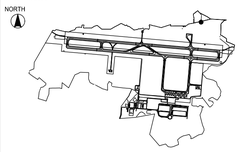

PROJECT:
GREENFIELD INTERNATIONAL AIRPORT AT MOPA, GOA

CLIENT:
GMR GOA INTERNATIONAL AIRPORT LIMITED

EPC CONTRACTOR:
MEGAWIDE CONSTRUCTION DMCC

ARCHITECTURAL CONSULTANT:
INTEGRATED DESIGN ASSOCIATES INDIA PVT. LTD.
c/o Ast.Mehta & Associates,
5th Floor, Midas Chambers, Off New Link Road
Andheri West, Mumbai - 400053
Maharashtra, India

STRUCTURAL CONSULTANT:
SY^2 + ASSOCIATES, Inc.
9801 Kamagong Street
Makati Philippines.

MEP CONSULTANT:
ESKAYEM
CONSULTANTS PVT. LTD.
301, 3RD FLOOR, SWASTIK CHAMBERS,
C.S.T. ROAD, CHEMBUR, MUMBAI-400071
TEL 022-25262645/46/47

PACKAGE:
SECURITY GATE HOUSE

TITLE:
GATE HOUSE TYPICAL SWING GATE DETAILS

DRAWING NO.:
GGIAL-MW-GH1-AR-10-SK-345

FILE REF.: | DATE : 03.06.2022

RELEASED FOR:	SCALE:	SIZE:	REV:
GFC	1 : 50	A1	R0

0 0.5 1.0 1.5 2.0 2.5
SCALE - 1 : 50

USER: INTEGRATED DESIGN ASSOCIATES LTD.