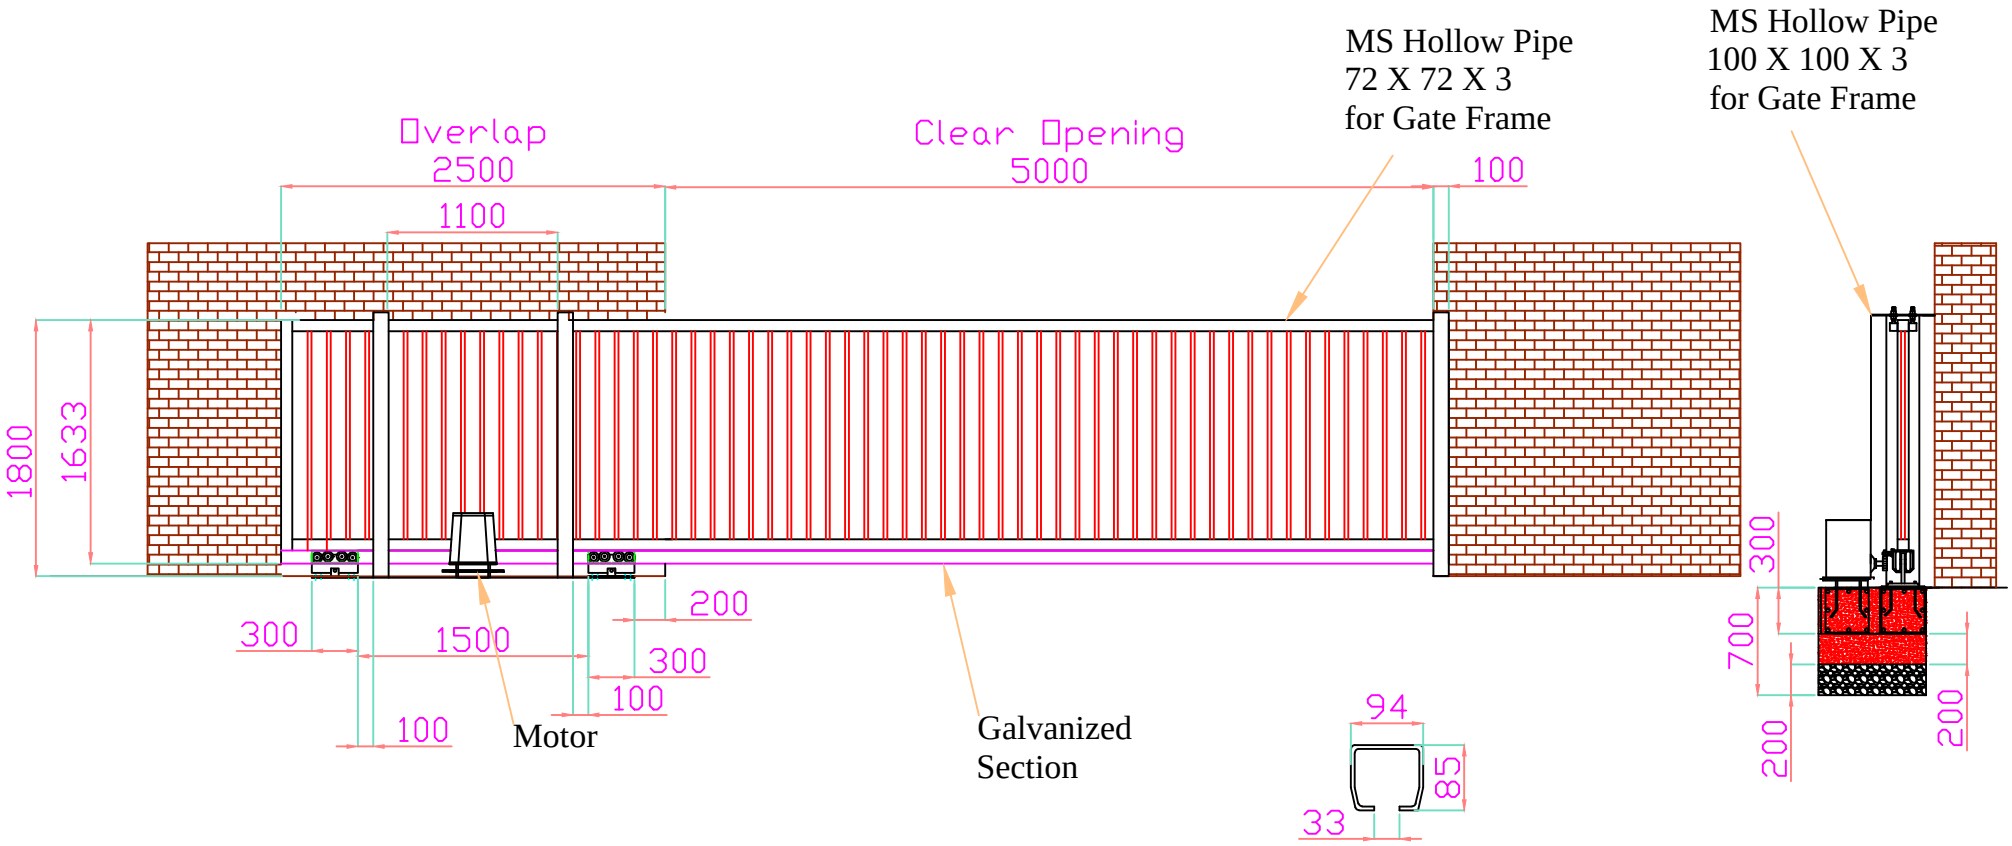


This drawing & designing is the property of NIHVA TECHNOLOGIES. Not be sold or copy to any other concern.

TITLE: CANTILEVER GATE FOUNDATION DETAILS		
	SIGN	DATE
DRAWN	ABHIJIT	08/11/14
CHECK	ANIL	08/11/14
REV.	01	
CLIENT APPROVAL		
ALL DIMENSION ARE IN mm		

NIHVA
NIHVA TECHNOLOGIES PVT. LTD.
NIHVA TECHNOLOGY PVT. LTD. PUNE
Tel : 020 66304033
Email:- info@nihva.com
Website:- www.nihva.com

CLIENT - SHAPOORJI PALANJI
PROJECT - MARS CHOCOLATE
SITE - KHED
DWG. NO. - NVA/SH.PA./01
SCALE:01 | Ref. No. | SHEET:01
If any queries contact : projects@nihva.com