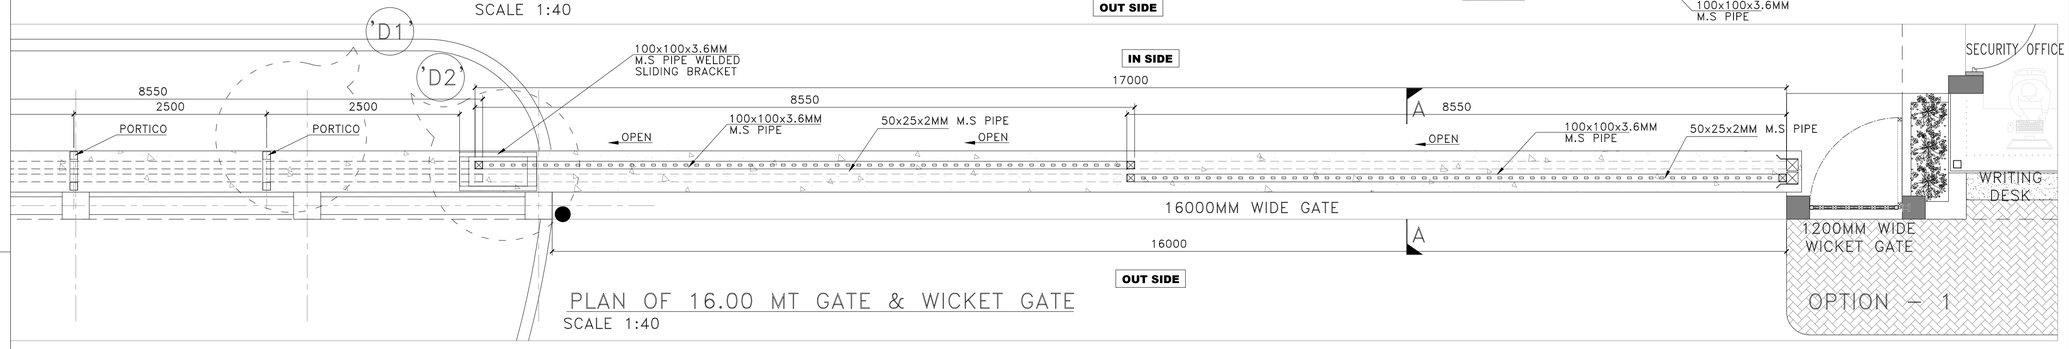
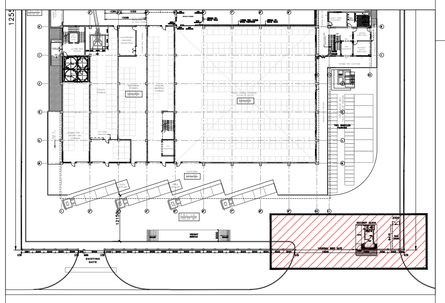



ELEVATION FOR ENTRANCE GATE
SCALE 1:40




PLAN OF 16.00 MT GATE & WICKET GATE
SCALE 1:40

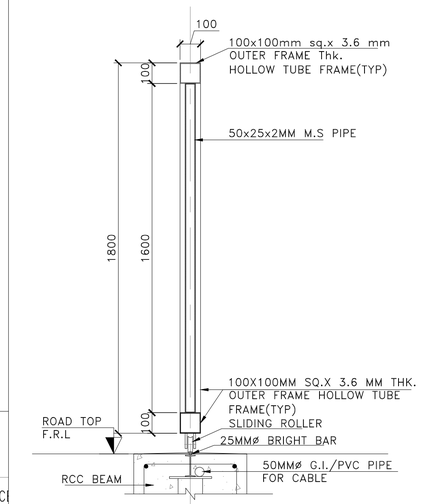


NOTES :-


1. DO NOT SCALE THE DRAWING. REFER TO WRITTEN DIMENSIONS ONLY.
2. ALL MEASUREMENTS MUST BE CHECKED AND VERIFIED AT SITE. ANY DISCREPANCY FOUND,TO BE NOTIFIED TO THE CONSULTING ENGINEER, BEFORE EXECUTION.
3. ALL DIMENSIONS ARE IN MM.& ALL LEVELS ARE IN METERS UNLESS OTHERWISE SPECIFIED.
4. F.G.L & F.R.L AS PER SITE ROAD LAYOUT PLAN.

LEGEND :-


F.G.L. = FINISHED GROUND LEVEL
F.R.L. = FINISHED ROAD LEVEL
F.F.L. = FINISHED FLOOR LEVEL





SECTION A–A GATE SECTION
SCALE 1:15

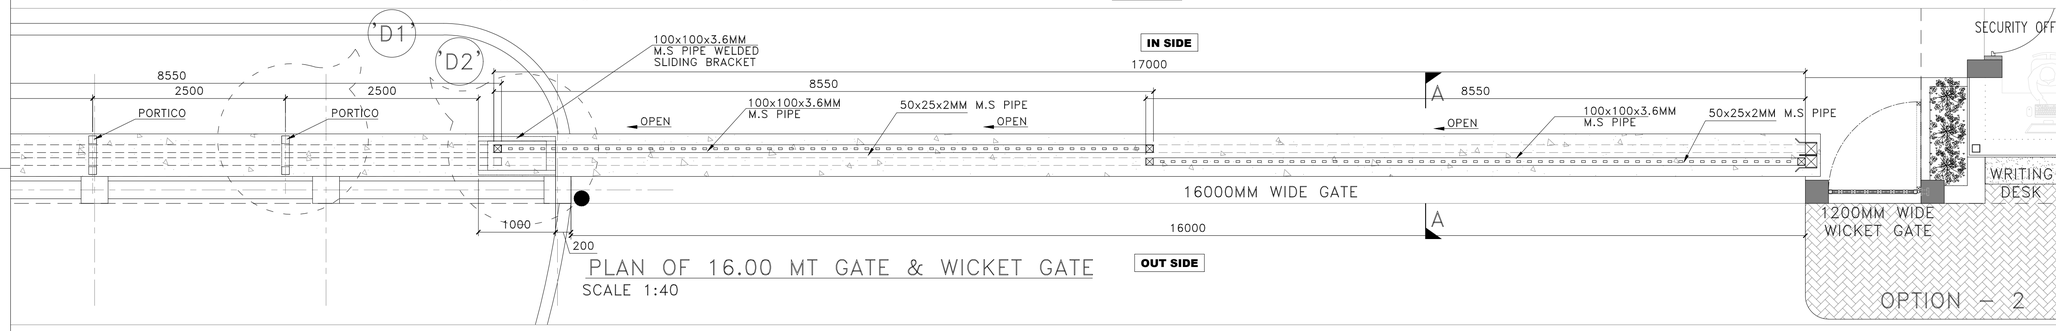

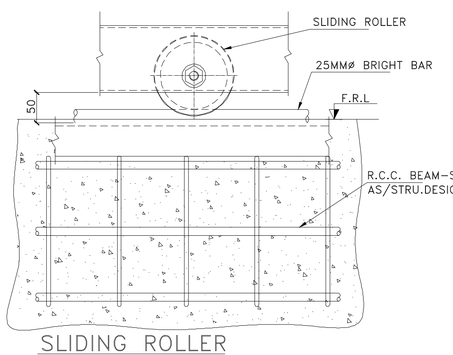

PLAN OF 16.00 MT GATE & WICKET GATE
SCALE 1:40





SLIDING ROLLER
SCALE 1:25

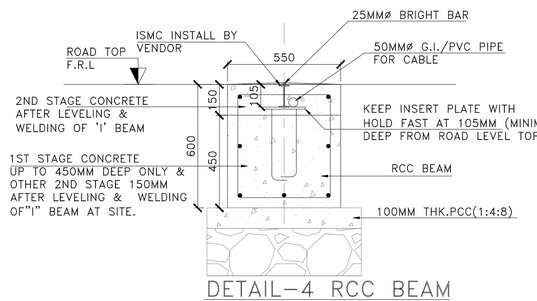



DETAIL–4 RCC BEAM
SCALE 1:15

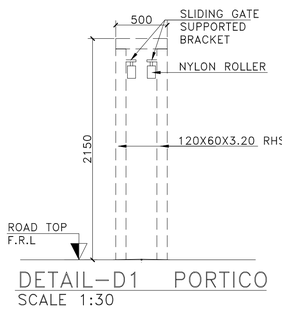


DETAIL–D1 PORTICO
SCALE 1:30

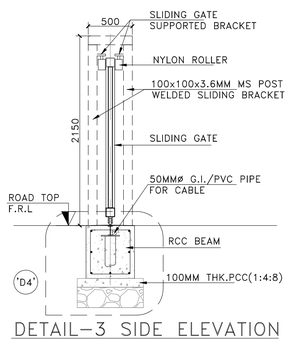


DETAIL–3 SIDE ELEVATION
SCALE 1:30

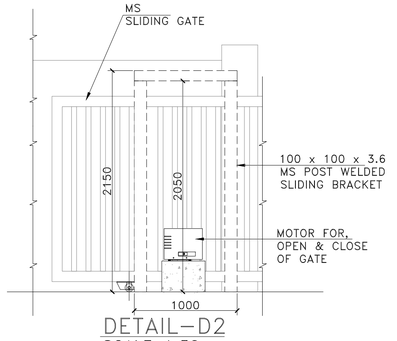


DETAIL–D2
SCALE 1:30
SLIDING BRACKET

| R0 | 18-06-24 | ISSUED FOR APPROVAL | DEVANG | AMITA | VNV | EMAIL |
|---|---|---|---|---|---|---|
| REV. | DATE | DESCRIPTION | DRN. | CHK. | APP. | PRN. |

ISSUED FOR

☐ INFORMATION ☑ APPROVAL ☐ CONSTRUCTION
☐ ENQUIRY ☐ ORDER ☐ REVIEW

CLIENT : LAXMI SNACKS PVT.LTD.
PLOT NO / SHED NO.-123, NARODA G.I.D.C.

PROJECT : PROPOSED FACTORY

CONSULTANT :

SHAH & TALATI Design & Engineering
9th FLOOR, KIRTI TOWER, TILAK ROAD, VADODARA-390001, GUJARAT, INDIA.
PHONE : +91-265-2440701 / 2440726
E-MAIL : design@shahntalati.com
WEBSITE : www.shahntalati.com

PROJECT NO. :- 2219

TITLE :- **16.00MT GATE&WICKET GATE PLAN & ELEVATION**

| DRAWN BY | DEVANG | |
|---|---|---|
| CHECKED BY | AMITA | |
| APPROVED BY | VNV | |
| DRAWING NO. | 2219-GATE-A01-SH1-A1-R0 | |
| SCALE : VARIES | | |

R0 18 06 24

SHEET 1 OF 2

THIS DOCUMENT OR DRAWING IS THE PROPERTY OF SHAH & TALATI CONSULTING ENGINEERS AND SHALL NOT, UNDER ANY CIRCUMSTANCES, BE TOTALLY OR PARTIALLY, DIRECTLY OR INDIRECTLY, TRANSFERRED, REPRODUCED, COPIED, DISCLOSED OR USED WITHOUT SHAH & TALATI'S PRIOR WRITTEN CONSENT.

A1