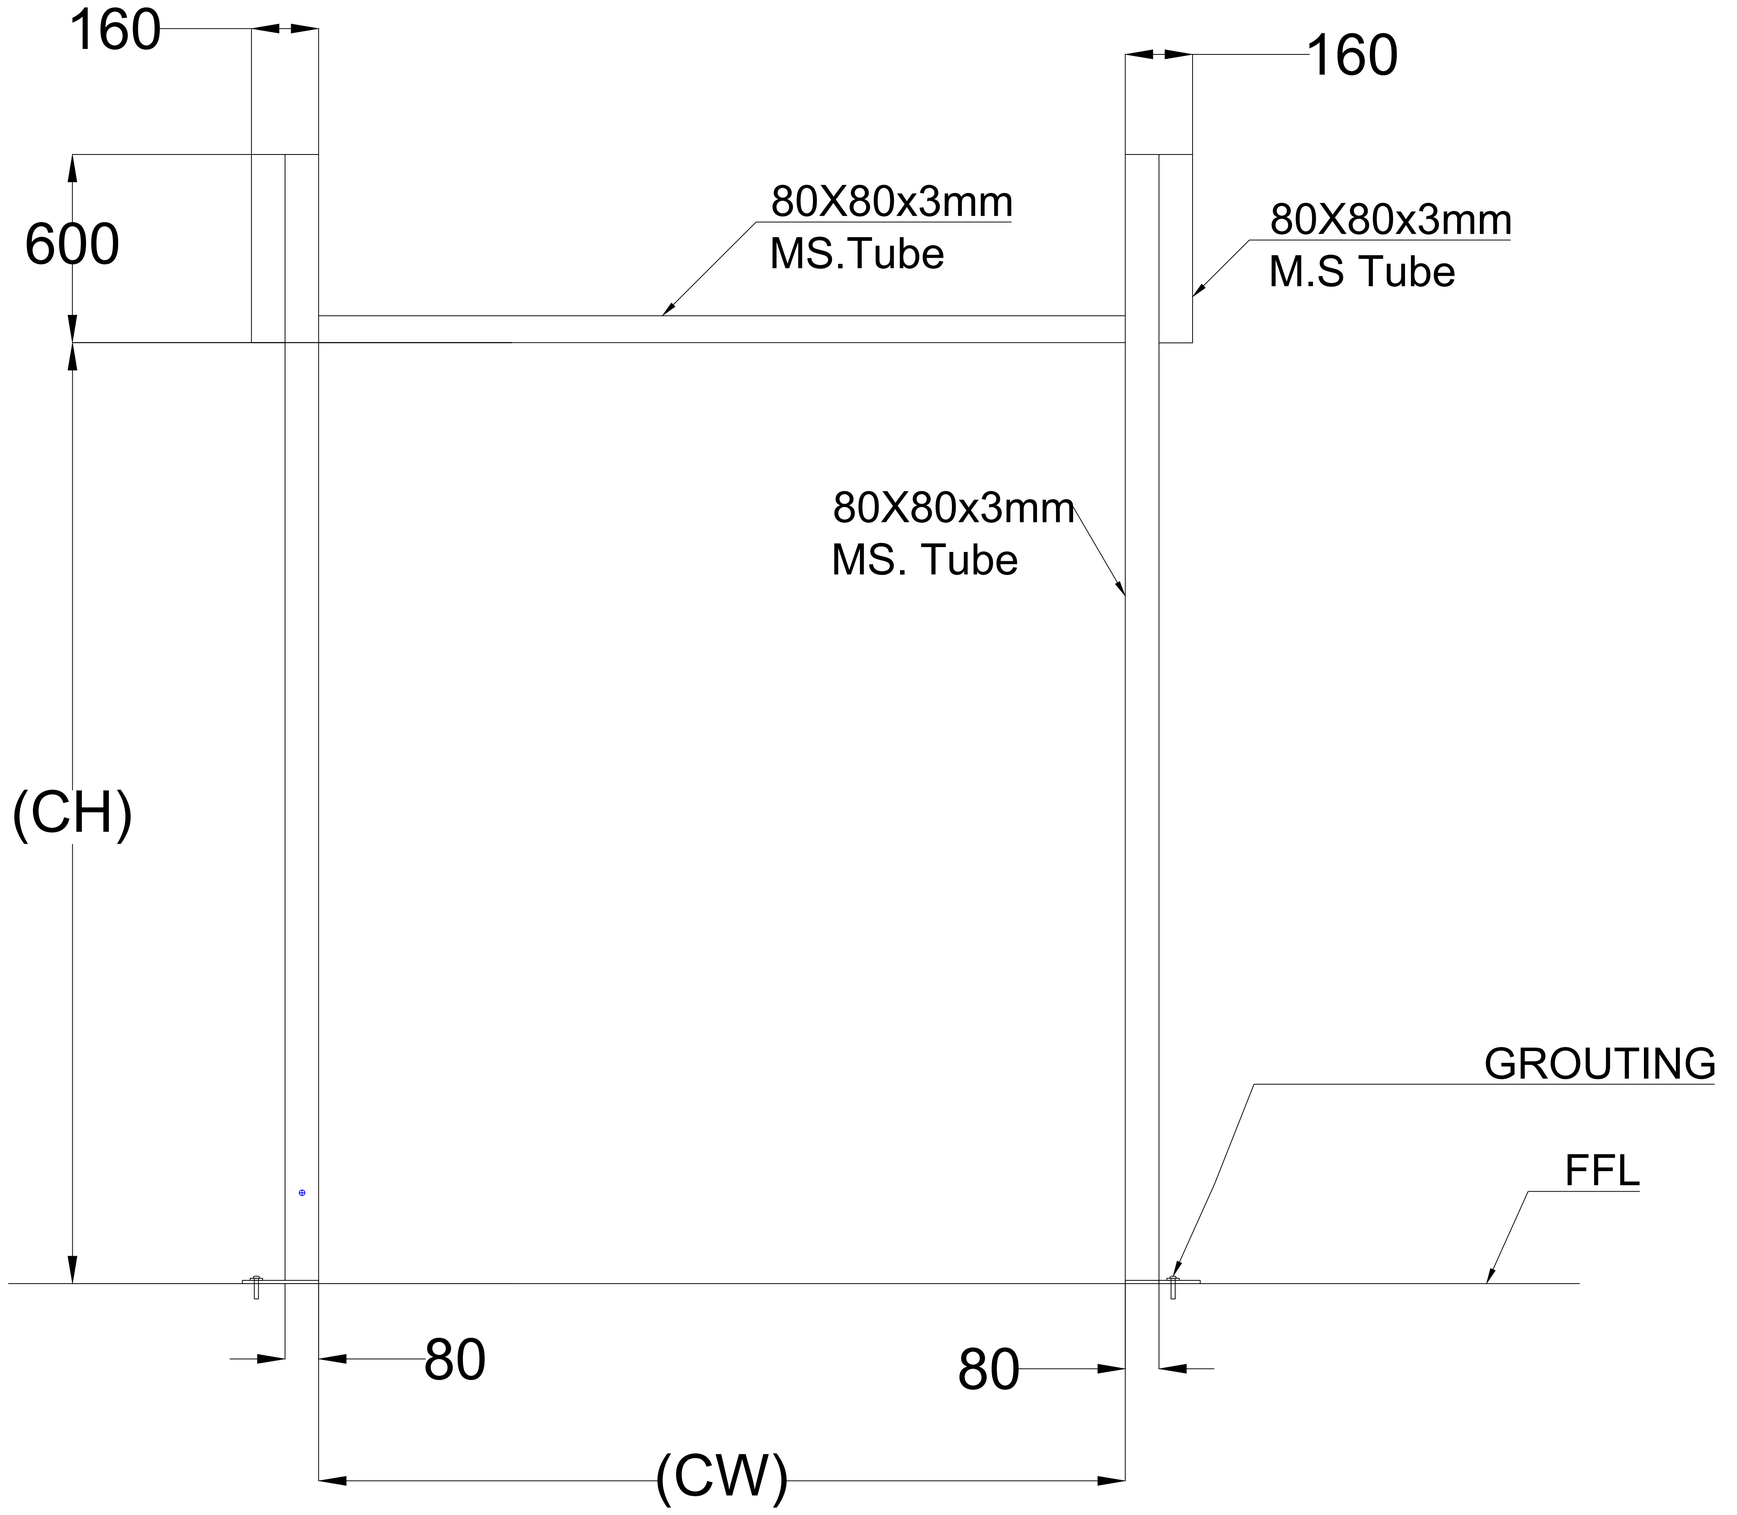


M.S. STRUCTURE DETAILS

SR.	CLEAR WIDTH (CW)	CLEAR HEIGHT (CH)	QTY.
01	4500	4075	01
02	2400	4075	05
02	2500	4500	01

This drawing & design is the property of NIHVA TECHNOLOGIES. Not to be sold or copied to any other concern.

TITLE: SHUTTER ST.

	NAME	SIGN	DATE
DRAWN	S.J		11.07.2024
CHECK	S.W.		11.07.2024
APPRD.	V.T		11.07.2024

If any queries contact : projectsupport@nihva.com

ALL DIMENSION ARE IN mm

NIHVA TECHNOLOGIES PVT. LTD.

NIHVA TECHNOLOGIES PVT. LTD. PUNE
Tel : 020 66304033
Email:- info@nihva.com
Website:- www.nihva.com

CLIENT - PANCHSHIL

PROJECT - ROLLING SHUTTER ST.

FORMAT NO -

DWG. NO. : NIHVA/24-25/00XX | REV- R00

SCALE: NTS | WT: | SHEET: