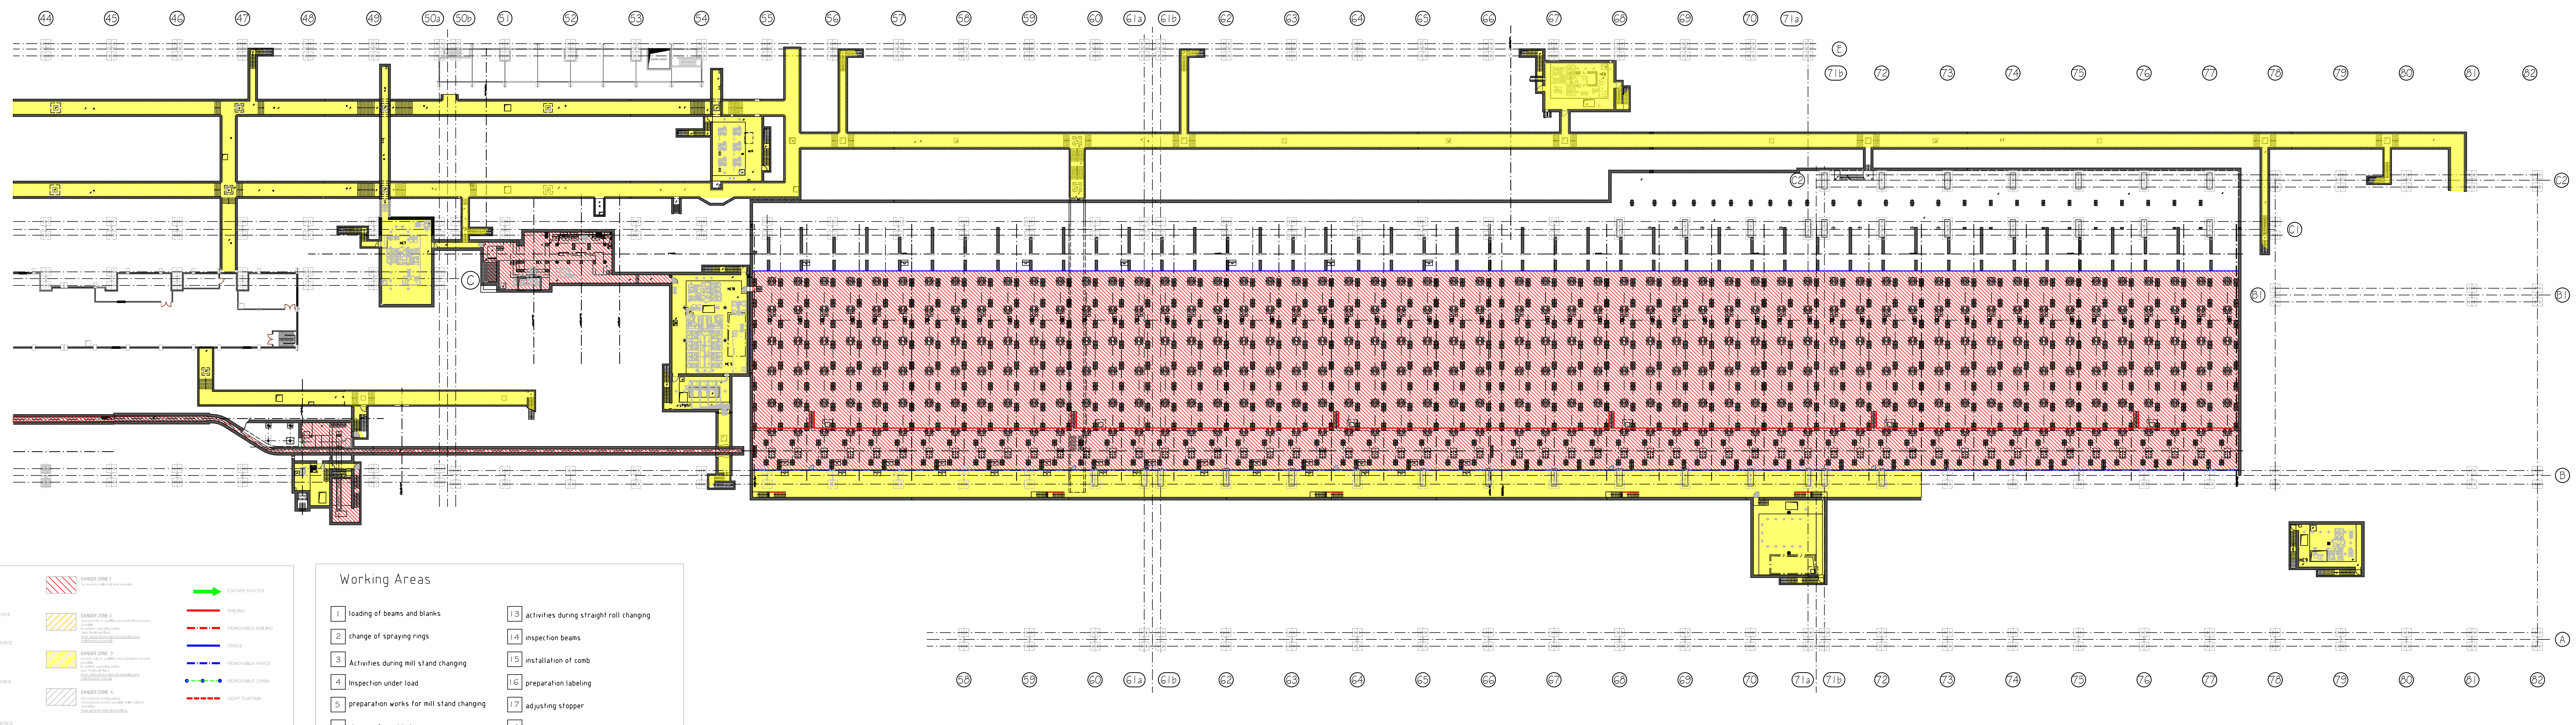

GATE	DANGER ZONE 1 No access while unit is in operation.	ESCAPE ROUTES
GATE WITH MECH. LOCKING DEVICE	DANGER ZONE 2 Access only to qualified and authorized persons possible in defined operating states. High Residual Risks Note safety instructions in operating and maintenance manual.	RAILING
GATE WITH ELECT. LOCKING DEVICE	DANGER ZONE 3 Access only to qualified and authorized persons possible in defined operating states. Low Residual Risks Note safety instructions in operating and maintenance manual.	REMOVABLE RAILING
DOOR WITH MECH. LOCKING DEVICE	DANGER ZONE 4 Permanente working place: Unrestricted access possible while unit is in operation. Note general safety instructions.	FENCE
DOOR WITH ELECT. LOCKING DEVICE	WORKING PLACE Part of no access zone, that can be entered by trained operators under particular conditions only Note safety instructions in operating and maintenance manual.	REMOVABLE FENCE
DOOR	REQUEST-/ ACKNOWLEDGEMENT BUTTON	REMOVABLE CHAIN
DOOR WITH MECH. LOCKING DEVICE	EMERGENCY STOP	LIGHT CURTAIN
DOOR WITH ELECT. LOCKING DEVICE	ACKNOWLEDGEMENT BUTTON	

Working Areas

1	loading of beams and blanks	13	activities during straight roll changing
2	change of spraying rings	14	inspection beams
3	Activities during mill stand changing	15	installation of comb
4	Inspection under load	16	preparation labeling
5	preparation works for mill stand changing	17	adjusting stopper
6	change of saw blade	18	change of coils (bundling area)
7	preparation saw blade	19	unloading of bundles
8	change of chip bucket	20	removal of short length
9	change of scrap bucket	21	repairing of beams
10	handling of sample	22	preparation of rolls, chocks and guides
11	testing of sample (laboratory)	23	operating and control
12	preparation straightening rolls		

Positions of crossovers must be in correspondence with the General Routing Plan (by Customer)

This safety layout must be considered in coherence with safety Instructions in Operation and Maintenance Manual. (Especially Chapter A2)

9463 0000 / RAILBHIL

CATEGORY OF DRWG.	APPROVAL	INFORMATION	REFERENCE	RECORD	CONSTRUCTION

BHILAI STEEL PLANT, BHILAI, CHATTISGARH
7.0 MTPA EXPANSION

मेकॉन लिमिटेड
MECON LIMITED

VENSDOR'S NAME: SMS Meer/SMS Meer India/ABB
PACKAGE DESCRIPTION: UNIVERSAL RAIL MILL (Pkg No-047)
TITLE OF DRAWING. SAFETY LAYOUT, -5000
SCALE-
VENDOR'S DRG NO.-
PROJECT DRG. NO. BSP-SMS Meer-08-047-21-120-50-BE-06603

Fertigungsvorschriften
Manufacturing instructions
SN 200

Ursprung / Origin
Fertiggewicht
Finished weight
kg
Werkstoff / Material
Modell-Nr.
Pattern-No.
Projektionsmethode 1
First angle projection method
ISO 128

	Datum Date	Name
Bearb. Drawn	30.03.12	Fryen
Geprüft Checked	30.03.12	Prätzel
Norm Stand		

Aus-gabe Issue	Änderung Revision	Datum Date	Name

Typ
Type
Safety Layout
Benennung
Sicherheitslayout -5000
Title
SAFETY LAYOUT -5000
Maßstab
Scale
1:200
Sach-Nr.
Drawing-No.
0100133-00.603
Blatt
Sheet
4
4
Blätter
Sheets
Ersatz für:/Supersedes:
Ersetzt durch:/Superseded by:

SMS MEER
SMS group

Diese Zeichnung und alle darauf enthaltenen Informationen sind vertraulich. This drawing and all information on it is confidential.

A0