

Abbreviation's:
WOW-Wall Opening Width
WOH-Wall Opening Height
UC-Under CutFFL-Finished Floor Level

ASSESORIES DETALES

(a) HINGES: SS Ball bearing butt hinges size 100x75x3mm

(b) LOCK : Mortise Dead lock,Cylinder(Both side key) with Escutcheon

(c) DOOR CLOSER

(d) HANDLE : 1) SS D Handle(254 mm) FROM OUTSIDE
2) SS PUSH PLATE FROM INSIDE.

(e) CONCEALED FLUSH BOLT-300mm


(f) VISION PANEL- FRAME LESS VISION PANEL OF DOUBLE GLASS(5mm THK.) OF SIZE 350X750mm.

(g) AUTOMATIC BOTTOM SEAL FOR DOOR.


(h) PULL & PUSH engraved plate for door.

Shutter thickness : 47 mm
Frame Sheet thick : 1.2mm
Shutter sheet thick :0.8mm
Fixing : On Soliid Brick plasterd wall with Anchors

NOTE:- *All Dimensions are in mm.
*Tolerance:-All Linear Dimensions ±3mm,Others ±0.5mm.
*The Drawing Is For Location of Hardware only. Drawing Does Not Represent The Hardware For More Clarity, Please Go Through Hardware Broucher.

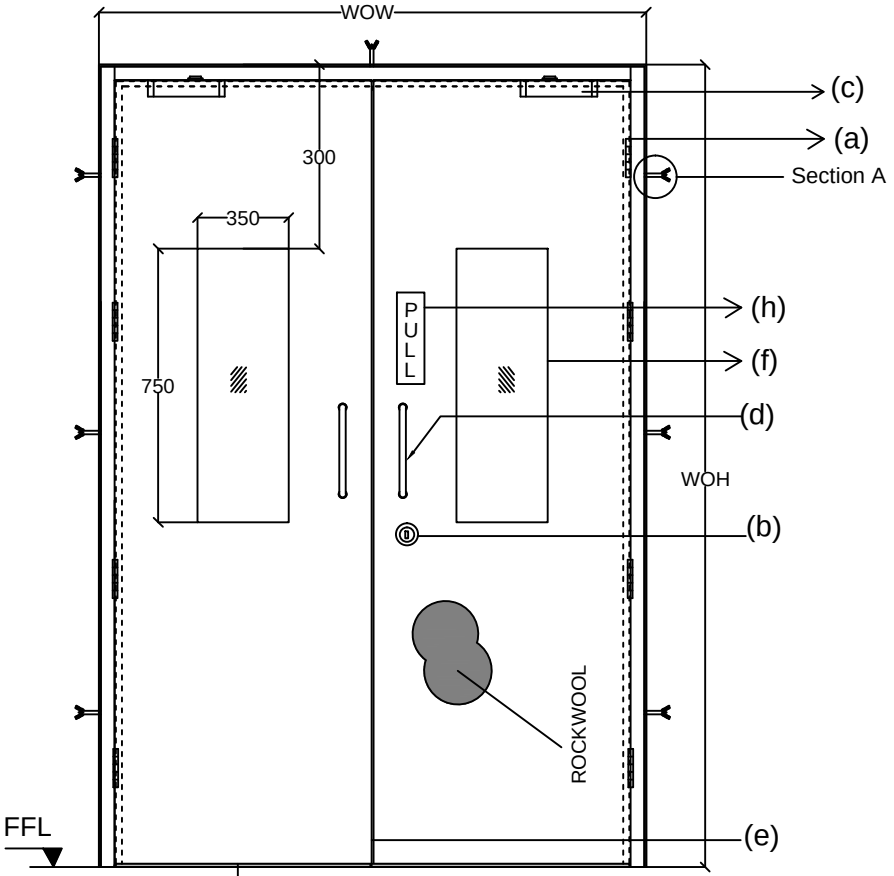


OUTSIDE ELEVATION

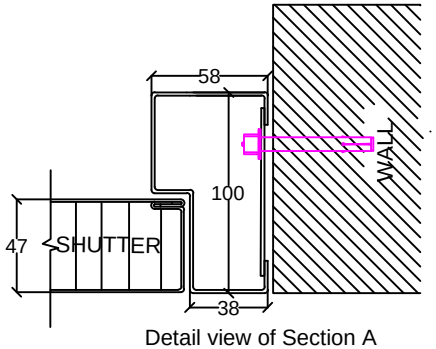

Detail view of Section A

Steel door size		
WOW	WOH	QUANTITY
1970	2200	1

ORIENTATION- TYPE 8 RIGHT HAND REVERSE ACTIVE

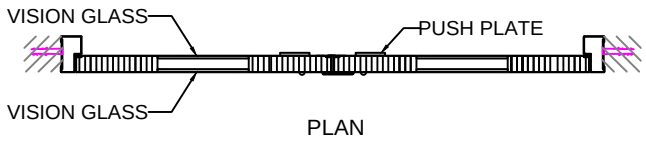

PLAN

COLOR:- Sapphire Blue(RAL 5003)

This drawing & designing is the property of NIHVA TECHNOLOGIES. Not be sold or copy to any other concern.

STEEL DOOR	ALL DIMENSION ARE IN mm				NIHVA TECHNOLOGY PVT. LTD. PUNE Tel : 020 66304033 Email:- info@nihva.com Website:-www.nihva.com
		NAME	DATE	SIGN.	
CLIENT APPROVAL	DRAWN	OMKAR	07/09/16		CLIENT -
	CHECK	ANIL	07/09/16		PROJECT -
	REV.	0			SITE -
	APPRD.				DWG. NO. - NIHVA/16-17/
	MFG				SCALE:NTS WT: SHEET: 01 OF 01
					If any queries contact : projects@nihva.com