

Abbrevation's:
WOW-Wall Opening Width
WOH-Wall Opening Height
UC-Under Cut
FFL-Finished Floor Level

ASSESORIES DETALES

(a) HINGES: SS Ball bearing butt hinges size 100x75x3mm

(b) LOCK : Mortise Dead lock,Cylinder(Both side key) with Escutcheon


(c) DOOR CLOSER :

(d) HANDLE : SS D HANDLE


(e) VISION PANEL : 5 mm THK. VISION GLASS 200(W) X 300(H)mm

Shutter thickness : 47 mm
Frame Sheet thick : 1.20mm
Shutter sheet thick : 0.80mm
Fixing : On Soliid Brick plasterd wall with Anchors

NOTE:- *All Dimensions are in mm.
*Tolerance:-All Linear Dimensions ±3mm,Others ±0.5mm.
*The Drawing Is For Location of Hardware only. Drawing Does Not Represent The Hardware For More Clarity, Please Go Through Hardware Broucher.

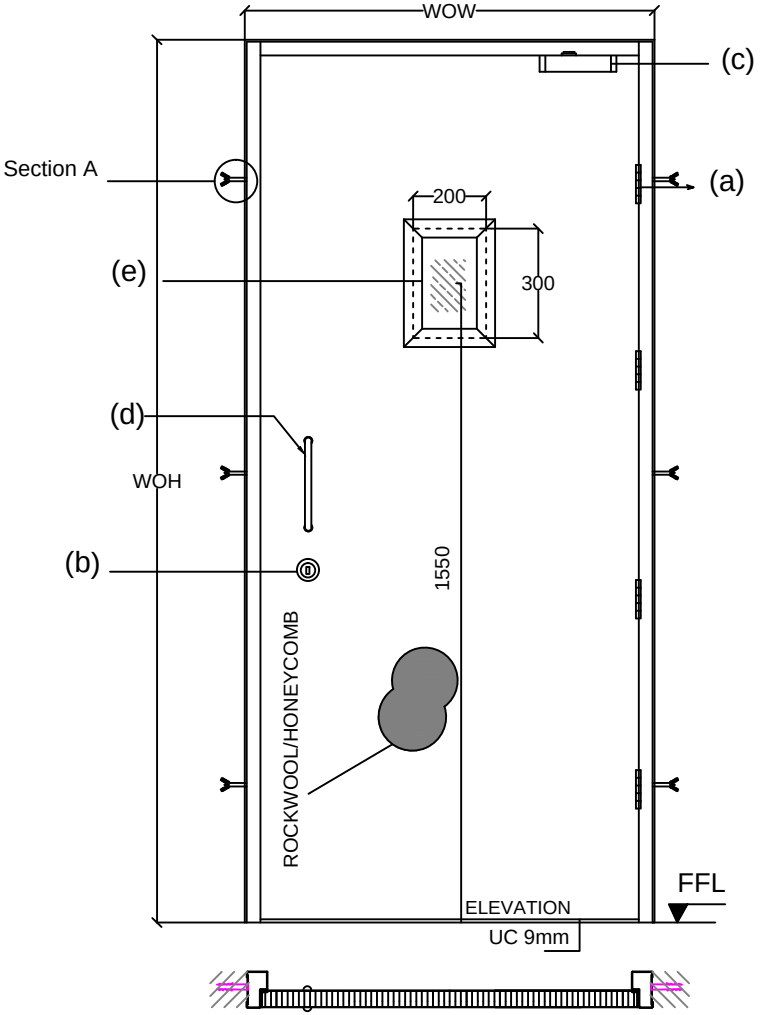

TOP VIEW

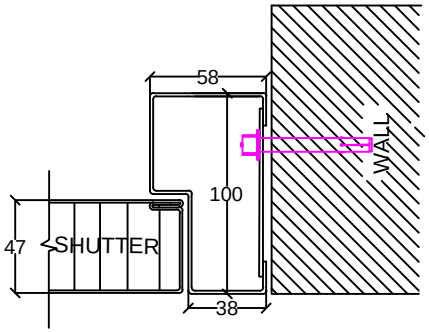

Section A

Steel door size

	WOW	WOH	TYPE 1	TYPE 2	TYPE 3	TYPE 4	QUANTITY
DOOR 4	1000	2165			1		1

This drawing & designing is the property of NIHVA TECHNOLOGIES. Not be sold or copy to any other concern.

FIRE RATED STEEL DOOR (SINGLE LEAF)

CLIENT APPROVAL

ALL DIMENSION ARE IN mm

	NAME	DATE	SIGN.
DRAWN BY	OMKAR	15/03/17	
CHECK BY	SAGAR P.	15/03/17	
REV.			
APPROVED BY	R.K.	15/03/17	
MFG			

NIHVA TECHNOLOGIES PVT. LTD.
NIHVA TECHNOLOGIES PVT. LTD. PUNE
Tel : 020 66304033
Email:- info@nihva.com
Website:-www.nihva.com

CLIENT -
PROJECT -
SITE -
DWG. NO. - NIHVA/16-17/VDR/069
SCALE: NTS | WT: | SHEET: 01 OF 01
If any queries contact : projects@nihva.com