

PRODUCED BY AN AUTODESK EDUCATIONAL PRODUCT

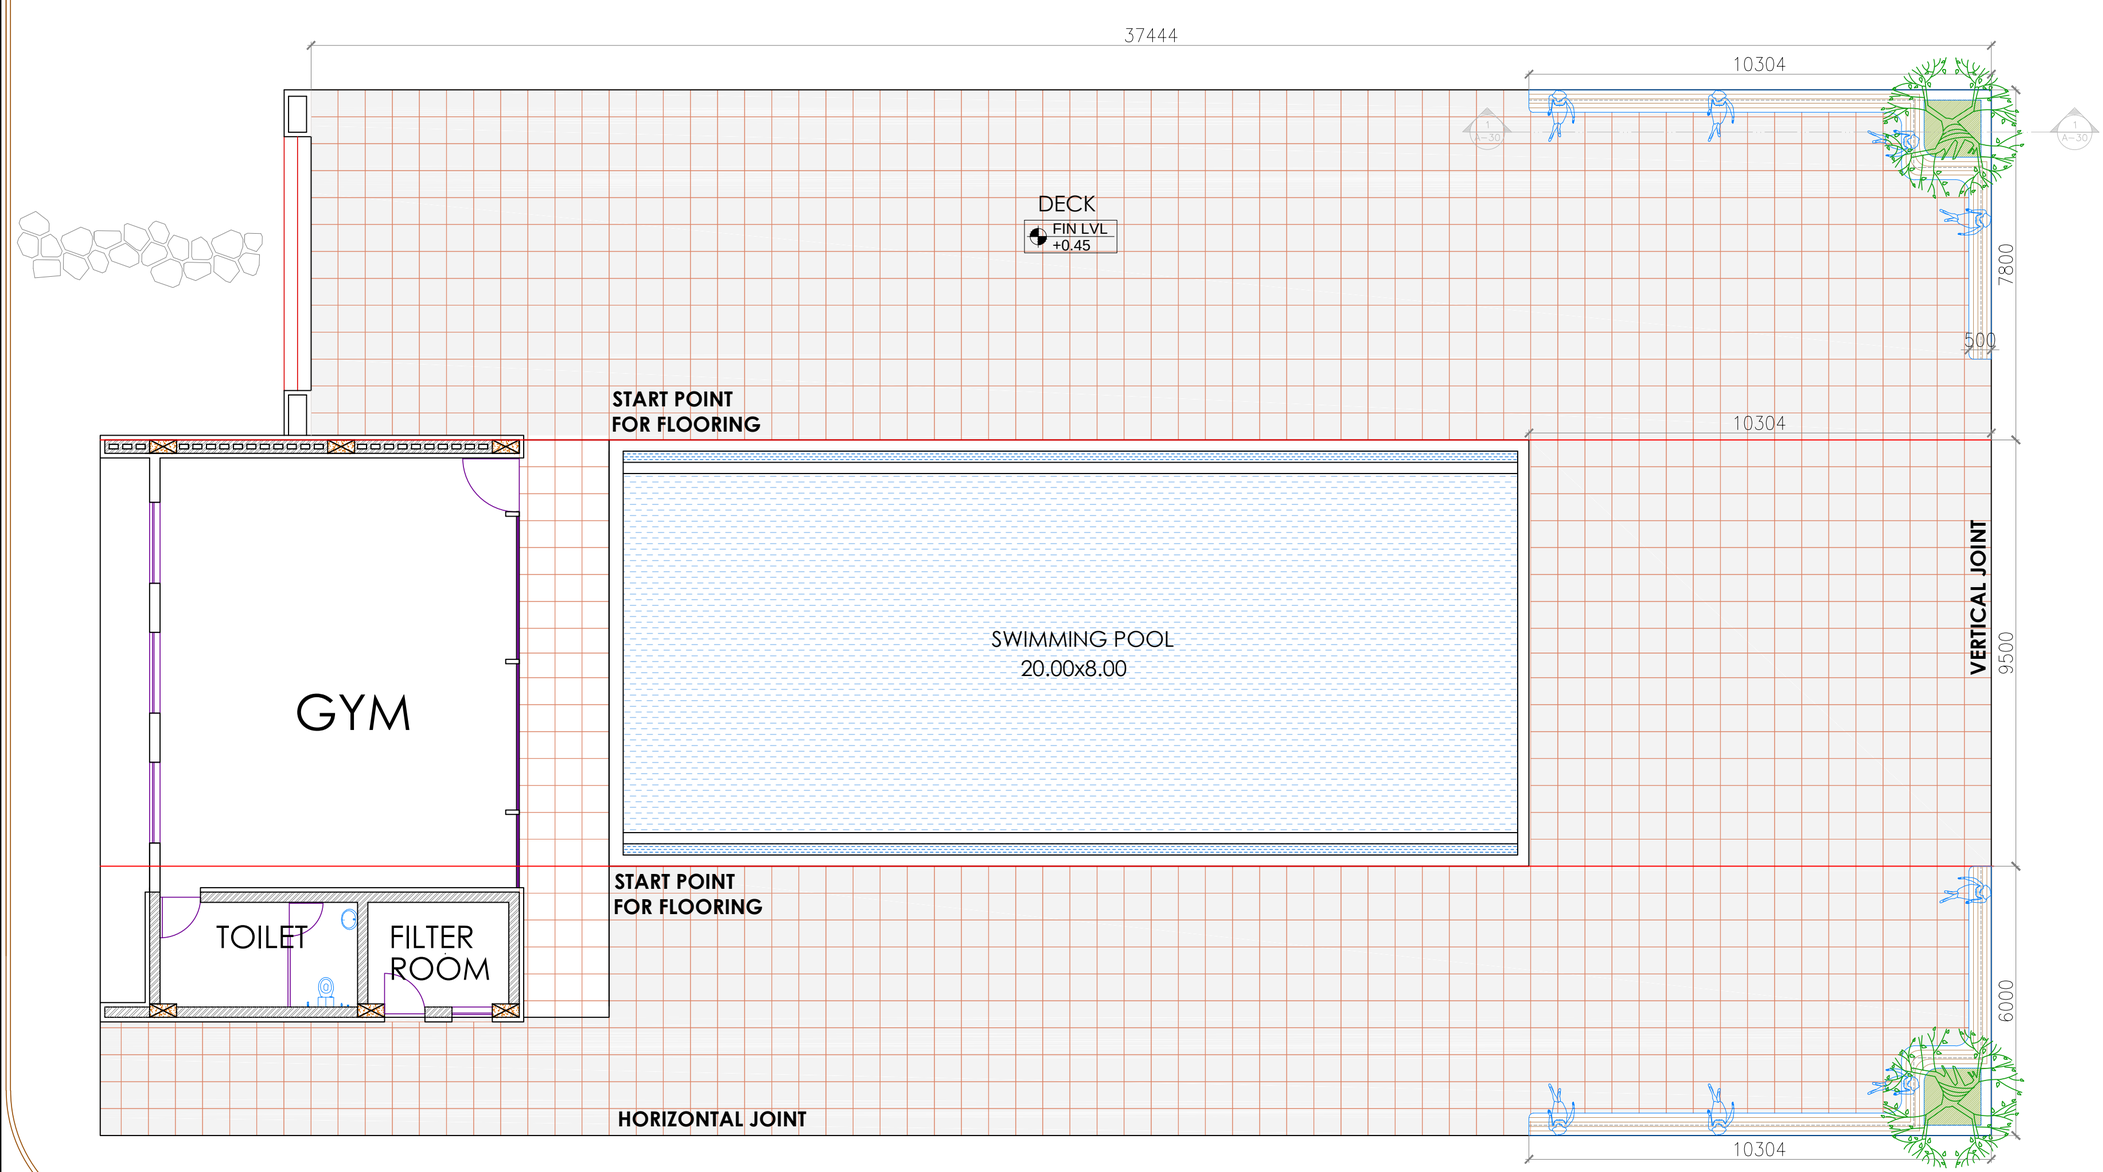

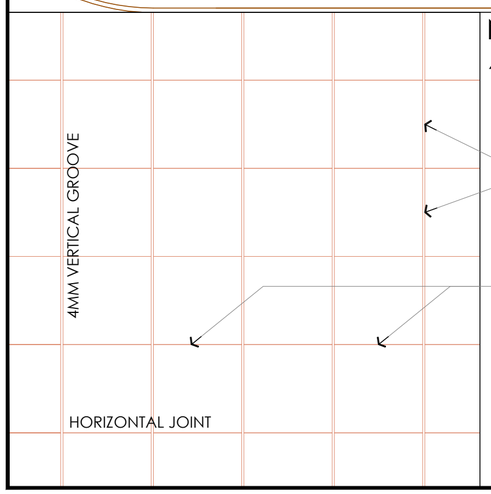

NOTE - 600x600 MM TILES WITH
4MM VERTICAL GROOVE

4MM VERTICAL GROOVE

0.00 MM HORIZONTAL JOINT

DRAWING NO.	EP-00

STAMP AND SIGN
*NOTE- LANDSCAPE PLAN

		R6
		R5
		R4
		R3
		R2
		R1
DATE	SUBJECT	REV

TAGS

P-CON	READ DWG IN CONJUNCTION WITH PLUMBING CONSULTANT'S DWG
S-CON	READ DWG IN CONJUNCTION WITH STRUCTURAL CONSULTANT'S DWG

ABBREVIATIONS

S.B	SHRUB BED	T.P	TOP OF PLANTER
R.P	RAISED PLANTER	W.L	WATER LEVEL
T.W	TOP OF WALL	B.L	BOTTOM LEVEL
T/WALL	TOP OF WALL		

GENERAL NOTES

1. ALL DIMENSIONS ARE IN METERS UNLESS NOTED.

2. DRAWING NOT TO BE SCALED. WRITTEN DIMENSIONS TO BE FOLLOWED ONLY.

3. DIMENSIONS SHOULD BE CHECKED AND VERIFIED ON SITE BEFORE EXECUTION. OF WORK. ANY AMBIGUITY SHALL BE IMMEDIATELY BROUGHT TO THE NOTICE OF THE LANDSCAPE ARCHITECT BEFORE COMMENCEMENT OF THE WORK.

4. SIZES OF ALL THE STRUCTURAL MEMBERS TO BE CONFIRMED BY THE STRUCTURAL CONSULTANT.

5. READ THIS DRAWING IN CONJUNCTION WITH LW/RH/01,RH/03

DRAWINGS ISSUED FOR:

ADVANCE COPY	☒	OFFICE RECORD	☐
STRUCTURAL DESIGN	☐	EXECUTION ON SITE	☐
MUNICIPAL SUBMISSION	☐	TENDER DRAWING	☐
DATE OF ISSUE:		SIGN	

DATE	AGENCY	REV.NO.	NO.OF COPIES

ARCHITECTS:
AR.SHARADCHANDRA H. BHOSALE

DWG TITLE:
SWIMMING POOL DECK
FLOORING LAYOUT

PROJECT:
PROPOSED LANDSCAPE FOR
MR. RANJIT SINGH AT SOLAPUR.

ALL DRAWINGS AND WRITTEN MATERIAL APPEARING HEREIN CONSTITUTE ORIGINAL AND UNPUBLISHED WORK OF THE ARCHITECTS 'SWATI ARINGALE'. AND MAY NOT BE DUPLICATED, USED OR DISCLOSED WITHOUT THE WRITTEN CONSENT OF THE ARCHITECTS.

SWATI ARINGALE
LAND SCAPE DESIGNERS
72 'SHANTIVAN',
RANGARGAON , LONAVLA. 410401.
PHONE: (95/02114) 272038

N

PROJECT NO.	SCALE	DATE	NORTH
2301	NTS	08-02-2023	
DEALT BY	CHKD BY	DRG No.	SHEET No.
Rituja	Swati	EP-00	1 / 1

PRODUCED BY AN AUTODESK EDUCATIONAL PRODUCT
PRODUCED BY AN AUTODESK EDUCATIONAL PRODUCT
PRODUCED BY AN AUTODESK EDUCATIONAL PRODUCT