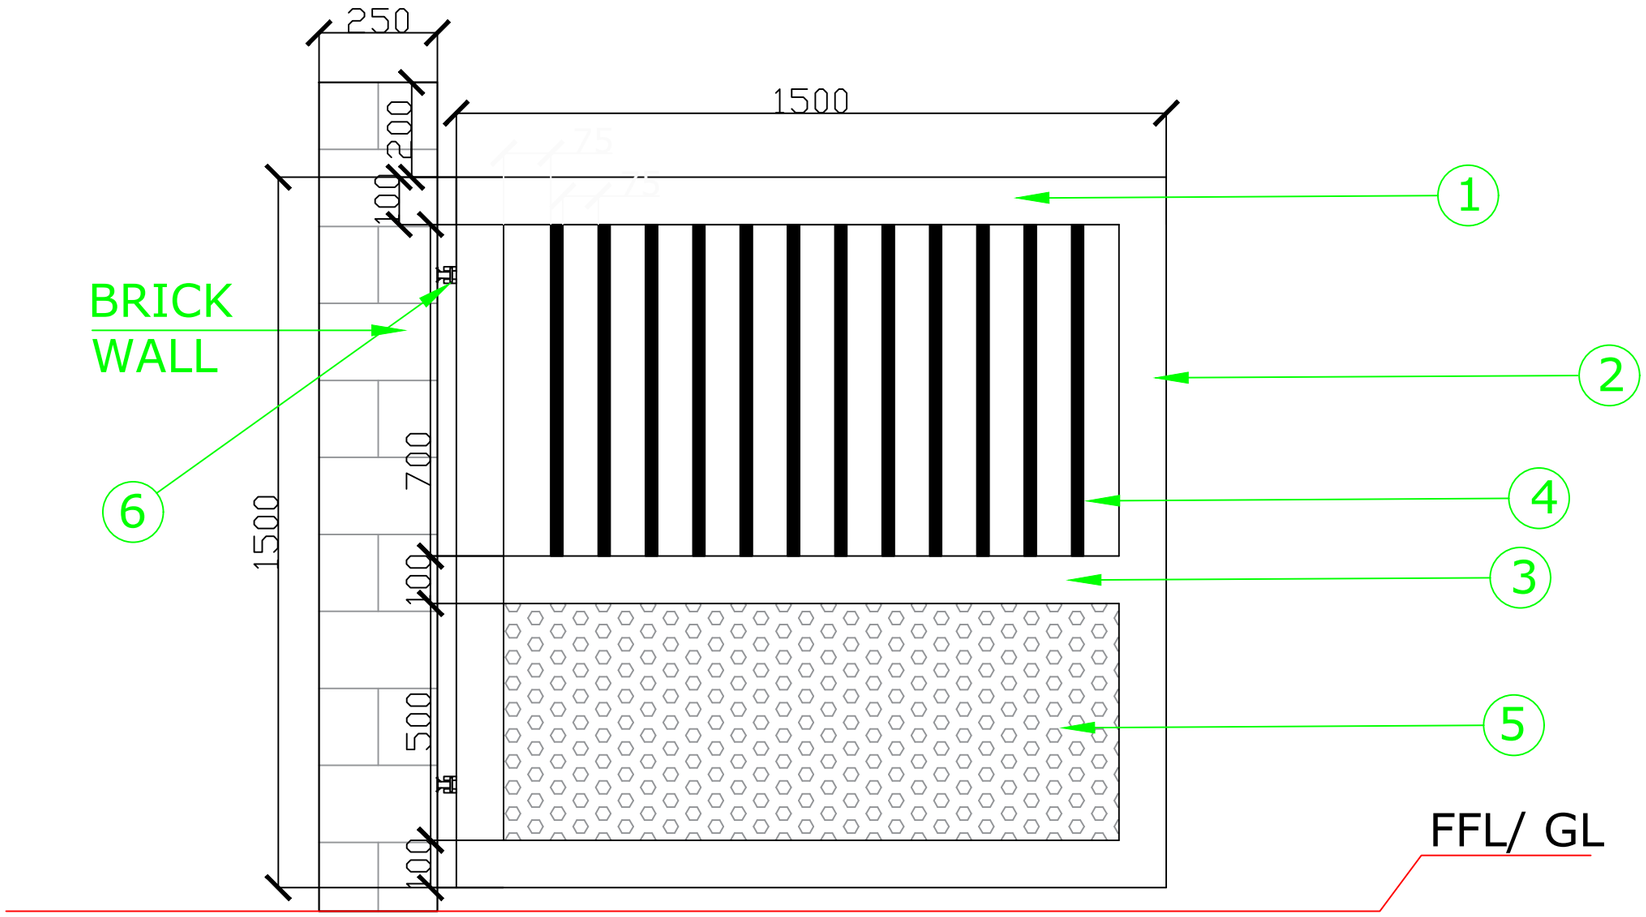



## GATE SIZES :-

| SR. | CLEAR WIDTH | CLEAR HEIGHT | QTY. |
|---|---|---|---|
| 01 | 1500 mm | 1500 mm | 01 |

| SR.NO | DESCRIPTION | LENGTH (M) | QTY |
|---|---|---|---|
| 1 | MS.RQ. TUBE 100X50X2.5 THK | 1.5 | 03 |
| 2 | MS.RQ. TUBE 100X50X2.5 THK | 1.5 | 02 |
| 3 | MS.RQ. TUBE 100X50X2.5 THK | 0.5 | 04 |
| 4 | MS.SQ. TUBE 25X25X2.0 THK | 1.0 | 12 |
| 5 | PERFORATED SHEET 1300X500X2.0MM THK | | 01 |
| 6 | HINGES | | 02 |

This drawing & designing is the property of NIHVA TECHNOLOGIES. Not to be sold or copied to any other concern.

TITLE :- WICKET GATE

NIHVA TECHNOLOGIES PVT. LTD. PUNE
Tel : 020 66304033
Email:- info@nihva.com
Website:- www.nihva.com

| | NAME | DATE |
|---|---|---|
| DRAWN | S.J. | 18/11/2024 |
| CHECK | K.T. | 18/11/2024 |
| APPROVAL | V.T. | 18/11/2024 |

CLIENT - REWARD CON.
PROJECT - WICKET GATE
FORMAT NO - NIHVA-DD-F-03
DWG. NO. : NIHVA/24-25/XX00 | REV-00
SCALE: NTS | WT: | SHEET: 01 OF 01
ALL DIMENSION ARE IN mm
If any queries contact : design@nihva.com