


PRODUCED BY AN AUTODESK EDUCATIONAL PRODUCT

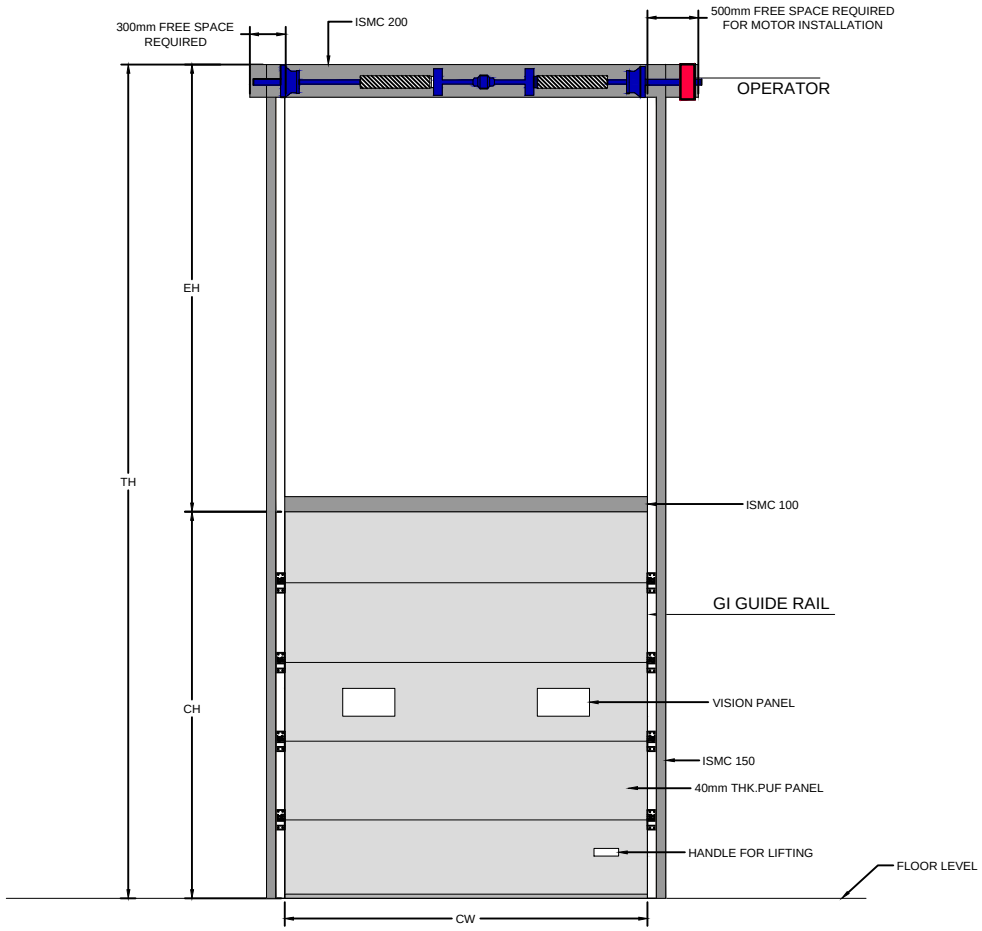


INSIDE VIEW

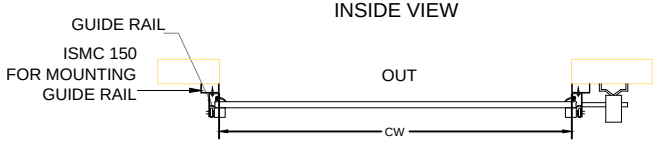

TOP VIEW

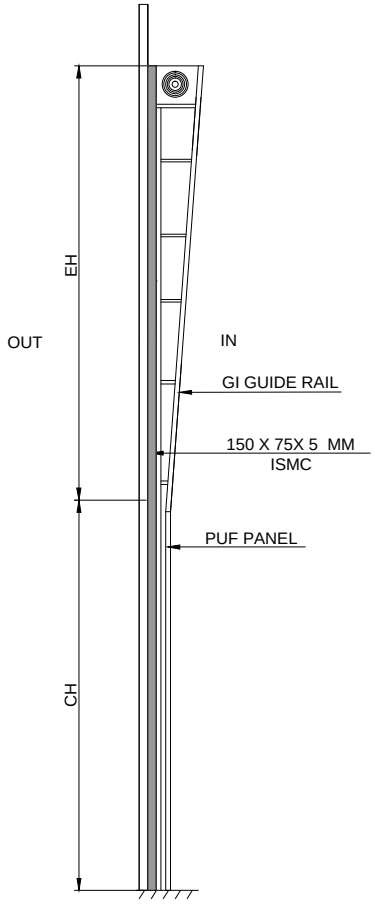

CROSS VIEW

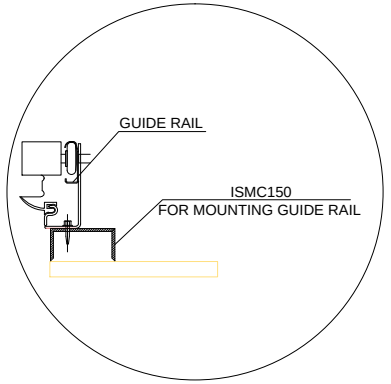

COLORS -1. RAL 9010 (Pure White)
2. RAL 7016 (Anthracite Gray)
3. RAL 9006 (White Aluminum)

SR NO	CLEAR WIDTH	CLEAR HEIGHT	QTY	TH	EH
1	4000mm	6000mm	12	12500	6300
2	5500mm	6000mm	1	12500	6300
3	5500mm	6500mm	2	13500	6856

This drawing & design is the property of NIHVA TECHNOLOGIES. Not to be sold or copied to any other concern.

TITLE
SECTIONAL DOOR

NIHVA TECHNOLOGIES PVT. LTD.
NIHVA TECHNOLOGIES PVT. LTD. PUNE
Tel : 020 66304033
Email:- info@nihva.com
Website:- www.nihva.com

	SIGN	DATE
DRAWN	OMKAR	13/04/17
CHECK	SAGAR P.	13/04/17
REV.		
APPROVAL		

CLIENT - TATA PROJECTS
PROJECT -
SITE - HYDERABAD , A.P.
DWG. NO. : NIHVA/17-18/0008
If any queries contact : projects@nihva.com
SCALE: NTS | WT: | SHEET: 01 OF 01
ALL DIMENSION ARE IN mm

PRODUCED BY AN AUTODESK EDUCATIONAL PRODUCT
PRODUCED BY AN AUTODESK EDUCATIONAL PRODUCT
PRODUCED BY AN AUTODESK EDUCATIONAL PRODUCT