


NOTE : ~ PLEASE MAINTAIN 8 MM GAP BETWEEN TWO LIP BUSHES.

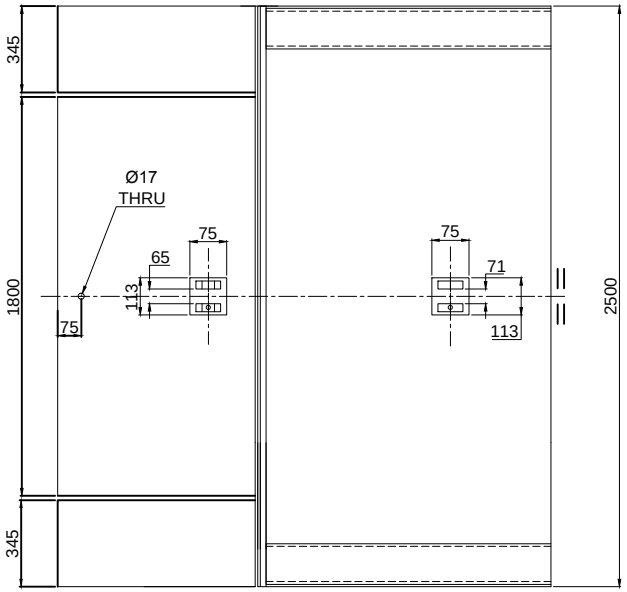



1

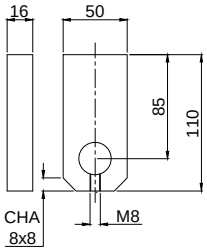

2

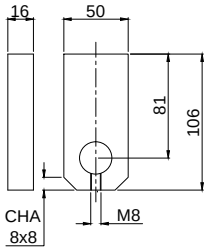

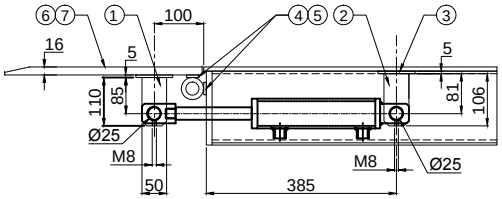

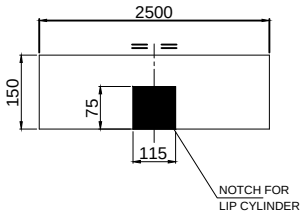

NOTE:~ MTL : MS

PART NO.	PART NAME	DESCRIPTION	QTY
1.	FLAT	50 X 16 X 113L	2 NOS
2.	FLAT	50 X 16 X 110L	2 NOS
3.	FLAT	75 X 5 X 113L	2 NOS
4.	FLAT	25 X 5 X 80L	14 NOS
5.	FLAT	25 X 5 X 60L	8 NOS
6.	PROFILE	300 X 16 X 1800L	1 NO
7.	PROFILE	300 X 16 X 345L	2 NOS

TOLERANCE - ±5mm

REV NO	DRAWN	DATE	DESCRIPTION
R01	P.A	18.12.18	1. LIP SIZE CHANGE.

This drawing & design is the property of NIHVA TECHNOLOGIES. Not to be sold or copied to any other concern.

TITLE

LIP CYL MOUNTING

NIHVA TECHNOLOGIES PVT. LTD.

NIHVA TECHNOLOGIES PVT. LTD. PUNE
Tel : 020 66304033
Email:- info@nihva.com
Website:- www.nihva.com

	NAME	SIGN	DATE
DRAWN	P.A		12.12.18
CHECK	P.A		12.12.18
APPRD.	P.A		12.12.18

If any queries contact : design@nihva.com

ALL DIMENSION ARE IN mm

CLIENT -

PROJECT - DLAG1010

SITE LOCATION -

DWG. NO. : NIHVA/18-19/MFG/DLAG1010/006/R01

SCALE: NTS | WT: | REV- R01