
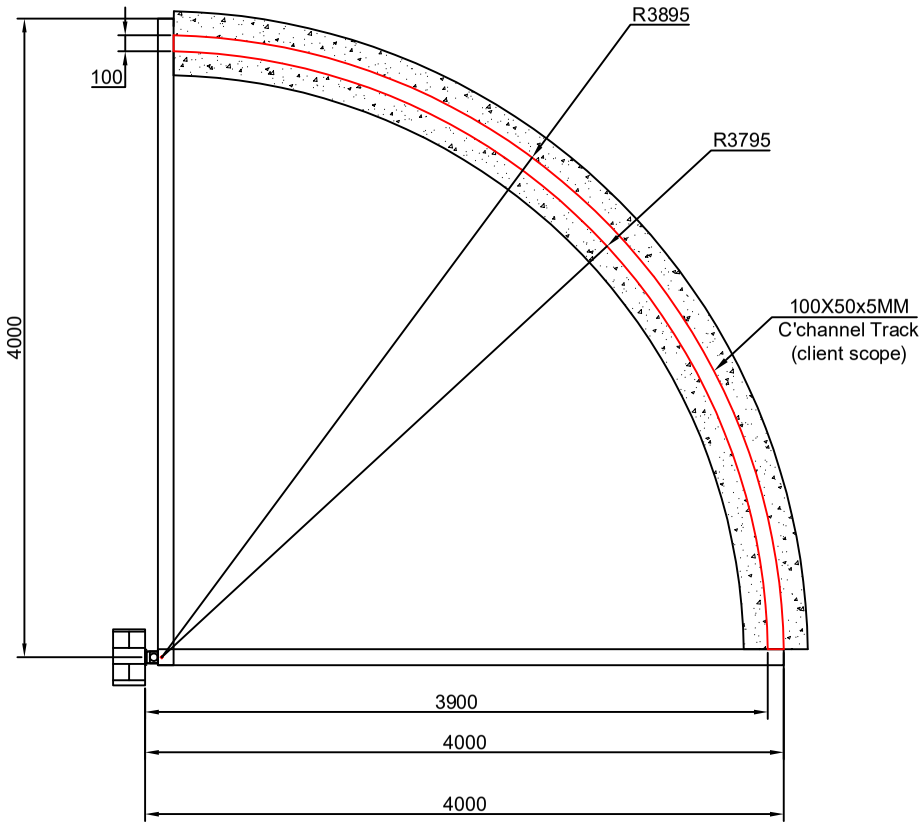


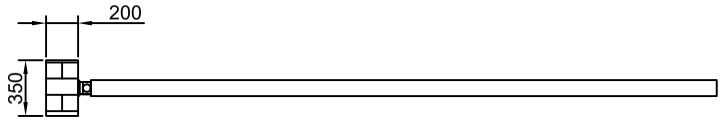

Note:-

1.All dimension are in mm.

2.All civil work is in client scope.

This drawing & design is the property of NIHVA TECHNOLOGIES. Not to be sold or copied to any other concern.

TITLE:- SWING GATE FOUNDATION DRAWING				NIHVA TECHNOLOGIES PVT. LTD. PUNE Tel : 020 66304033 Email:- info@nihva.com Website:- www.nihva.com
	NAME	DATE	SIGN	
DRAWN	SUJATA.B	31/01/2022		CLIENT - Fanidhar Mega Food Park Private Limited
CHECK	G.PATIL	31/01/2022		LOCATION - GUJARAT
APPRD.	A.K	31/01/2022		PRODUCT - SWING GATE
If any queries contact : design@nihva.com				DWG NO:-NIHVA/21-22/CLT/0305 REV- 1
ALL DIMENSION ARE IN mm				SCALE: NTS SCALE:-- 1:1 SHEET: 01 OF 01

Rev No.	Revision	Date	Revised By