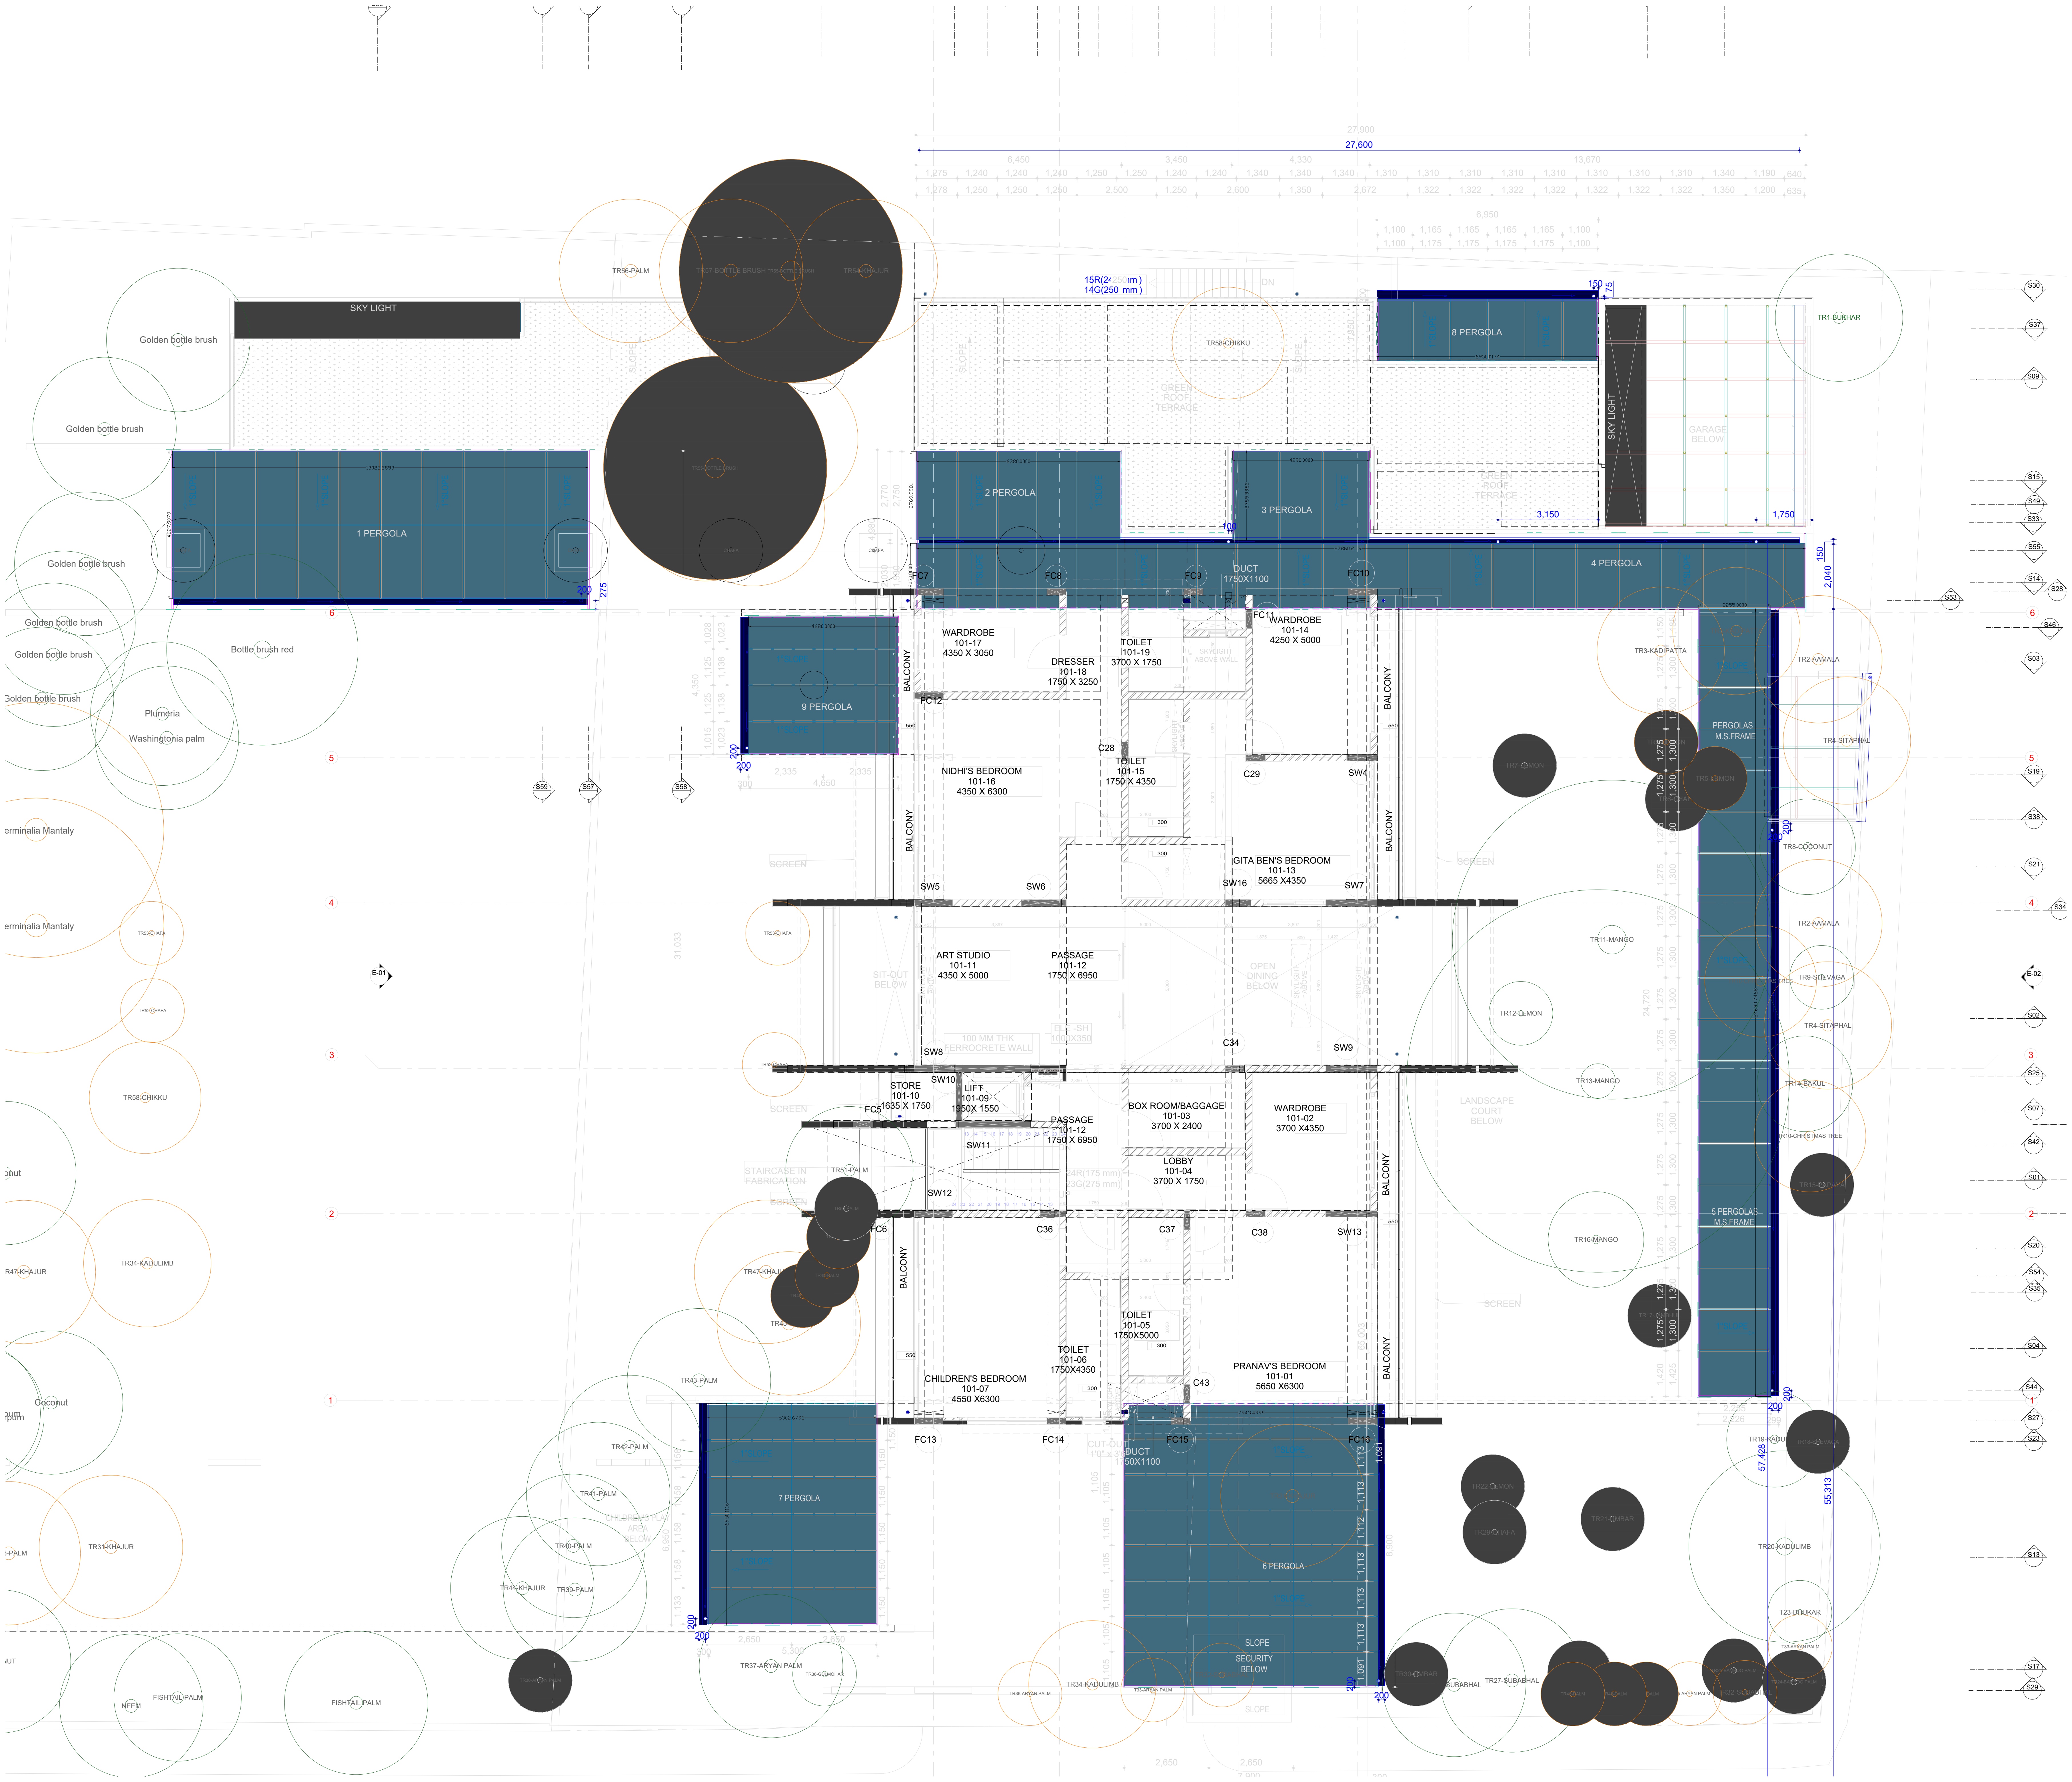
27,600
SKY LIGHT
1 PERGOLA
2 PERGOLA
3 PERGOLA
4 PERGOLA
5 PERGOLAS
M.S FRAME
6 PERGOLA
7 PERGOLA
8 PERGOLA
9 PERGOLA
PERGOLAS
M.S.FRAME
SKY LIGHT
GARAGE BELOW
15R(250 mm)
14G(250 mm)
DN
3,150
1,750
DUCT
1750X1100
FC7
FC8
FC9
FC10
FC11
FC12
WARDROBE
101-17
4350 X 3050
DRESSER
101-18
1750 X 3250
TOILET
101-19
3700 X 1750
WARDROBE
101-14
4250 X 5000
SKYLIGHT ABOVE WALL
BALCONY
C28
TOILET
101-15
1750 X 4350
NIDHI'S BEDROOM
101-16
4350 X 6300
C29
SW4
GITA BEN'S BEDROOM
101-13
5665 X4350
SW5
SW6
SW16
SW7
ART STUDIO
101-11
4350 X 5000
PASSAGE
101-12
1750 X 6950
SIT-OUT BELOW
OPEN DINING BELOW
SKYLIGHT ABOVE
100 MM THK FERROCRETE WALL
ELE -SH 1000X350
SW8
C34
SW9
STORE
101-10
1635 X 1750
SW10
LIFT
101-09
1950X 1550
FC5
PASSAGE
101-12
1750 X 6950
BOX ROOM/BAGGAGE
101-03
3700 X 2400
WARDROBE
101-02
3700 X4350
LOBBY
101-04
3700 X 1750
SW11
SW12
24R(175 mm)
23G(275 mm)
STAIRCASE IN FABRICATION
FC6
C36
C37
C38
SW13
TOILET
101-05
1750X5000
TOILET
101-06
1750X4350
CHILDREN'S BEDROOM
101-07
4550 X6300
C43
PRANAV'S BEDROOM
101-01
5650 X6300
FC13
FC14
FC15
FC16
CUT-OUT 1'0" x 3'6"
DUCT
1750X1100
SLOPE
SECURITY BELOW
SCREEN
LANDSCAPE COURT BELOW
Golden bottle brush
Bottle brush red
Plumeria
Washingtonia palm
Terminalia Mantaly
TR56-PALM
TR57-BOTTLE BRUSH
TR58-CHIKKU
TR1-BUKHAR
TR3-KADIPATTA
TR2-AAMALA
TR4-SITAPHAL
TR8-COCONUT
TR11-MANGO
TR12-LEMON
TR13-MANGO
TR9-SHEVAGA
TR14-BAKUL
TR16-MANGO
TR19-KADU
TR20-KADULIMB
T23-BUKHAR
TR27-SUBABHAL
TR34-KADULIMB
TR31-KHAJUR
TR47-KHAJUR
TR43-PALM
TR42-PALM
TR41-PALM
TR40-PALM
TR44-KHAJUR
TR39-PALM
TR37-ARYAN PALM
TR51-PALM
Coconut
NEEM
FISHTAIL PALM
E-01
E-02
1
2
3
4
5
6
S30
S37
S09
S15
S49
S33
S55
S14
S28
S53
S46
S03
S19
S38
S21
S34
S02
S25
S07
S42
S01
S20
S54
S35
S04
S44
S27
S23
S13
S17
S29
S59
S57
S58
57,428
55,313