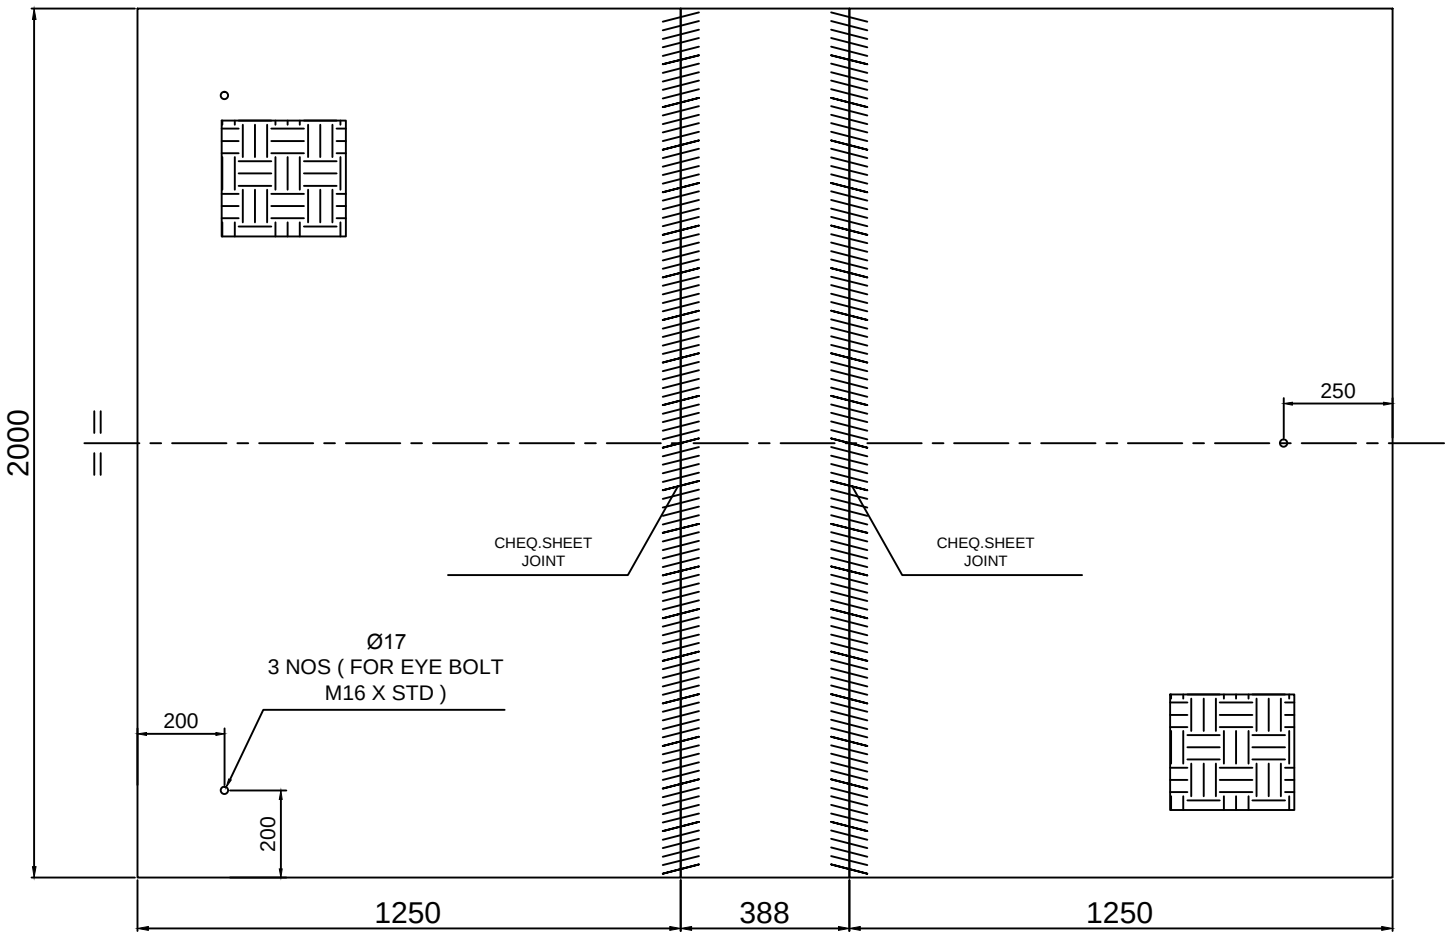


This drawing & design is the property of NIHVA TECHNOLOGIES. Not to be sold or copied to any other concern.

TITLE

DECK CHEQ.SHEET

NIHVA TECHNOLOGIES PVT. LTD.
NIHVA TECHNOLOGIES PVT. LTD. PUNE
Tel : 020 66304033
Email:- info@nihva.com
Website:- www.nihva.com

	NAME	SIGN	DATE
DRAWN	PRADEEP		05.09.2018
CHECK	PRADEEP		05.09.2018
APPRD.	PRADEEP		05.09.2018

If any queries contact : design@nihva.com

ALL DIMENSION ARE IN mm

CLIENT -

PROJECT - DLSD1009

SITE LOCATION -

DWG. NO. : NIHVA/18-19/MFG/DLSD1009/003

SCALE: NTS | WT: | REV- 00