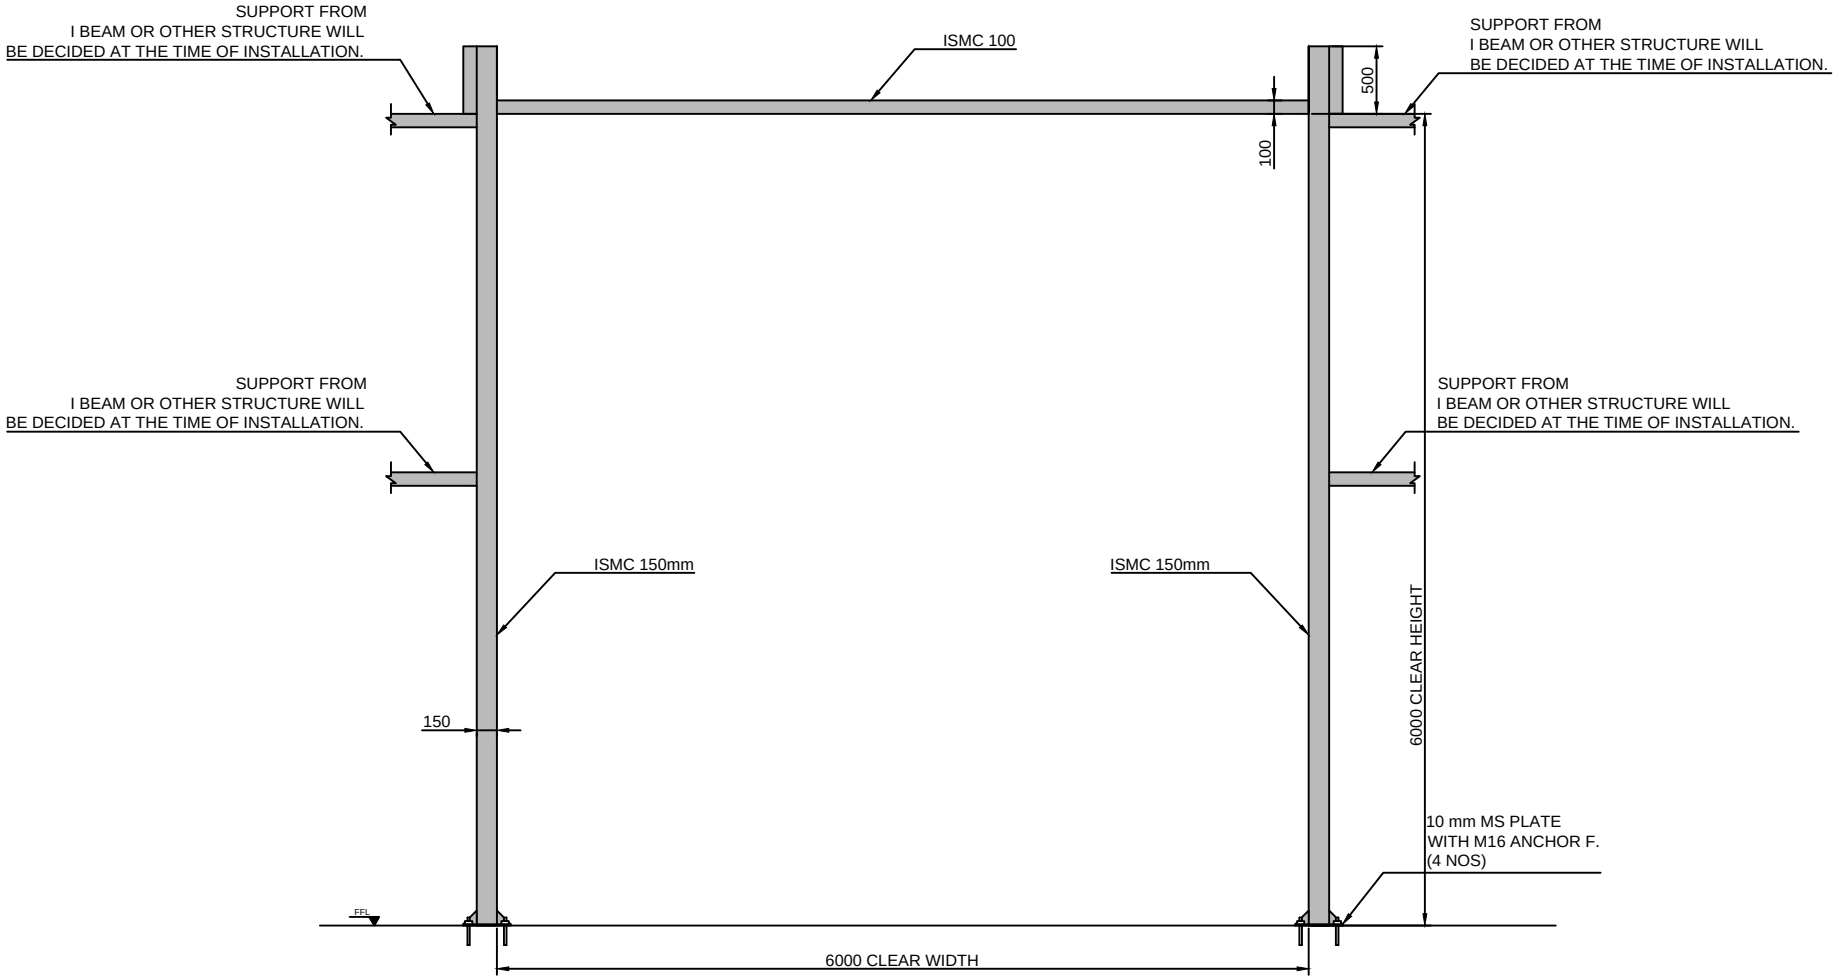

ELEVATION

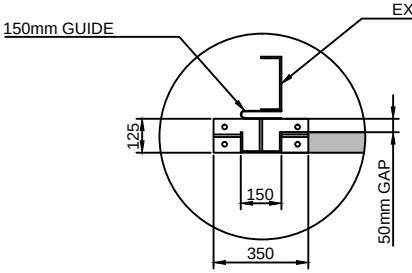

DETAILED VIEW OF A

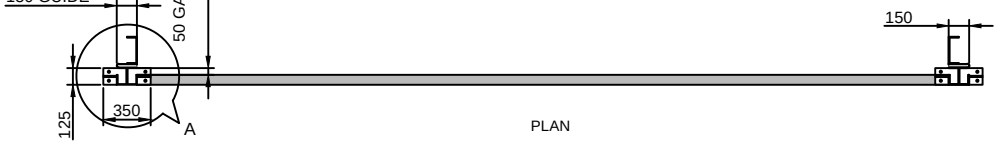

PLAN

QUANTITY- 2 NOS.

This drawing & designing is the property of NIHVA TECHNOLOGIES. Not be sold or copy to any other concern.

TITLE: STRUCTURE FOR HSD 6X6m			NIHVA TECHNOLOGY PVT. LTD. PUNE
	SIGN	DATE	Tel : 020 66304033
DRAWN	OMKAR	11/11/16	Email:- info@nihva.com
CHECK	SAGAR P.	11/11/16	Website:- www.nihva.com
REV.	0		CLIENT -
APPROVAL			PROJECT -
If any queries contact : projects@nihva.com			SITE -
ALL DIMENSION ARE IN mm			DWG. NO. : NIHVA/16-17/
			SCALE: 1:1 | WT: | SHEET: 01 OF 01