
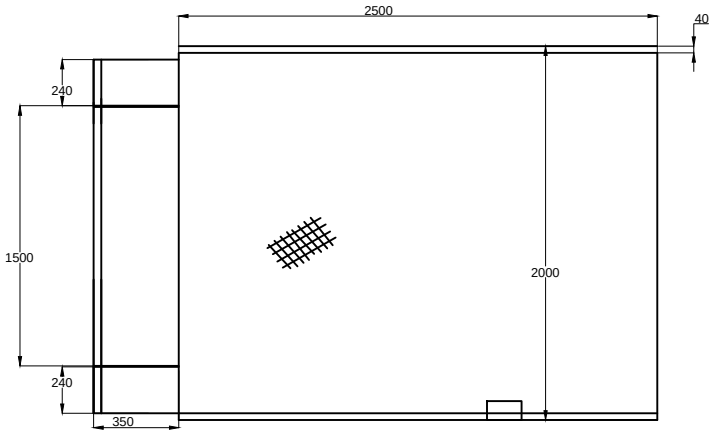
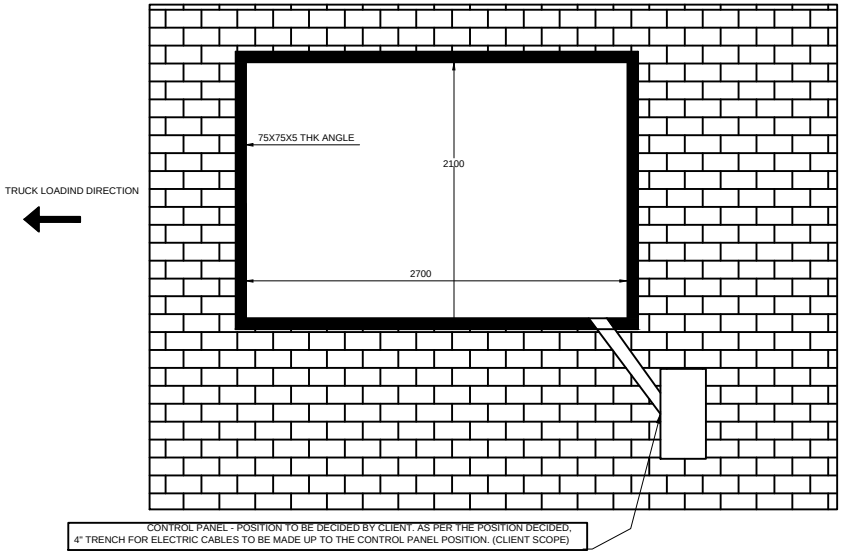
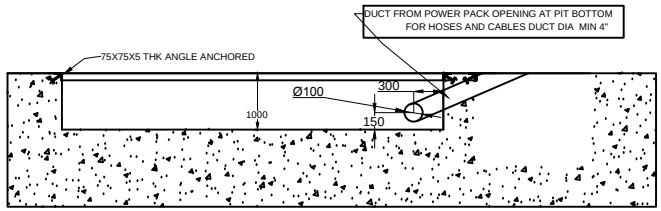



CONTROL PANEL - POSITION TO BE DECIDED BY CLIENT. AS PER THE POSITION DECIDED, 4" TRENCH FOR ELECTRIC CABLES TO BE MADE UP TO THE CONTROL PANEL POSITION. (CLIENT SCOPE)

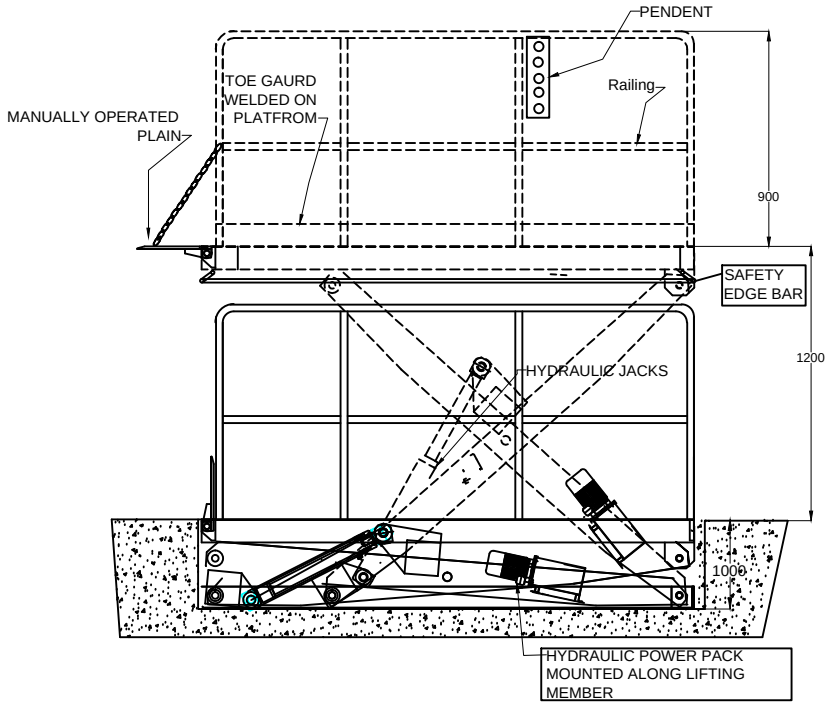


PIT DRAWING

NOTE :
1. PIT FOR SCISSORLIFT HAS TO BE DIAGONALLY WITHIN 3-5 MM
2. BASE OF THE PIT HAS TO BE IN WATER LEVEL AND RIGHT ANGLE TO THE VERTICAL SIDE WALLS
3. PROPER ARRANGEMENT FOR ROUTING HOSES AND CABLES HAVE TO BE MADE DEPENDING ON SITE CONDITIONS AND POSITION OF POWER PACK
4. COVERING REQUIRED FOR CABLES AND RELATED CIVIL WORK IS IN CLIENTS SCOPE
5. WATER DRAINAGE AND PIT CLEANING NEEDS TO BE CONSIDERED AND DONE BY CLIENT

## Specifications

| | | | |
|---|---|---|---|
| | Equipment | | Scissors Lift |
| | Rated Capacity | W Kgs | 6000 |
| Dimensions | Platform Length | mm | 2500 |
| Dimensions | Platform Width | mm | 2000 |
| Dimensions | Overall Length | mm | 2150 |
| Dimensions | Overall Width | mm | 2000 |
| Dimensions | Lip One side | mm | 350 x2090 |
| Dimensions | Lip Operation | | Manual |
| Dimensions | Lip Type | | Single |
| Dimensions | Speed Lifting/Lower | | 3-4 / 2-3 |
| Dimensions | Heights Closed | mm | 1000 |
| Dimensions | Heights Lift | mm | 1200 |
| Drive | Lift Motor 3 Ph 400 V AC | H.P. | 7.5 Hp |
| Drive | Pendent | | 1 Nos |
| Drive | Lift & Lower cut-off - Yes | | |

NOTE :
1. ELECTRICAL CABLE FROM CONTROL PANEL TO PIT OPENING : 5 MTR
2. INPUT SUPPLY : 3 PHASE 400 VOLT WITH NEUTRAL.
3. SURFACE FINISH : HOT DIP GALVANIZING
4. SCISSOR LIFT WILL BE INTERLOCKED WITH SECTIONAL DOOR AND DOCK LEVELER

This drawing & designing is the property of NIHVA TECHNOLOGIES. Not be sold or copy to any other concern.

TITLE
PIT MOUNTED ELECTRO-HYDRAULIC SCISSOR LIFT WITH BELLOW

NIHVA TECHNOLOGIES PVT. LTD.
NIHVA TECHNOLOGY PVT. LTD. PUNE
Tel : 020 66304033
Email:- info@nihva.com
Website:- www.nihva.com

| | | | |
|---|---|---|---|
| | SIGN | DATE | |
| DRAWN | G.P. | 16.8.2021 | CLIENT - SHUBHSHREE ENGINEERING |
| CHECK | A.K. | 16.8.2021 | PROJECT - E+H |
| APPROVAL | V.T. | 16.8.2021 | SITE - |
| REV. | 00 | | DWG. NO. : NIHVA/21-22/209 |

If any queries contact : nihvacare@nihva.com | SCALE: NTS | WT: | SHEET: 01 OF 02

ALL DIMENSION ARE IN mm