



SECTION-AA'

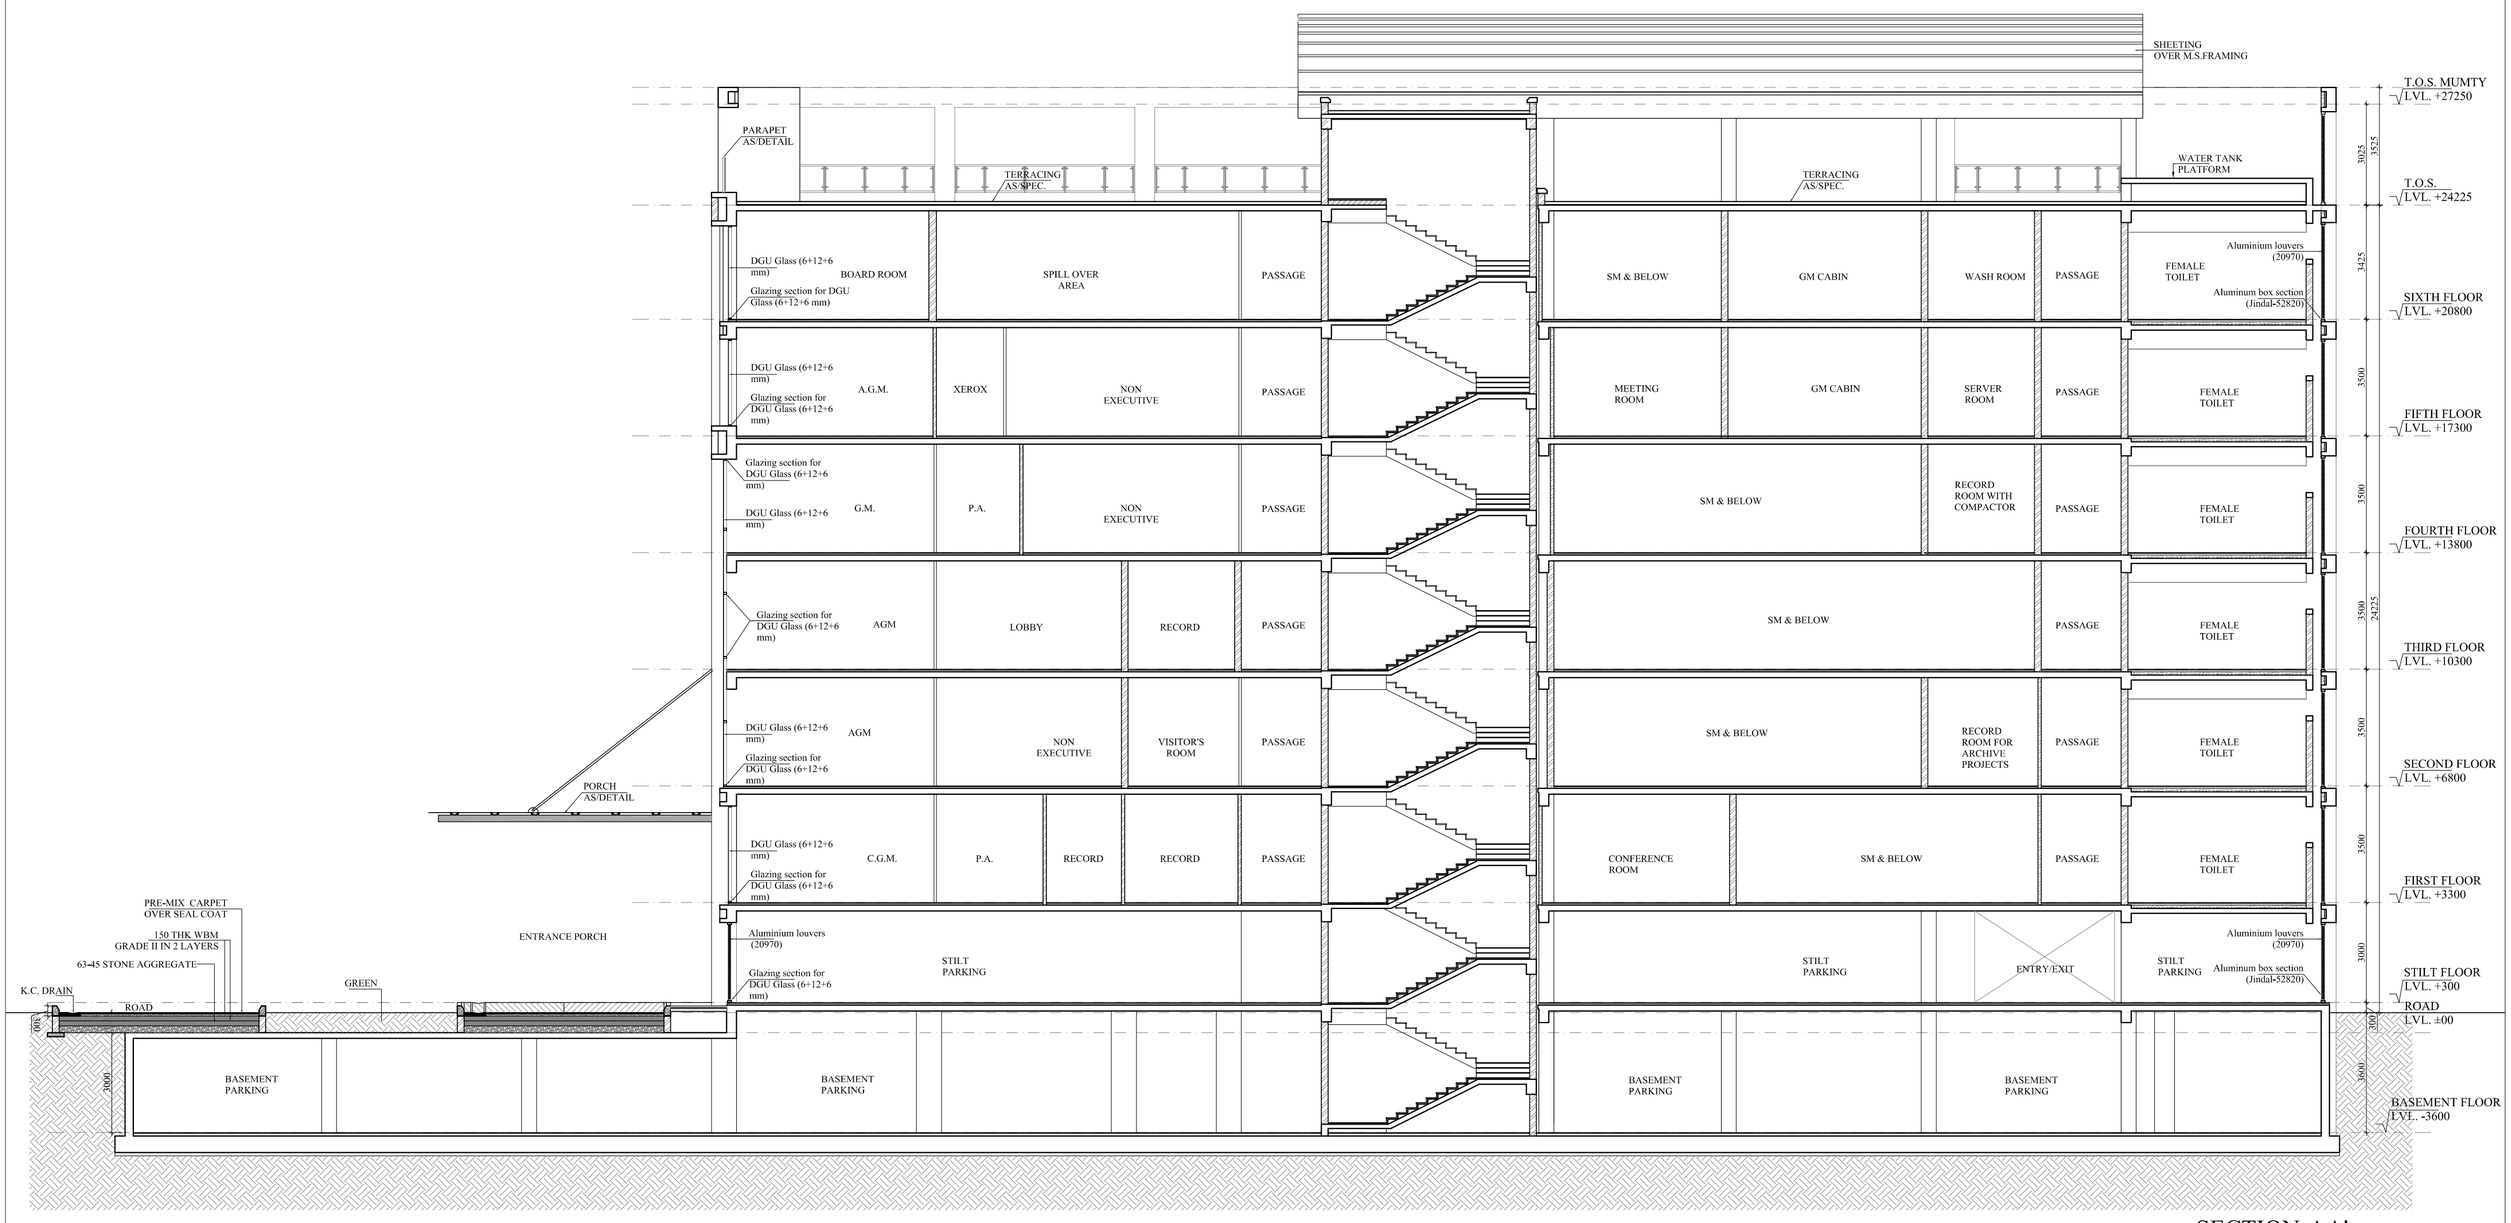

SECTION-BB'

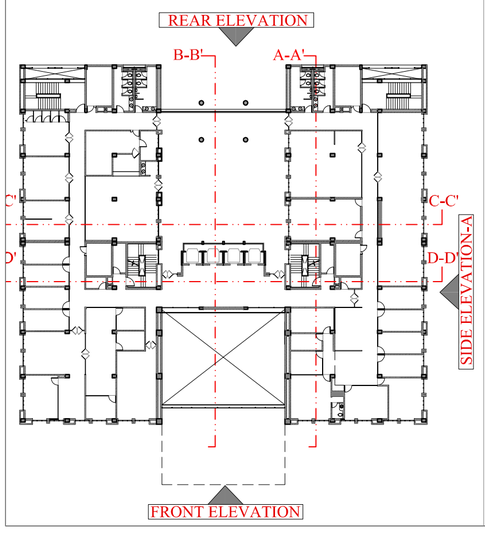

KEY PLAN

PROJECT-
CONSTRUCTION OF MCMV OFFICE BUILDING AT GOA SHIPYARD, GOA

DRAWING TITLE-
SECTIONS

OWNER-

ARCHITECTS-
DESIGN ASSOCIATES INC
A - 163, Sector - 136,
Noida - Greater Noida Expressway,
Noida - 201301, Phone no: 0120-2428600/30
e-mail: matinder.sharma@designassociates.in

NOTES:
1. ALL DIMENSIONS ARE IN MM.
2. ALL DIMENSIONS ARE TO BE READ AND NOT MEASURED.
3. ALL LEVELS ARE IN METERS.
4. GRID DIMENSIONS AND PLOT LINES ARE TO BE STRICTLY ADHERED TO.
5. ALL LEVELS INCLUDING FLOOR LEVELS, CILL & LINTEL LEVELS, LANDING LEVELS, PARAPET HEIGHT/ LEVELS, LEVELS OF HORIZONTAL PROJECTION & BONDS INCLUDING ANY SURFACE FEATURES INDICATED IN THE DRAWINGS ARE TO BE STRICTLY ADHERED TO.

THIS DRAWING IS THE PROPERTY OF THE DESIGN ASSOCIATES INC. AND SHALL NOT BE COPIED OR USED IN ANY MANNER WITHOUT PRIOR PERMISSION.

KEY PLAN

DRAWING PURPOSE-
WORKING DRAWING

DWG. NO.-
538/GSL/TD/AR/201

EXECUTING AGENCY-
NBCC (INDIA) LIMITED
(Formerly National Buildings Construction Limited)
(A Government of India Enterprise)
A Navratna CPSE
NBCC Bhawan, Lodhi Road
New Delhi - 110 003, India
Telephone No : 011 - 24367314 - 17, 24367573
Fax : 011 - 24366995

JOB NO. -	DWG. REF. NO.-	DATE-	SHEET SIZE-	SHEET NO-
538	----------	----------	A1	----------

SCALE-	REVISION-	DATE OF ISSUE-	DRAWN BY-	CHECKED BY-
1:110	----------	----------	RAJEEV	MATINDER


MECHANICAL CONSULTANT-
DESIGN CENTER CONSULTING ENGINEERS, NEW DELHI

ELECTRICAL CONSULTANT-
DESIGN CENTER CONSULTING ENGINEERS, NEW DELHI


PLUMBING CONSULTANT-
DESIGN CENTER CONSULTING ENGINEERS, NEW DELHI

STRUCTURE CONSULTANT-
LKT ENGINEERING CONSULTANTS LTD.
10/49, Subhash Nagar,New Delhi-110027
Phone:+011-45565818,Tel/Fax:+011-25126129
info@lktengineering.com
http://www.lktengineering.com


MARK	DATE	DESCRIPTION
R2	--------	REVISION
R1	--------	REVISION
GFC	--------	GOOD FOR CONSTRUCTION
AC	--------	ADVANCE COPY

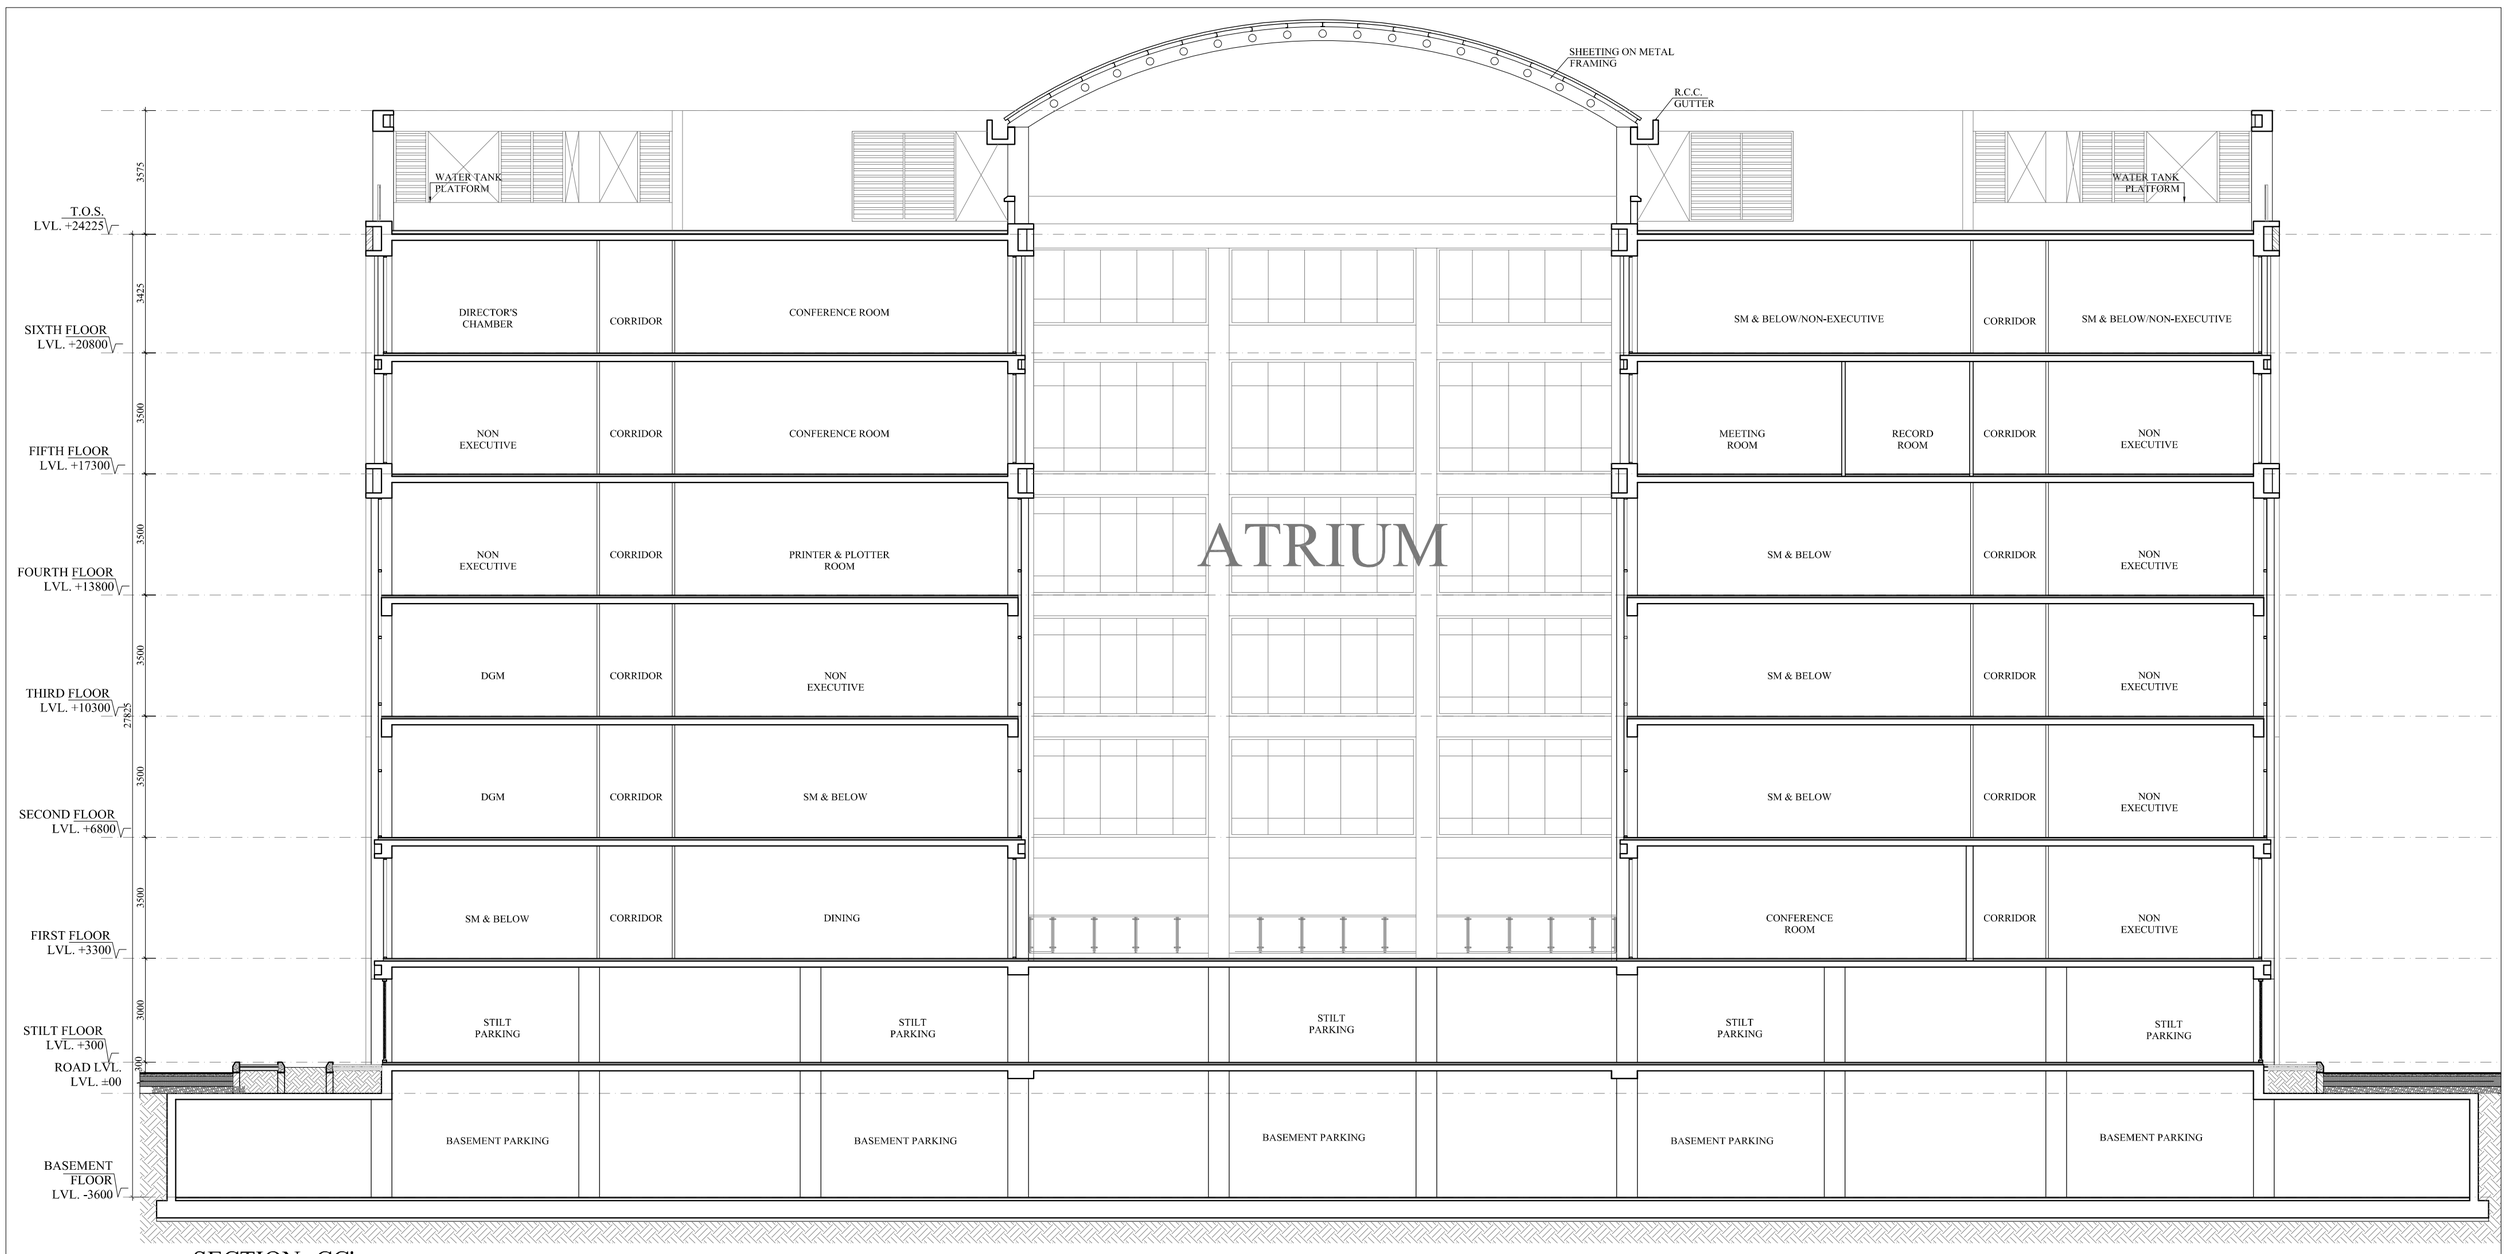

SECTION- CC'

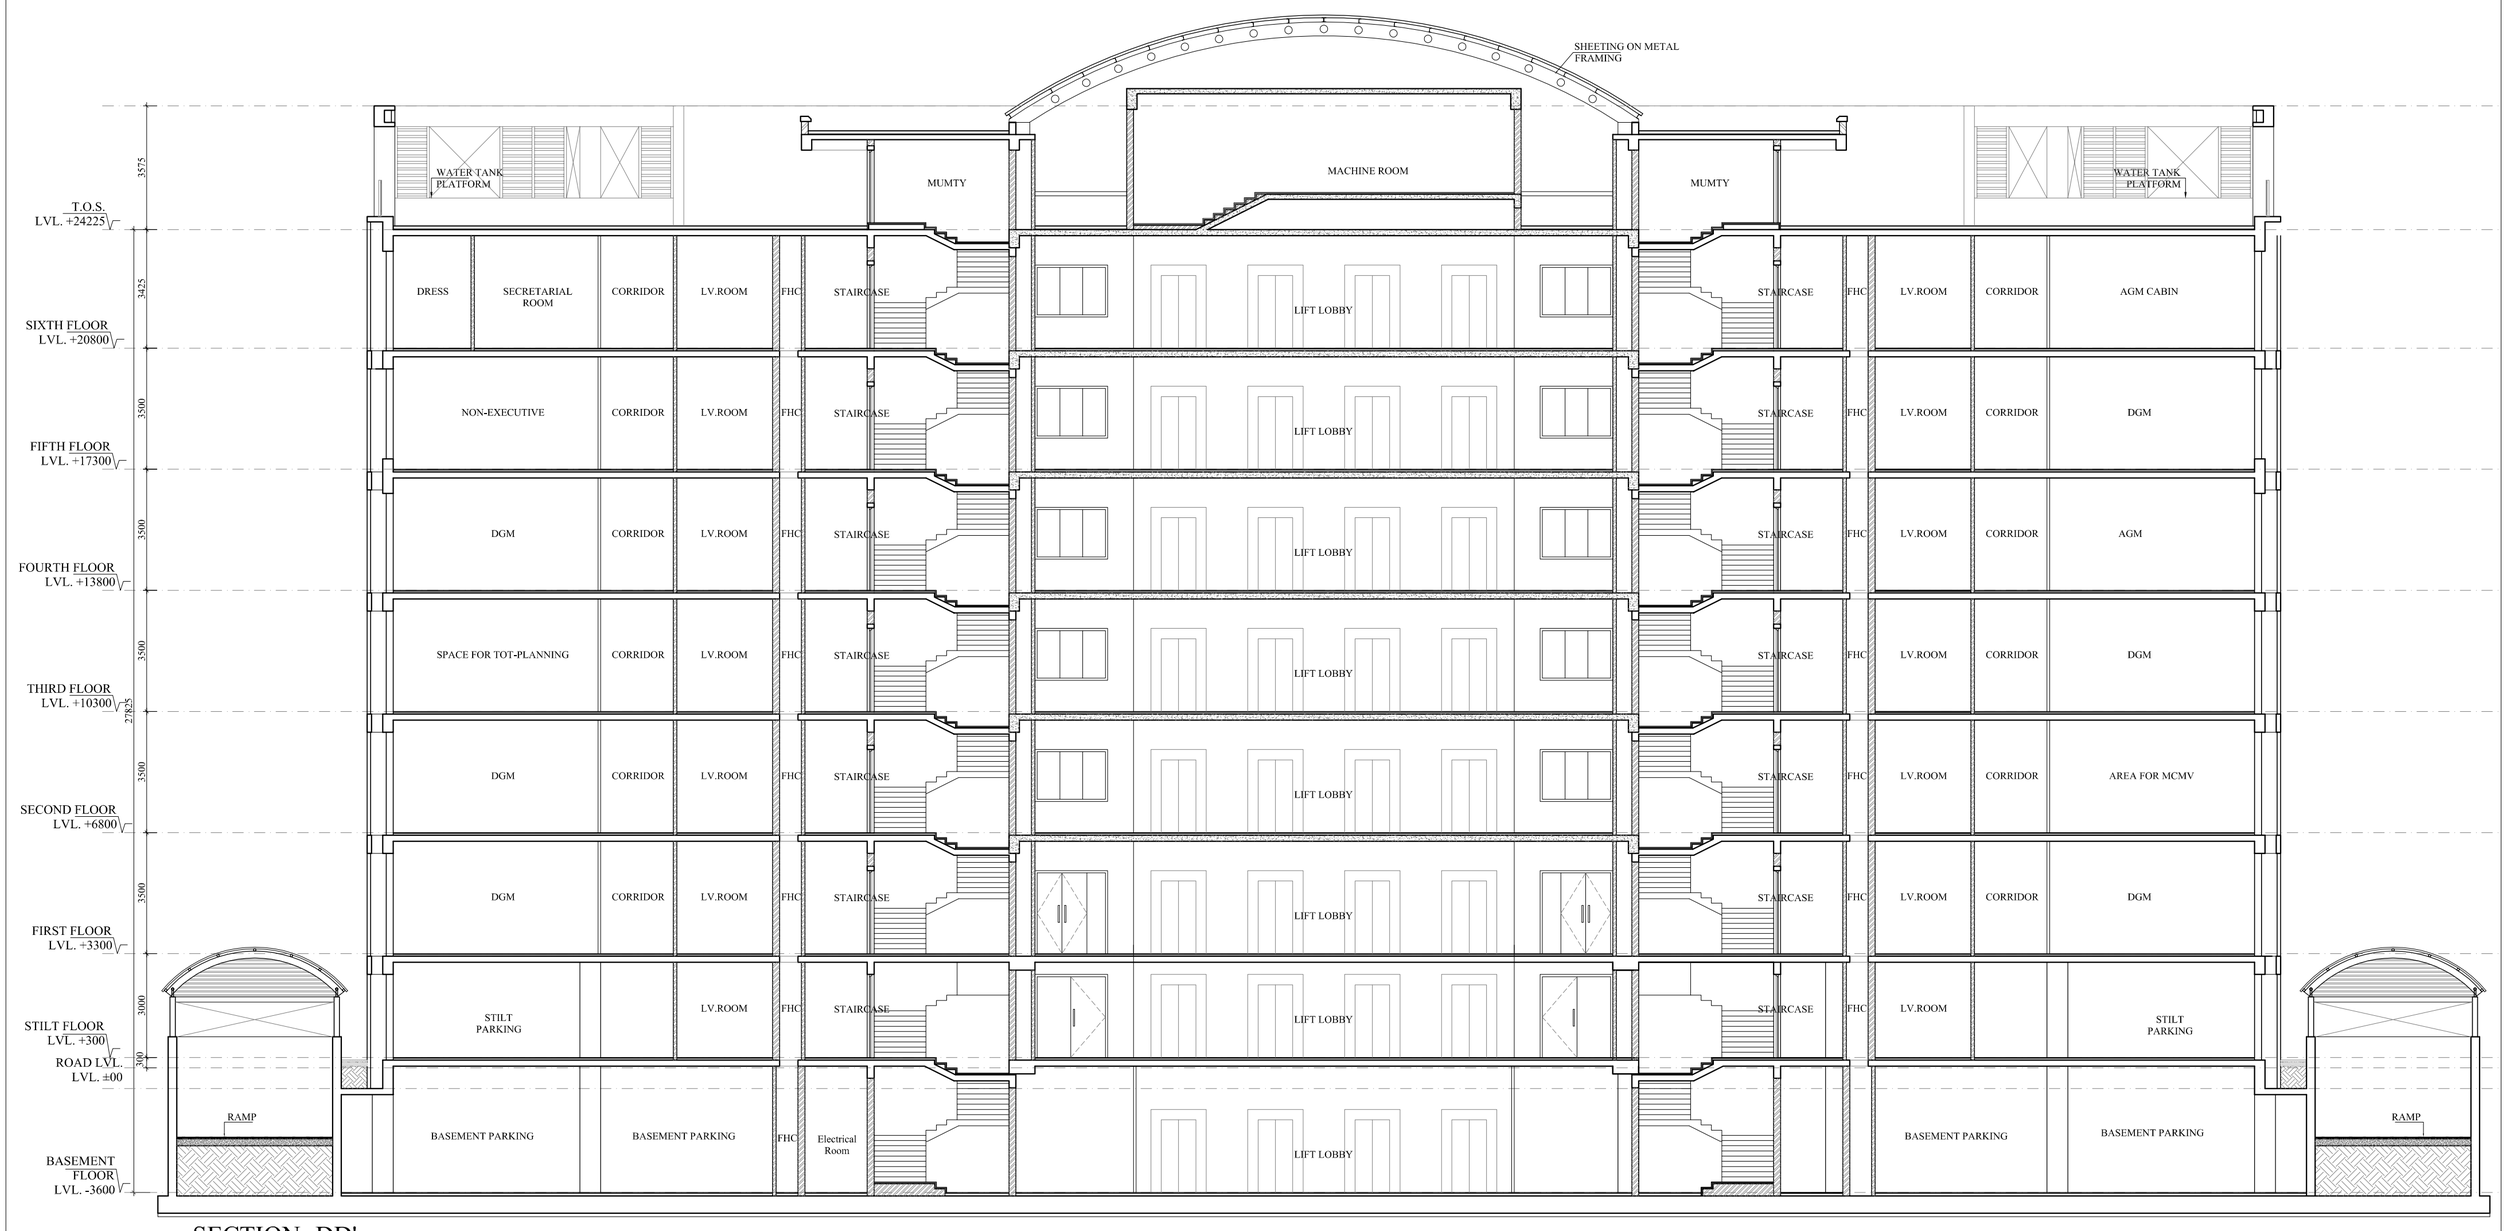

SECTION- DD'

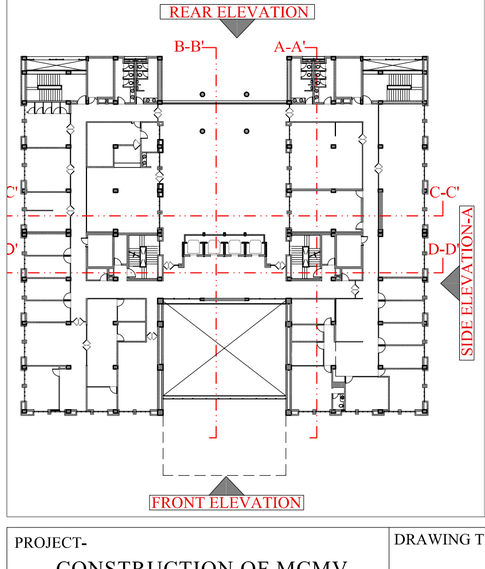

KEY PLAN

PROJECT-
CONSTRUCTION OF MCMV OFFICE BUILDING AT GOA SHIPYARD, GOA

DRAWING TITLE-
SECTIONS

OWNER-

ARCHITECTS-
DESIGN ASSOCIATES INC
A - 163, Sector - 136,
Noida - Greater Noida Expressway,
Noida - 201301, Phone no: 0120-2428600/30
e-mail: matinder.sharma@designassociates.in

NOTES:
1. ALL DIMENSIONS ARE IN MM.
2. ALL DIMENSIONS ARE TO BE READ AND NOT MEASURED.
3. ALL LEVELS ARE IN METERS.
4. GRID DIMENSIONS AND PLOT LINES ARE TO BE STRICTLY ADHERED TO.
5. ALL LEVELS INCLUDING FLOOR LEVELS, CILL & LINTEL LEVELS, LANDING LEVELS, PARAPET HEIGHT/ LEVELS, LEVELS OF HORIZONTAL PROJECTION & BONDS INCLUDING ANY SURFACE FEATURES INDICATED IN THE DRAWINGS ARE TO BE STRICTLY ADHERED TO.

THIS DRAWING IS THE PROPERTY OF THE DESIGN ASSOCIATES INC. AND SHALL NOT BE COPIED OR USED IN ANY MANNER WITHOUT PRIOR PERMISSION.

KEY PLAN

DRAWING PURPOSE-
WORKING DRAWING

DWG. NO.-
538/GSL/TD/AR/202

EXECUTING AGENCY-
NBCC (INDIA) LIMITED
(Formerly National Buildings Construction Limited)
(A Government of India Enterprise)
A Navratna CPSE
NBCC Bhawan, Lodhi Road
New Delhi - 110 003, India
Telephone No : 011 - 24367314 - 17, 24367573
Fax : 011 - 24366995

JOB NO. -	DWG. REF. NO.-	DATE-	SHEET SIZE-	SHEET NO-
538	----------	----------	A1	----------
SCALE-	REVISION-	DATE OF ISSUE-	DRAWN BY-	CHECKED BY-
1:110	----------	----------	RAJEEV	MATINDER


MECHANICAL CONSULTANT-
DESIGN CENTER CONSULTING ENGINEERS, NEW DELHI

ELECTRICAL CONSULTANT-
DESIGN CENTER CONSULTING ENGINEERS, NEW DELHI


PLUMBING CONSULTANT-
DESIGN CENTER CONSULTING ENGINEERS, NEW DELHI

STRUCTURE CONSULTANT-
LKT ENGINEERING CONSULTANTS LTD.
10/49, Subhash Nagar,New Delhi-110027
Phone:-011-45565818,Tel/Fax:-011-25126129
info@lktengineering.com
http://www.lktengineering.com


MARK	DATE	DESCRIPTION
R2	--------	REVISION
R1	--------	REVISION
GFC	--------	GOOD FOR CONSTRUCTION
AC	--------	ADVANCE COPY

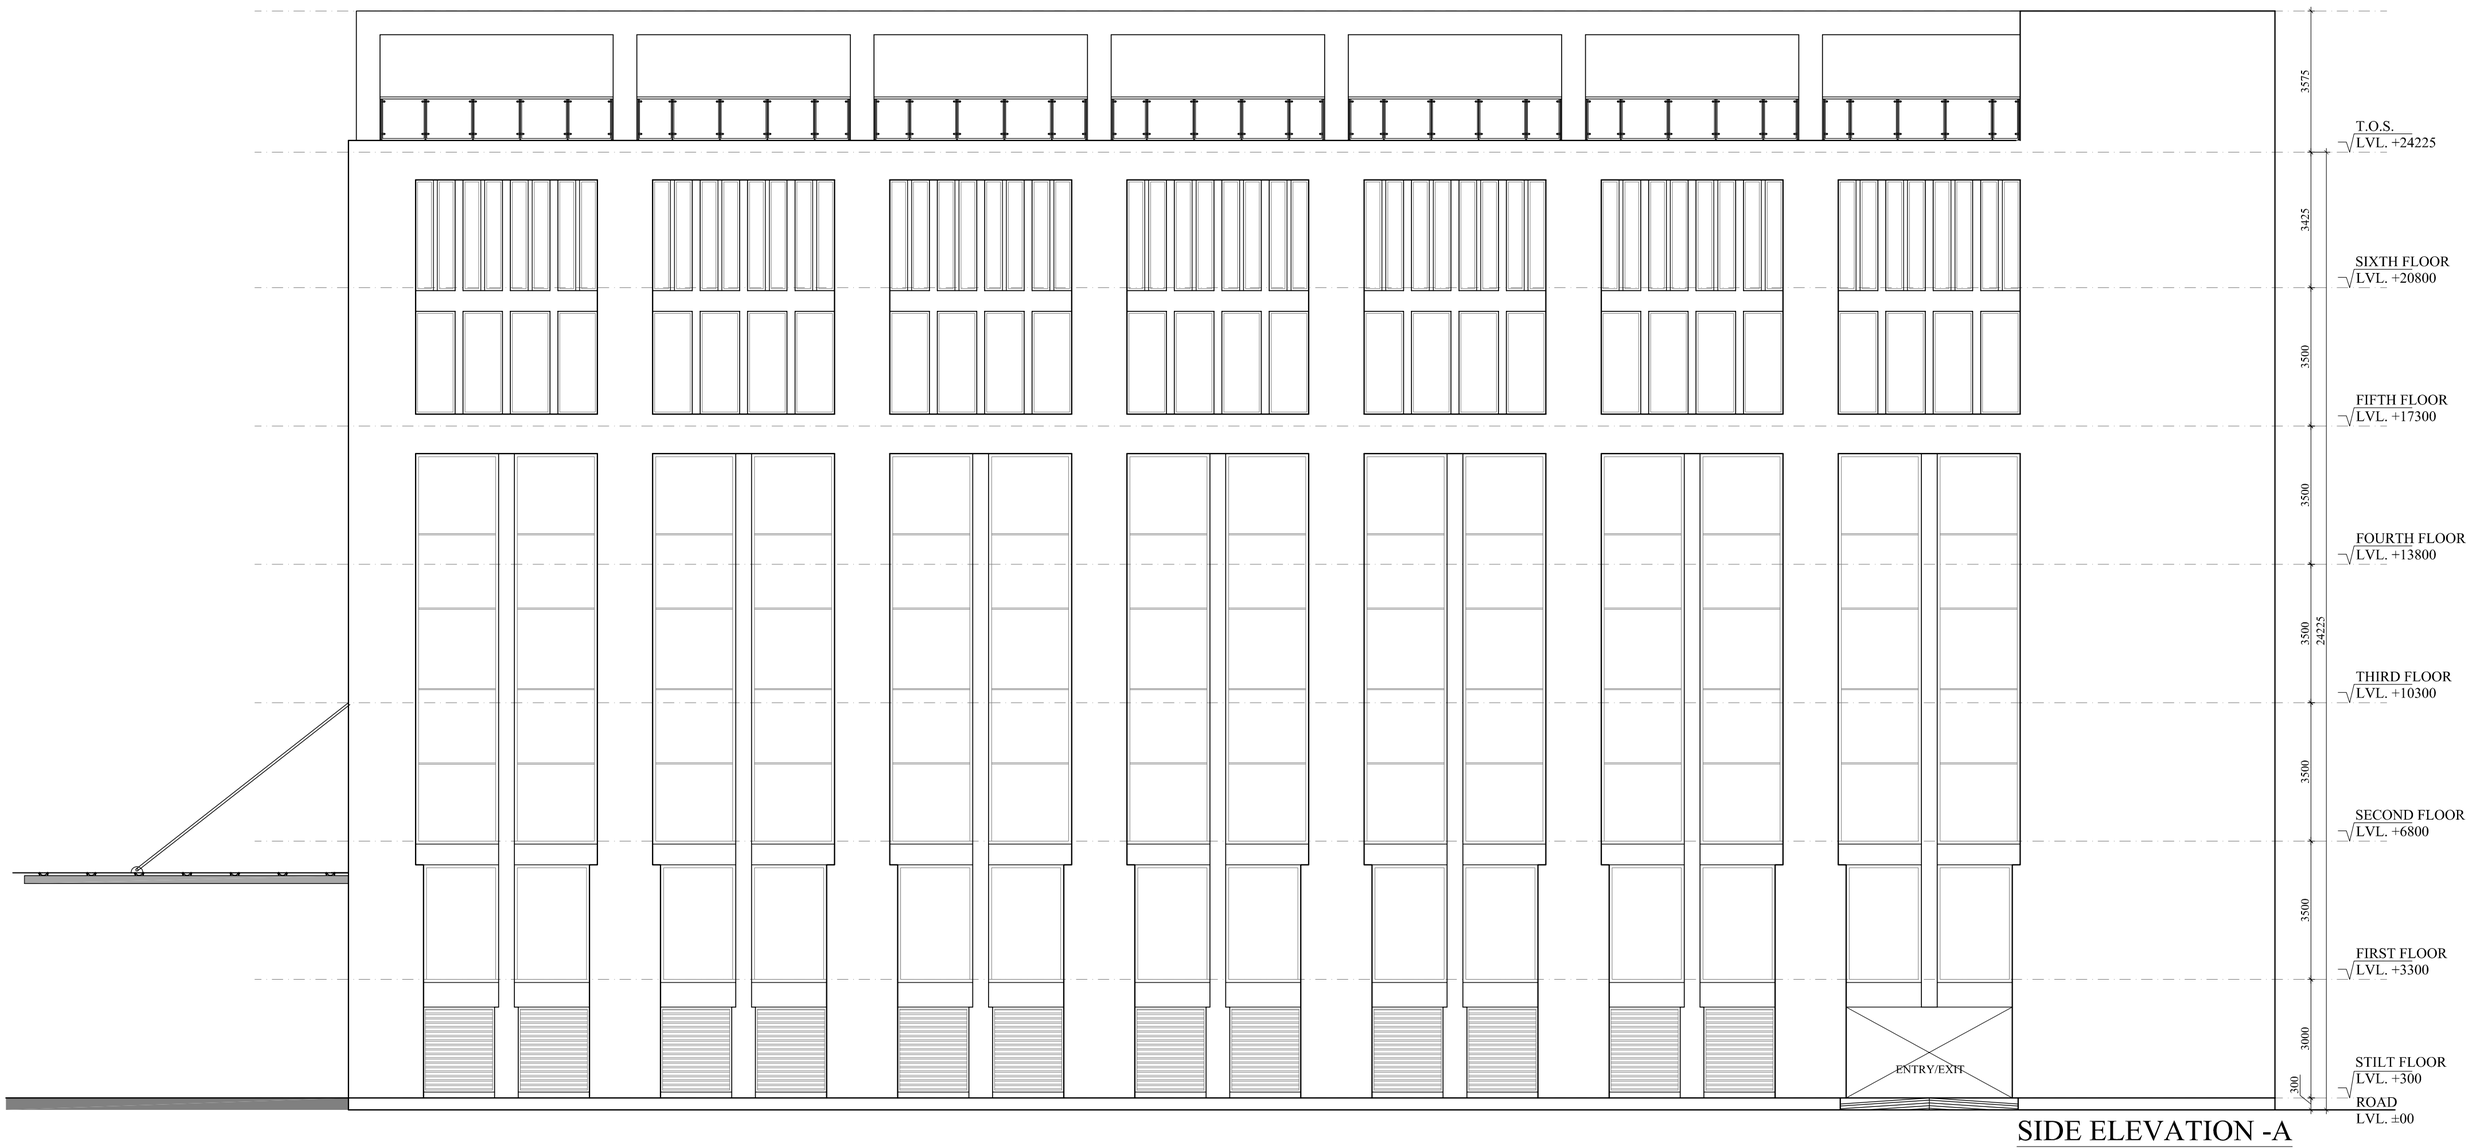

SIDE ELEVATION -A

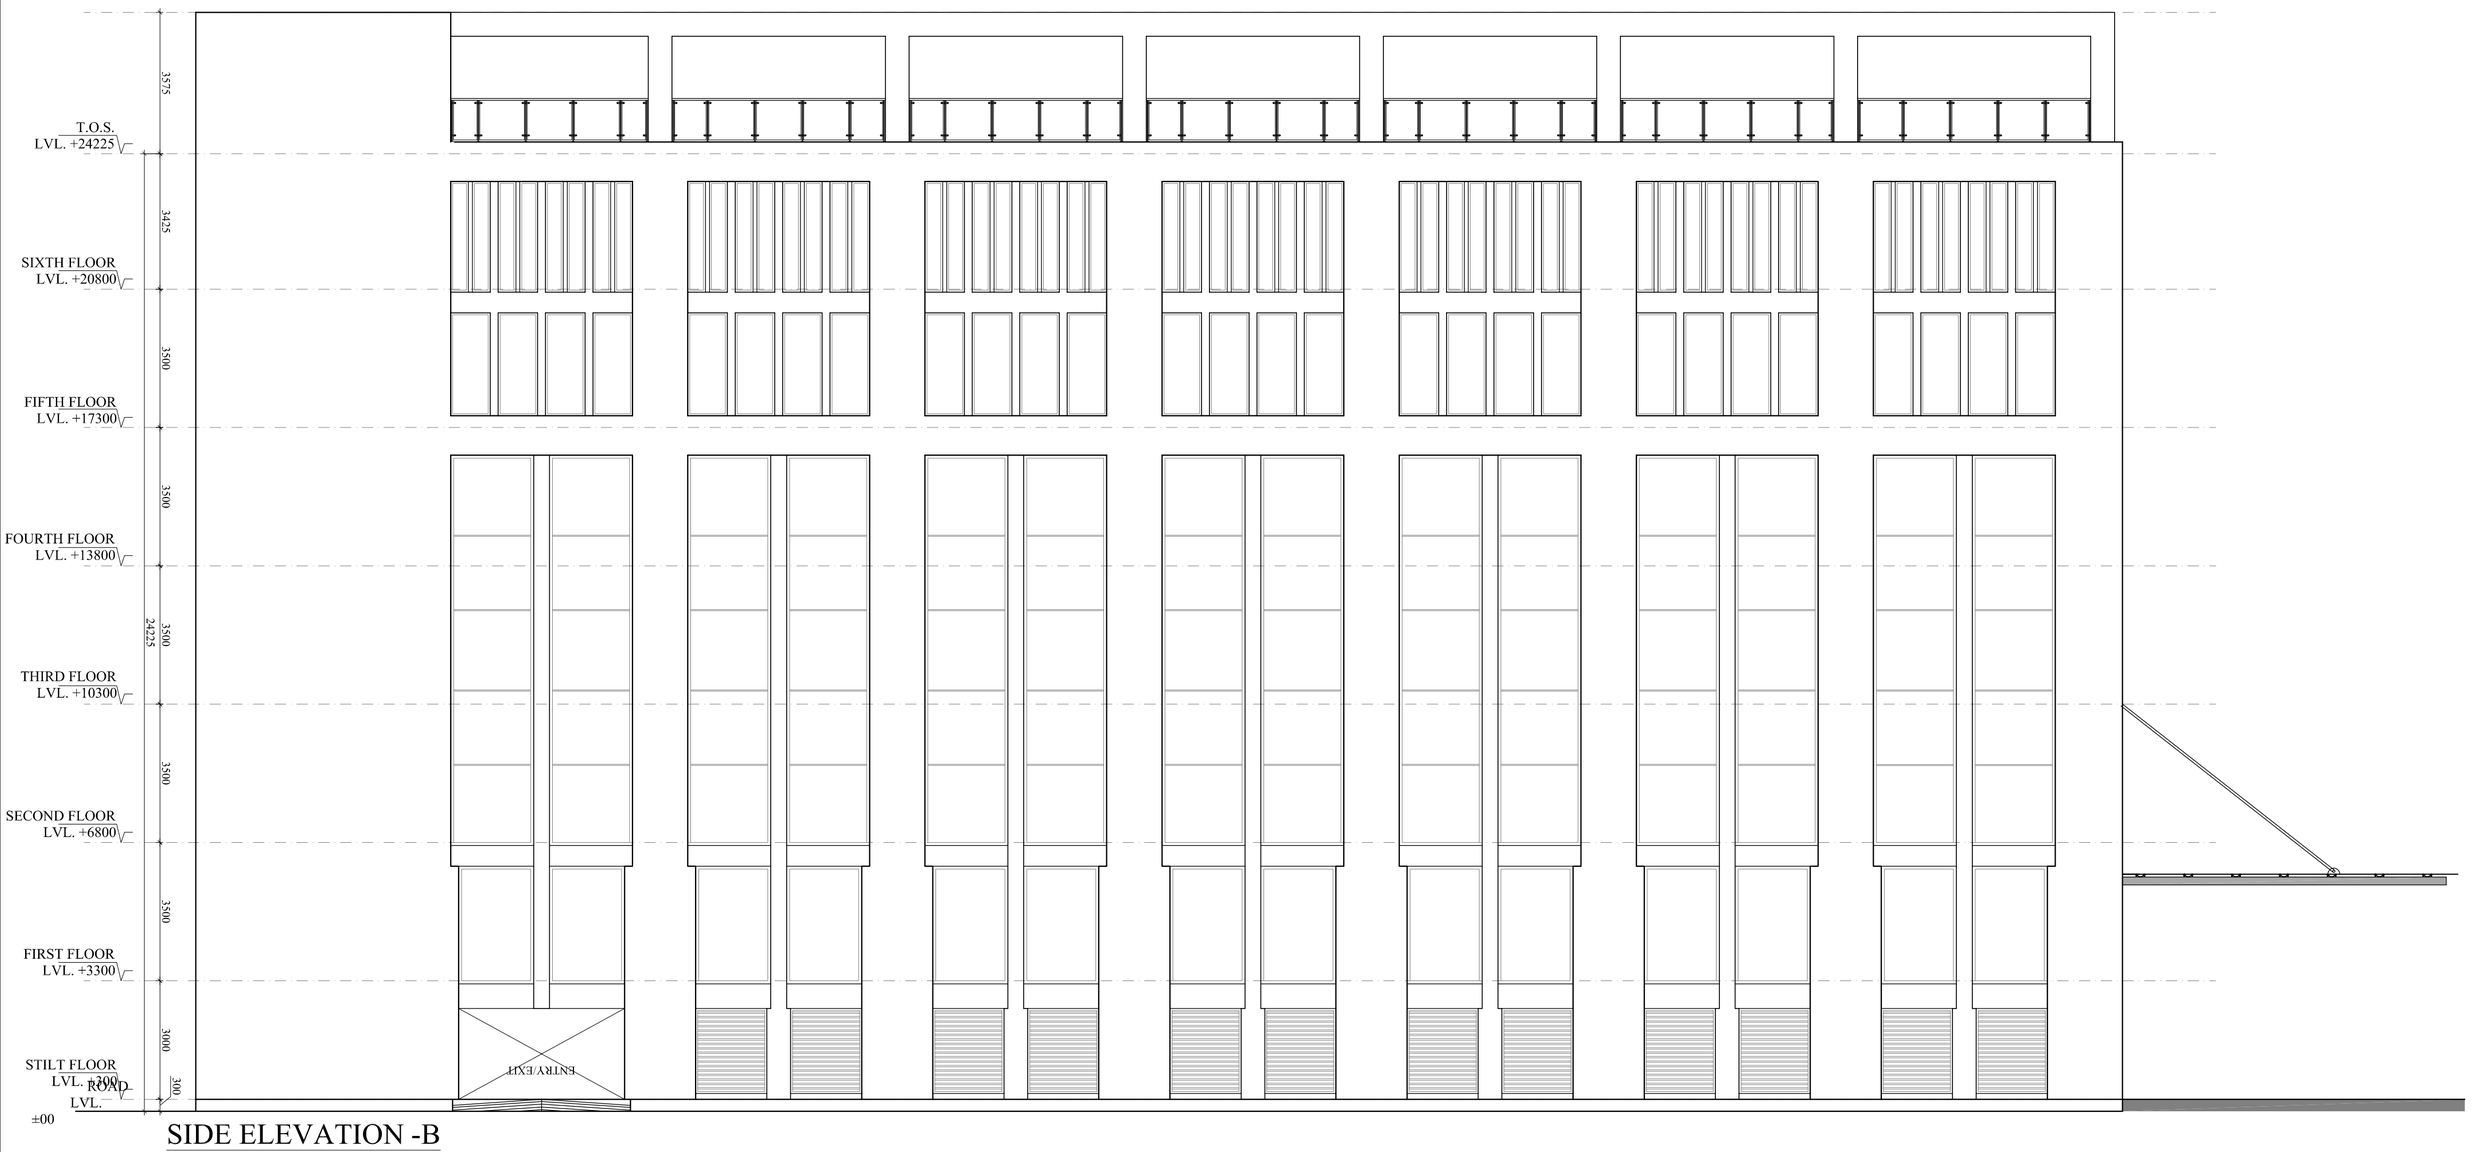

SIDE ELEVATION -B

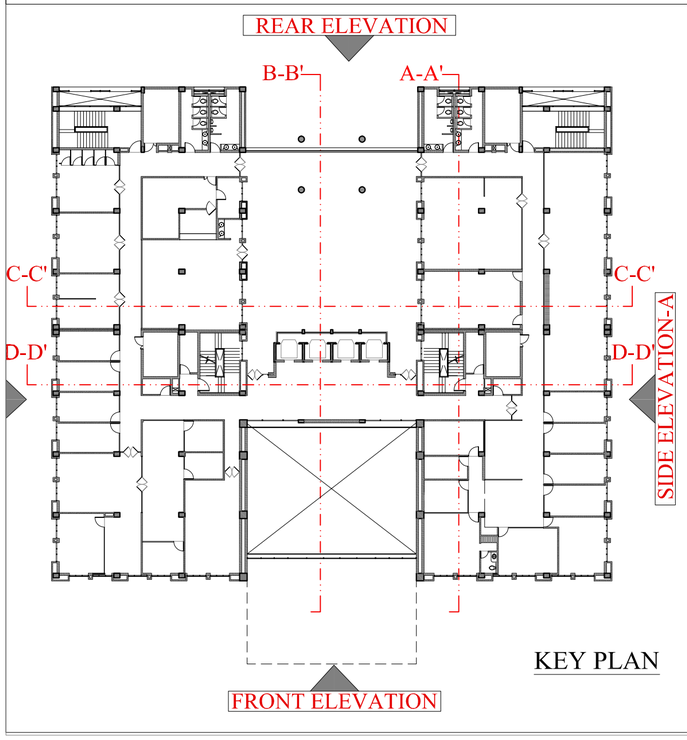

KEY PLAN

PROJECT- CONSTRUCTION OF MCMV OFFICE BUILDING AT GOA SHIPYARD, GOA		DRAWING TITLE- SIDE ELEVATIONS		
DRAWING PURPOSE- WORKING DRAWING				
DWG. NO.- 538/GSL/TD/AR/302				
JOB NO. - 538	DWG. REF. NO.- ----------	DATE- ----------	SHEET SIZE- A1	SHEET NO- ----------
SCALE- 1:110	REVISION- ----------	DATE OF ISSUE- ----------	DRAWN BY- RAJEEV	CHECKED BY- MATINDER

OWNER-

EXECUTING AGENCY-

NBCC (INDIA) LIMITED
(Formerly National Buildings Construction Limited)
(A Government of India Enterprise)
A Navratna CPSE
NBCC Bhawan, Lodhi Road
New Delhi - 110 003, India
Telephone No : 011 - 24367314 - 17, 24367573
Fax : 011 - 24366995

MECHANICAL CONSULTANT- DESIGN CENTER CONSULTING ENGINEERS, NEW DELHI

ELECTRICAL CONSULTANT- DESIGN CENTER CONSULTING ENGINEERS, NEW DELHI

ARCHITECTS-

DESIGN ASSOCIATES INC
A - 163, Sector - 136,
Noida - Greater Noida Expressway,
Noida - 201301, Phone no: 0120-2428600/30
e-mail: matinder.sharma@designassociates.in

PLUMBING CONSULTANT- DESIGN CENTER CONSULTING ENGINEERS, NEW DELHI

STRUCTURE CONSULTANT-


LKT ENGINEERING CONSULTANTS LTD.
10/49, Subhash Nagar,New Delhi-110027
Phone:+011-45565818,Tel/Fax:+011-25126129
info@lktengineering.com
http://-www.lktengineering.com

NOTES:
1. ALL DIMENSIONS ARE IN MM.
2. ALL DIMENSIONS ARE TO BE READ AND NOT MEASURED.
3. ALL LEVELS ARE IN METERS.
4. GRID DIMENSIONS AND PLOT LINES ARE TO BE STRICTLY ADHERED TO.
5. ALL LEVELS INCLUDING FLOOR LEVELS, CILL & LINTEL LEVELS, LANDING LEVELS, PARAPET HEIGHT/ LEVELS, LEVELS OF HORIZONTAL PROJECTION & BONDS INCLUDING ANY SURFACE FEATURES INDICATED IN THE DRAWINGS ARE TO BE STRICTLY ADHERED TO.


MARK	DATE	DESCRIPTION
R2	--------	REVISION
R1	--------	REVISION
GFC	--------	GOOD FOR CONSTRUCTION
AC	--------	ADVANCE COPY

THIS DRAWING IS THE PROPERTY OF THE DESIGN ASSOCIATES INC. AND SHALL NOT BE COPIED OR USED IN ANY MANNER WITHOUT PRIOR PERMISSION.


KEY PLAN

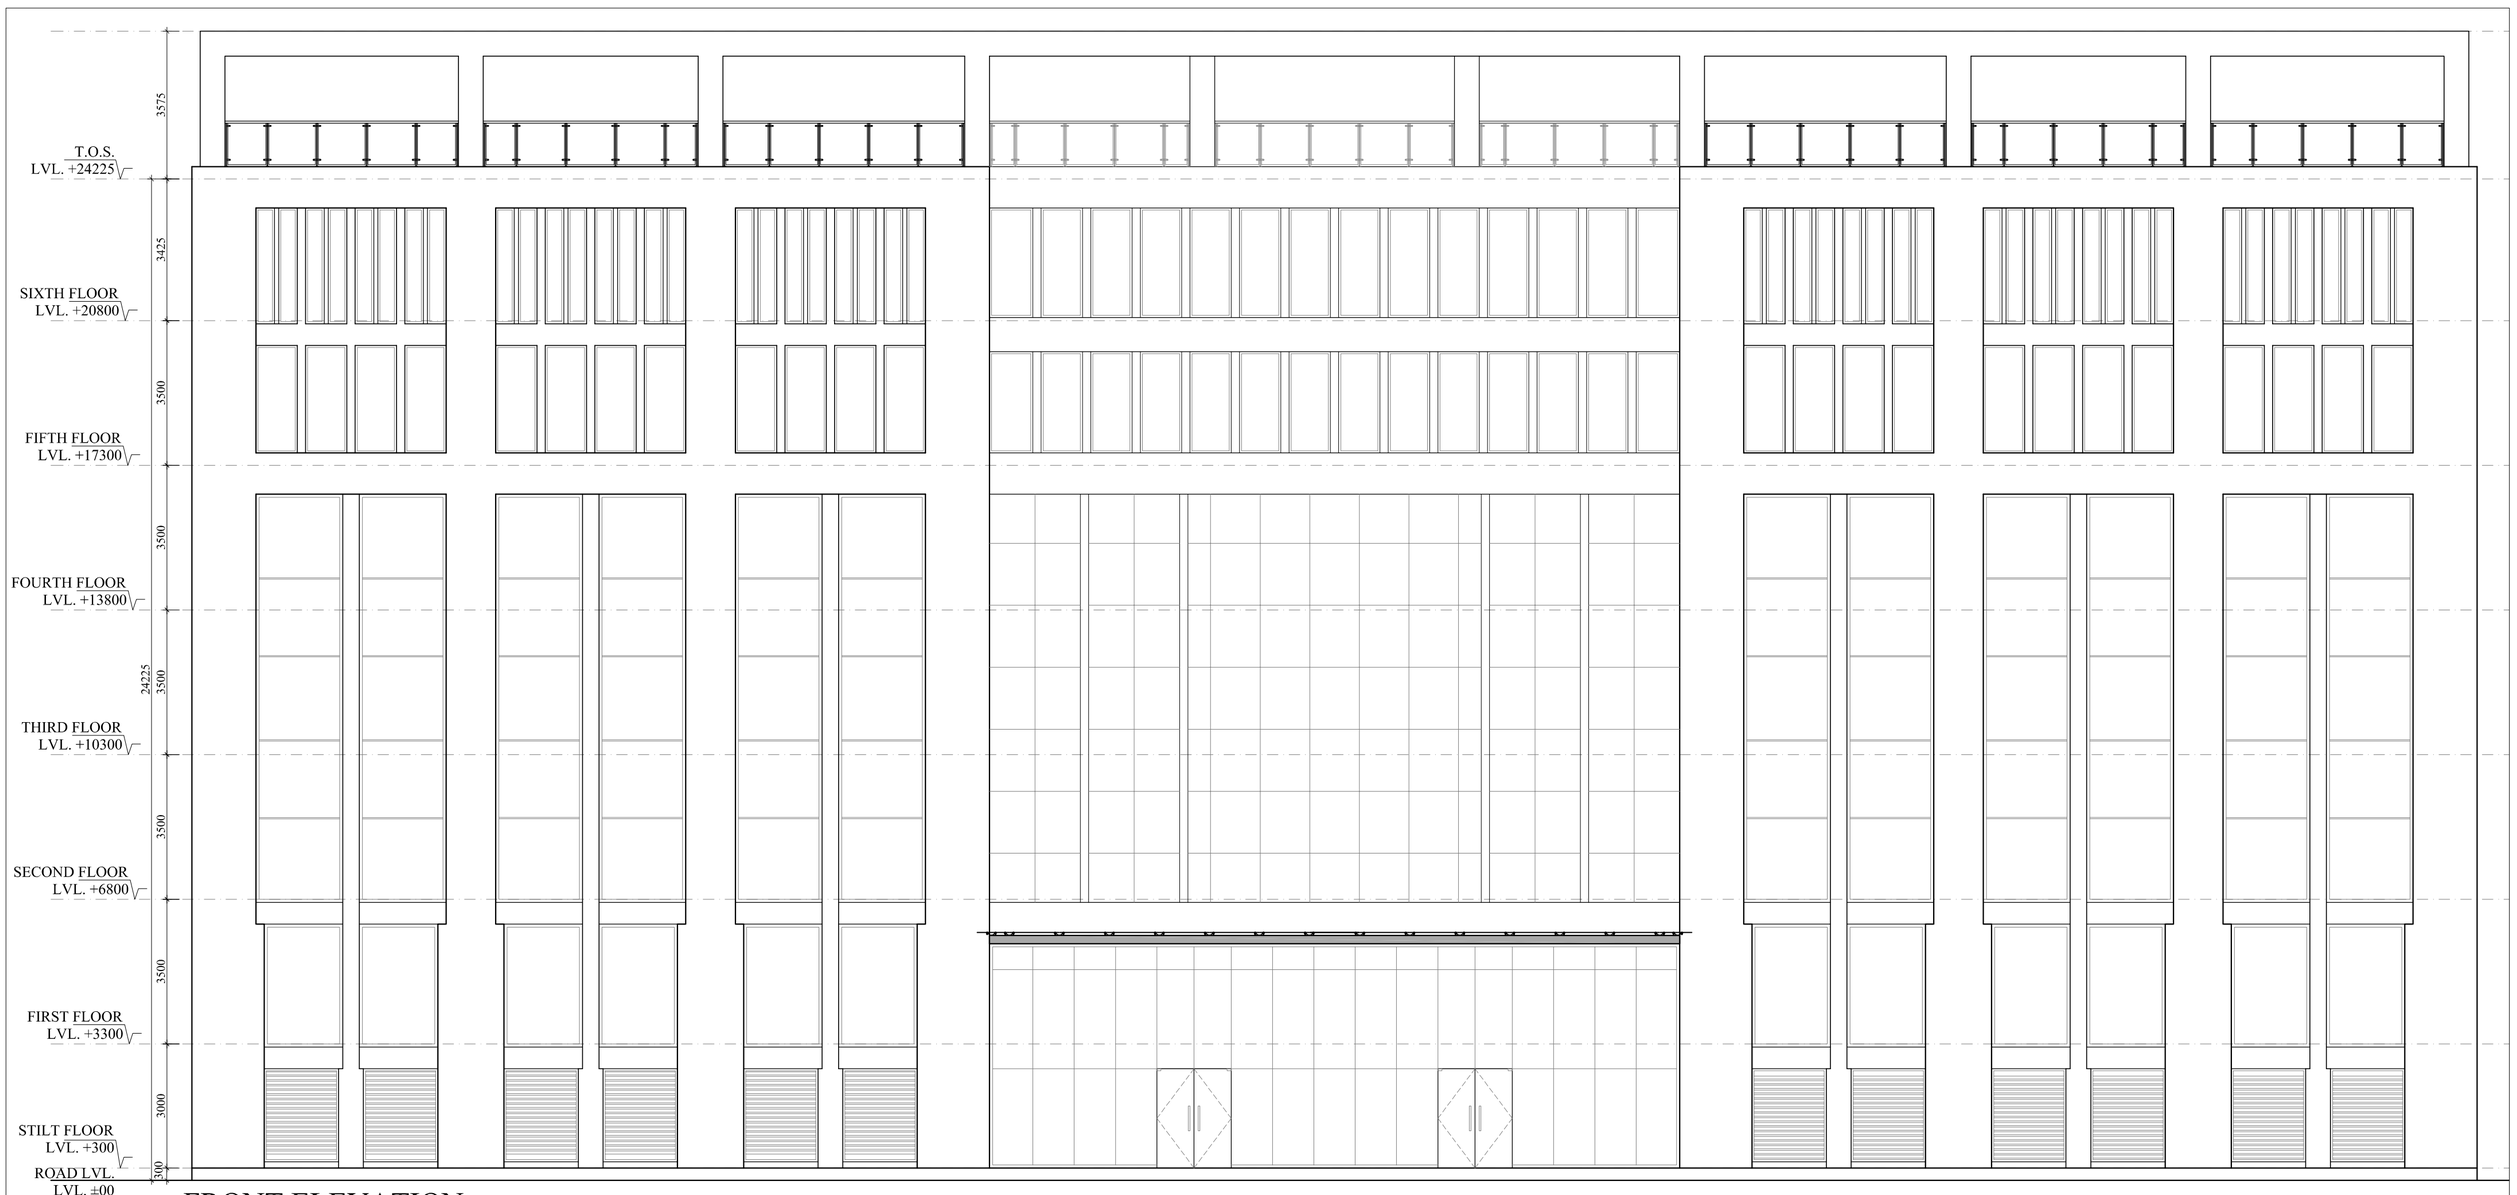

FRONT ELEVATION

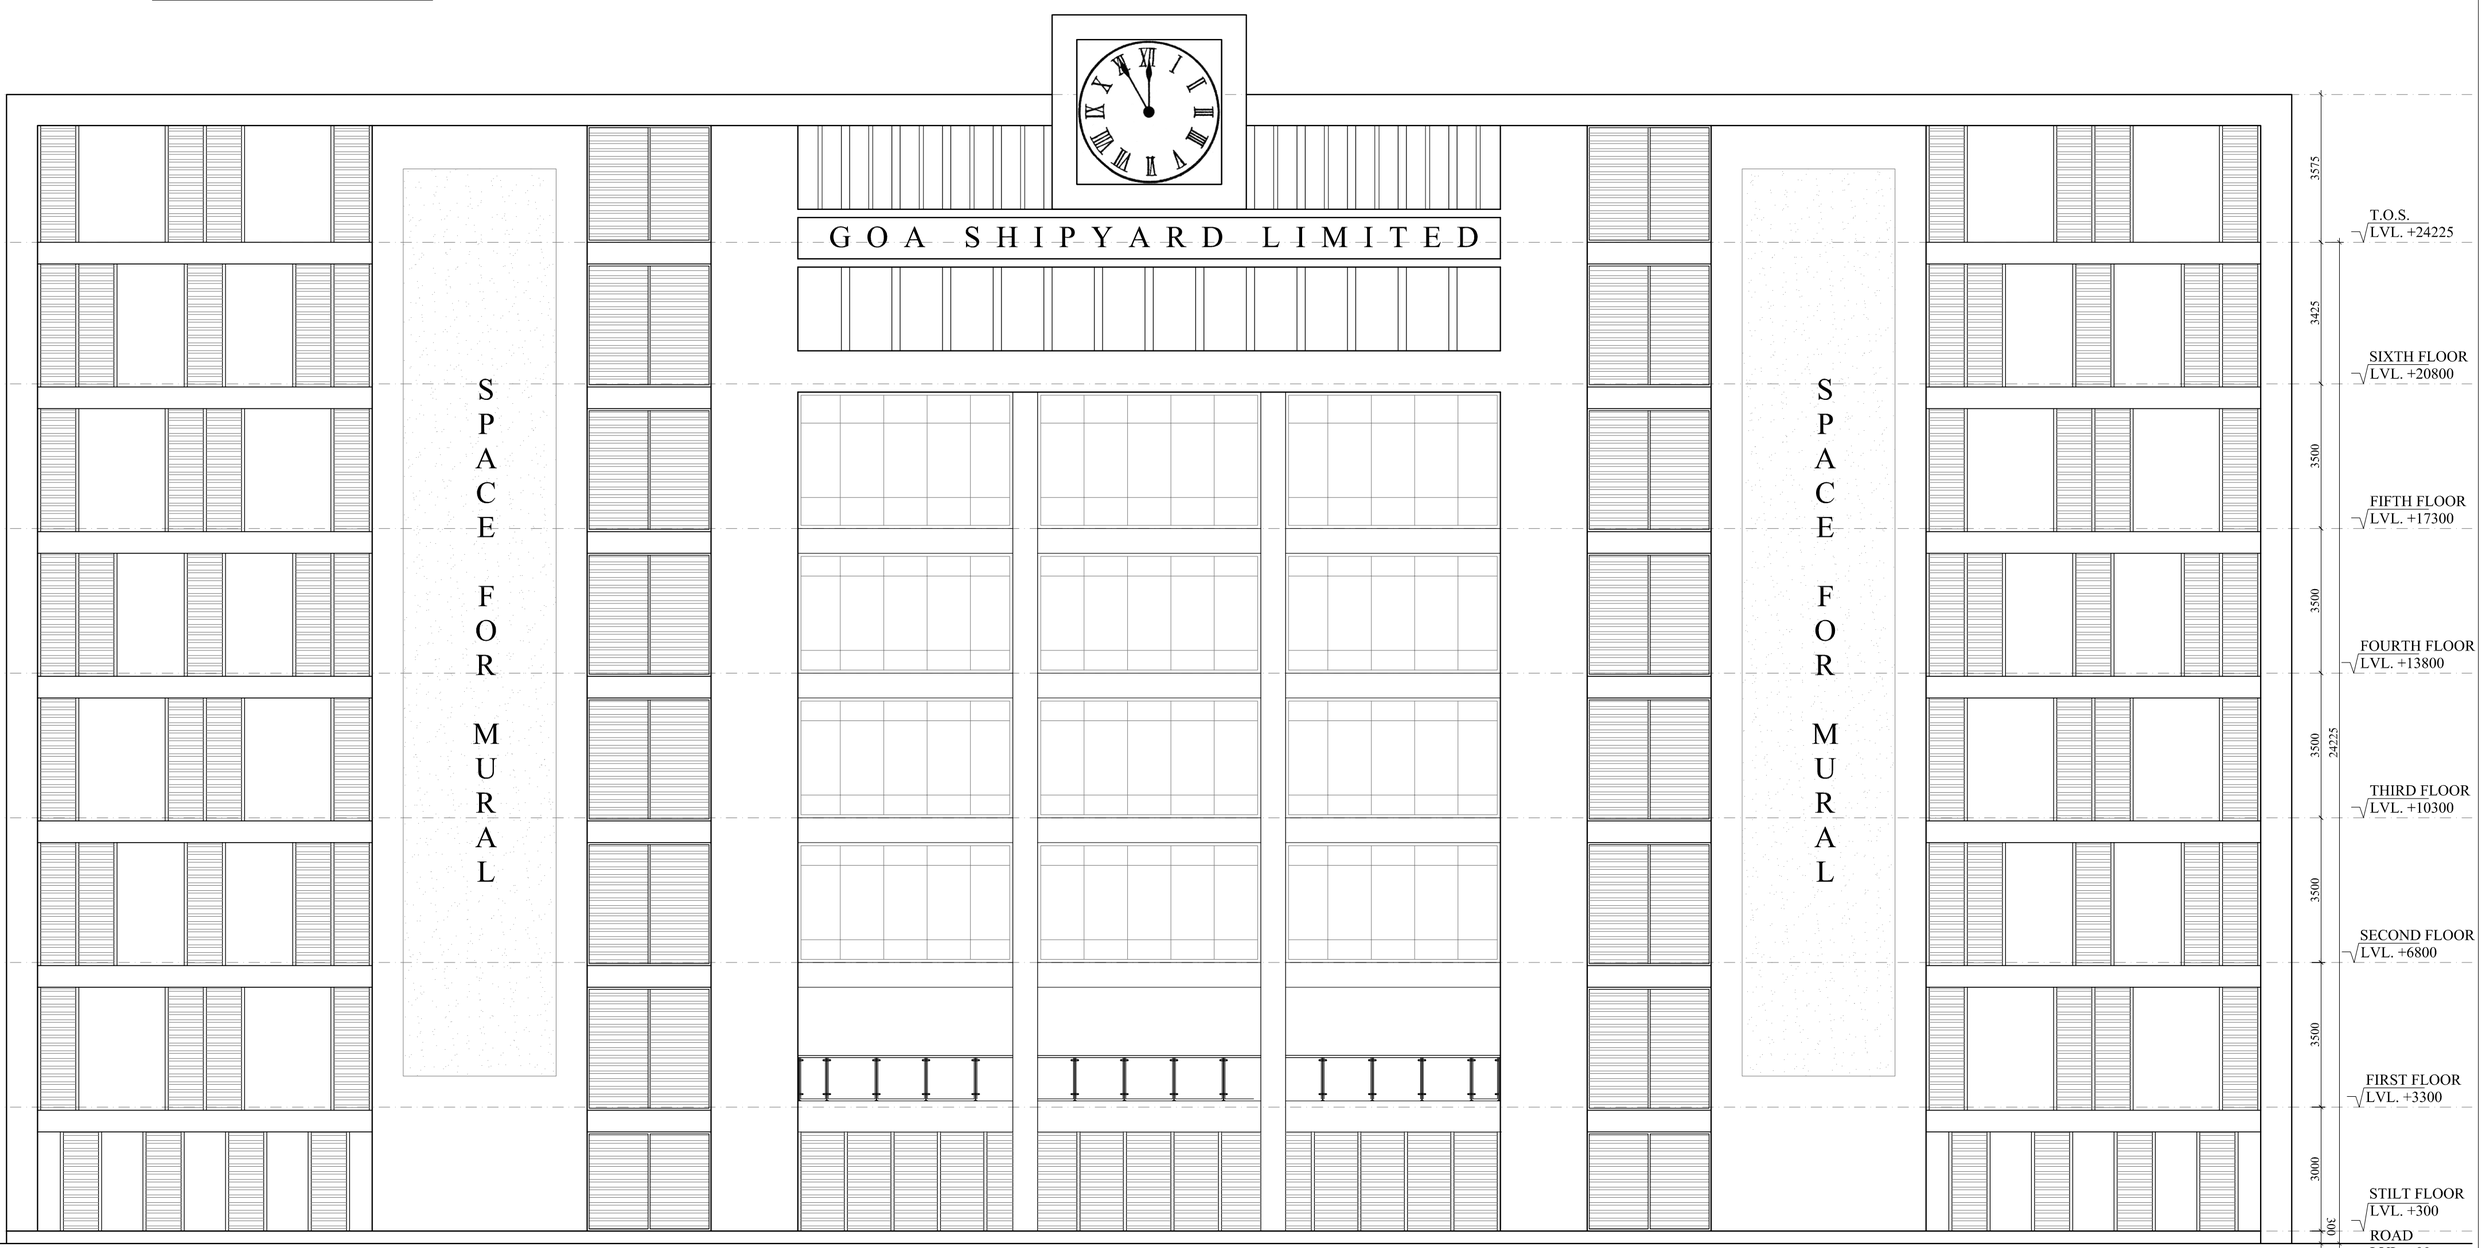

REAR ELEVATION

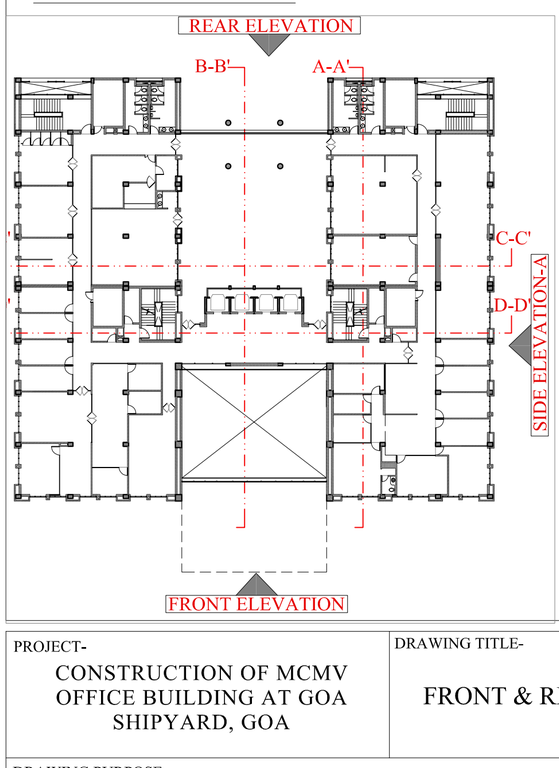

PROJECT-
CONSTRUCTION OF MCMV OFFICE BUILDING AT GOA SHIPYARD, GOA

DRAWING TITLE-
FRONT & REAR ELEVATION

OWNER-

ARCHITECTS-
DESIGN ASSOCIATES INC
A - 163, Sector - 136,
Noida - Greater Noida Expressway,
Noida - 201301, Phone no: 0120-2428600/30
e-mail: matinder.sharma@designassociates.in

NOTES:
1. ALL DIMENSIONS ARE IN MM.
2. ALL DIMENSIONS ARE TO BE READ AND NOT MEASURED.
3. ALL LEVELS ARE IN METERS.
4. GRID DIMENSIONS AND PLOT LINES ARE TO BE STRICTLY ADHERED TO.
5. ALL LEVELS INCLUDING FLOOR LEVELS, CILL & LINTEL LEVELS, LANDING LEVELS, PARAPET HEIGHT/ LEVELS, LEVELS OF HORIZONTAL PROJECTION & BONDS INCLUDING ANY SURFACE FEATURES INDICATED IN THE DRAWINGS ARE TO BE STRICTLY ADHERED TO.

THIS DRAWING IS THE PROPERTY OF THE DESIGN ASSOCIATES INC. AND SHALL NOT BE COPIED OR USED IN ANY MANNER WITHOUT PRIOR PERMISSION.

DRAWING PURPOSE-
WORKING DRAWING

EXECUTING AGENCY-
NBCC (INDIA) LIMITED
(Formerly National Buildings Construction Limited)
(A Government of India Enterprise)
A Navratna CPSE
NBCC Bhawan, Lodhi Road
New Delhi - 110 003, India
Telephone No : 011 - 24367314 - 17, 24367573
Fax : 011 - 24366995

DWG. NO.-
538/GSL/TD/AR/301

JOB NO. -	DWG. REF. NO.-	DATE-	SHEET SIZE-	SHEET NO-
538	----------	----------	A1	----------
SCALE-	REVISION-	DATE OF ISSUE-	DRAWN BY-	CHECKED BY-
1:110	----------	----------	RAJEEV	MATINDER

MECHANICAL CONSULTANT-
DESIGN CENTER CONSULTING ENGINEERS, NEW DELHI


PLUMBING CONSULTANT-
DESIGN CENTER CONSULTING ENGINEERS, NEW DELHI

ELECTRICAL CONSULTANT-
DESIGN CENTER CONSULTING ENGINEERS, NEW DELHI

STRUCTURE CONSULTANT-
LKT ENGINEERING CONSULTANTS LTD.
10/49, Subhash Nagar,New Delhi-110027
Phone : 011-45565818,Tel/Fax:011-25126129
info@lktengineering.com
http://www.lktengineering.com

MARK	DATE	DESCRIPTION
R2	--------	REVISION
R1	--------	REVISION
GFC	--------	GOOD FOR CONSTRUCTION
AC	--------	ADVANCE COPY

KEY PLAN

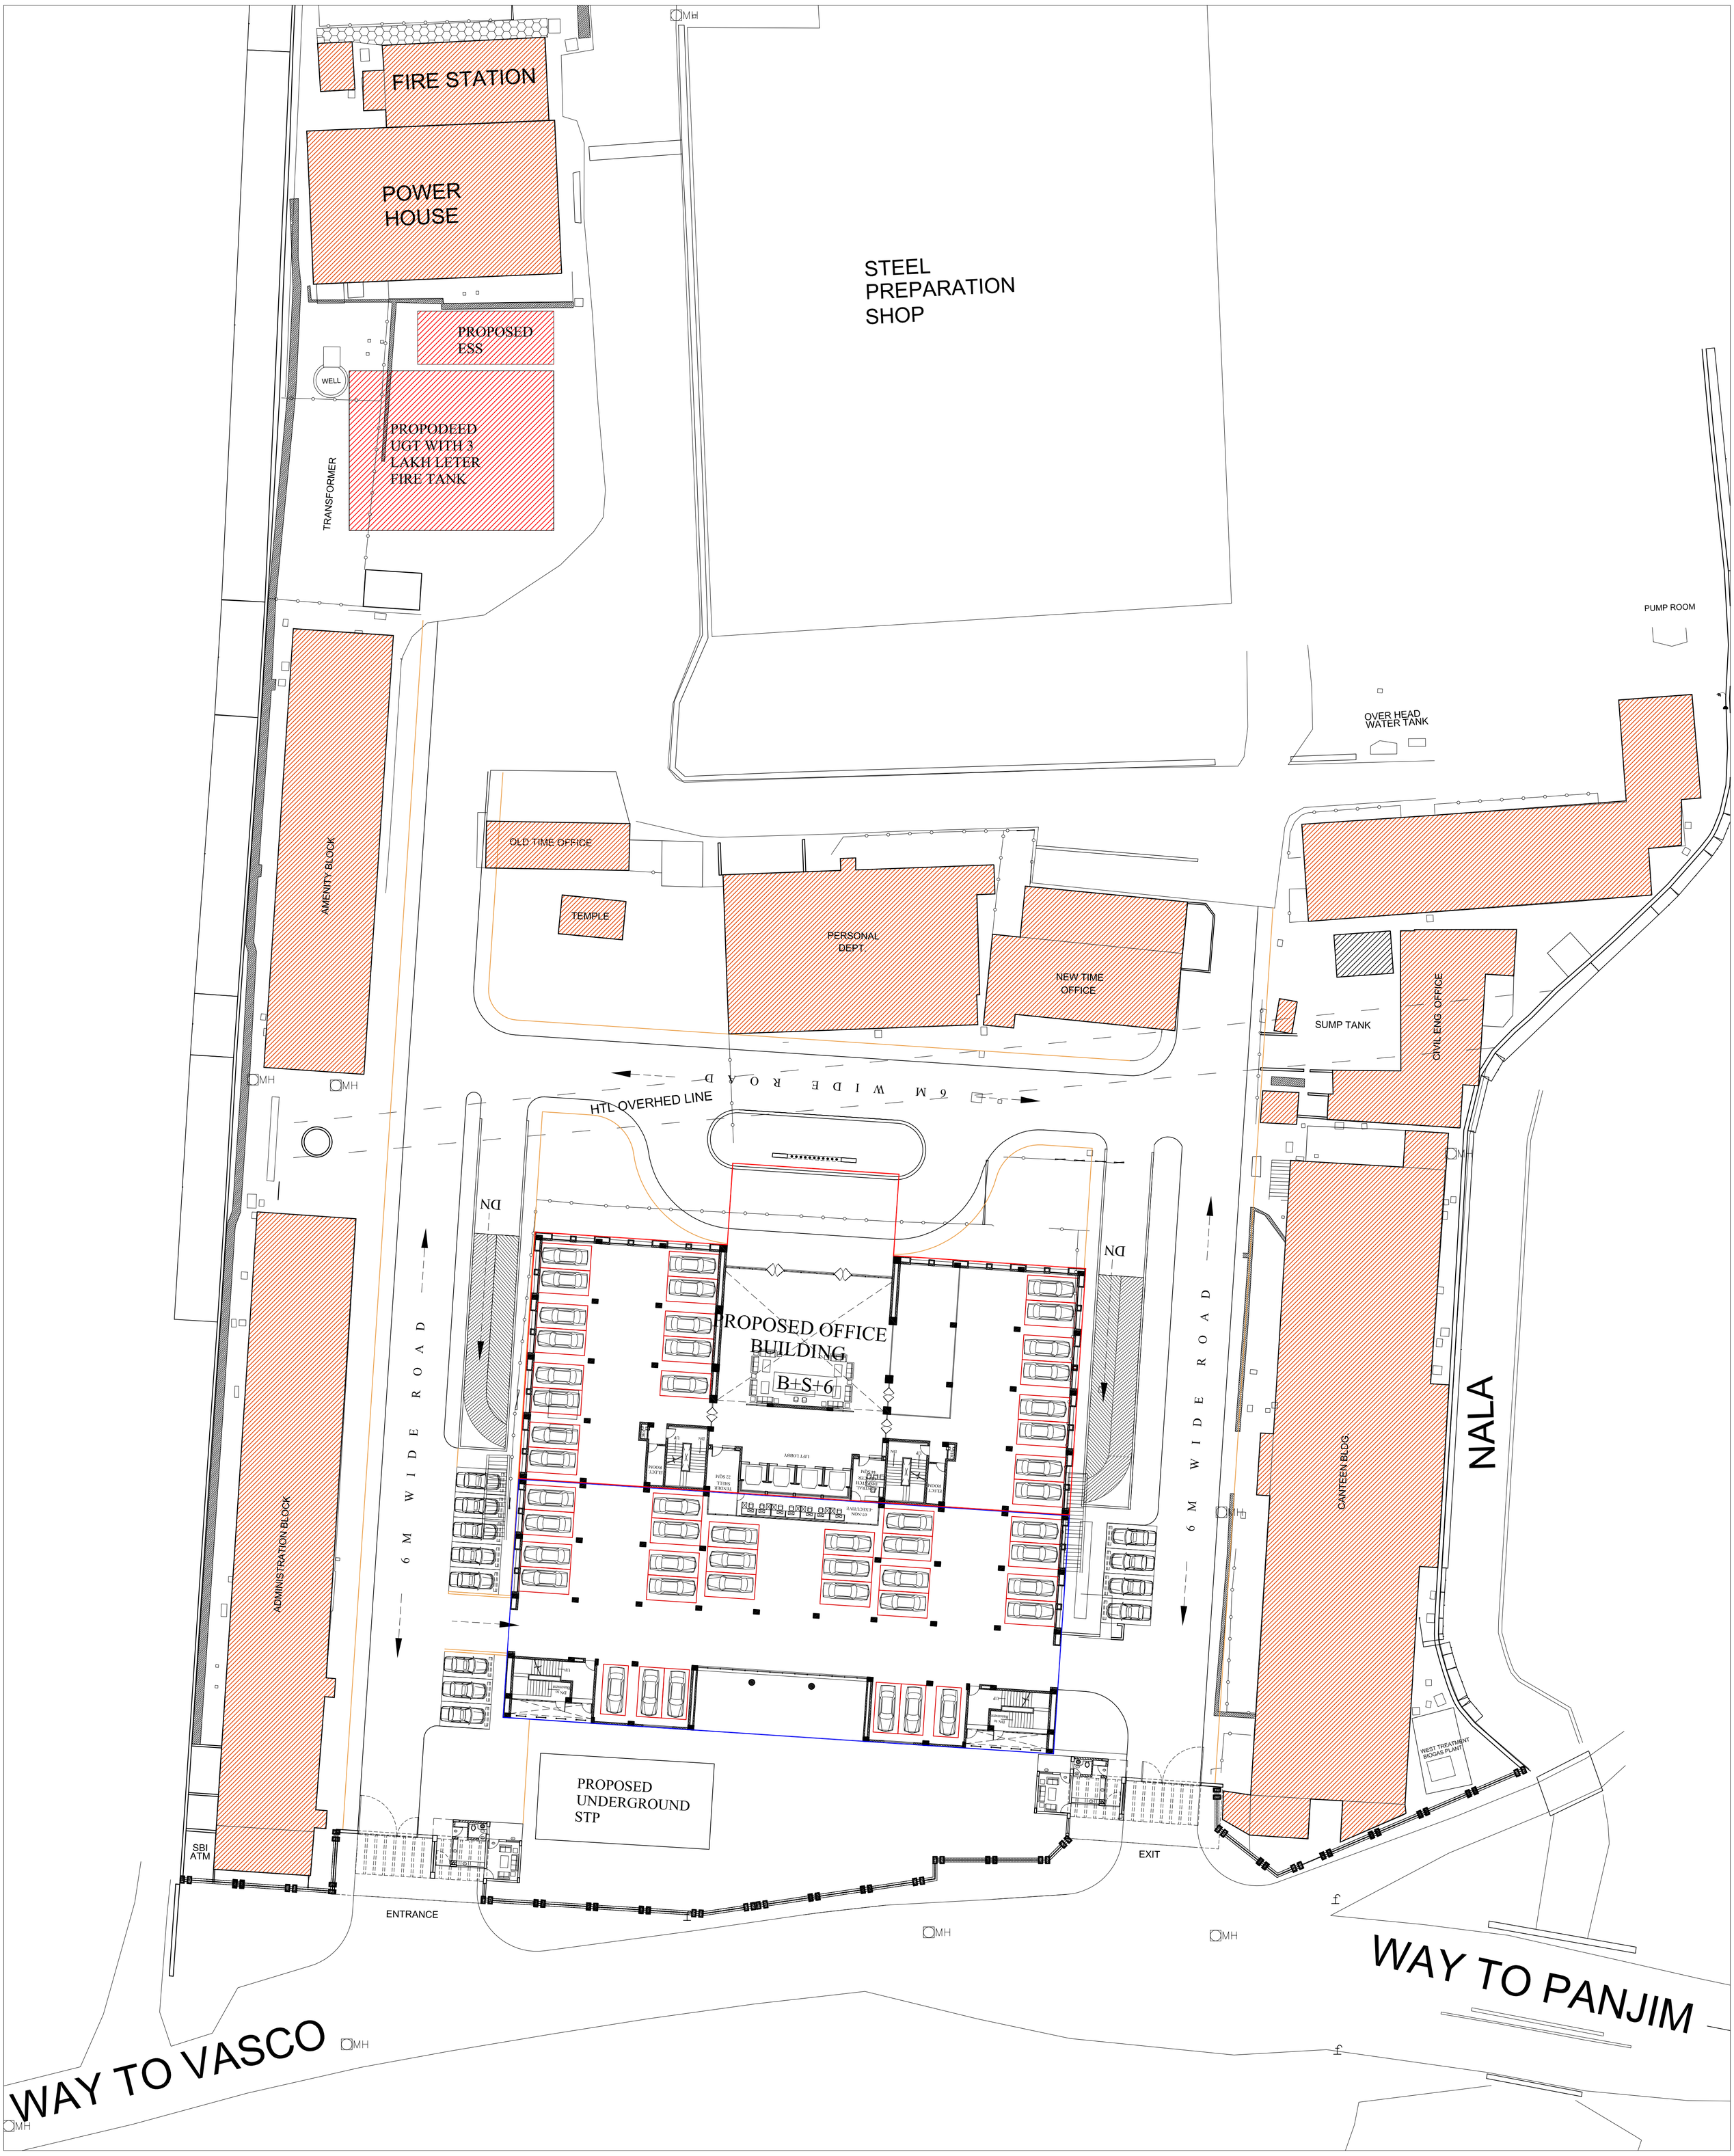

PROJECT-

CONSTRUCTION OF MCMV OFFICE BUILDING AT GOA SHIPYARD, GOA

DRAWING TITLE-

SITE PLAN

OWNER-

GOA SHIPYARD LIMITED
(A Govt. of India Undertaking)

VASCO DA GAMA, GOA, 403802
contactus@goashipyard.com
TEL.No: - (0832) 251252-56, 2512359
FAX No: -(0091-832) 2514232, 2512148

ARCHITECTS-

DESIGN ASSOCIATES INC.

A - 163, Sector - 136,
Noida - Greater Noida Expressway,
Noida - 201301, Phone no: 0120-2428600/30
e-mail: matinder.sharma@designassociates.in

NOTES:
1. ALL DIMENSIONS ARE IN MM.
2. ALL DIMENSIONS ARE TO BE READ AND NOT MEASURED.
3. ALL LEVELS ARE IN METERS.
4. GRID DIMENSIONS AND PLOT LINES ARE TO BE STRICTLY ADHERED TO.
5. ALL LEVELS INCLUDING FLOOR LEVELS, CILL & LINTEL LEVELS, LANDING LEVELS, PARAPET HEIGHT/ LEVELS, LEVELS OF HORIZONTAL PROJECTION & BONDS INCLUDING ANY SURFACE FEATURES INDICATED IN THE DRAWINGS ARE TO BE STRICTLY ADHERED TO.

THIS DRAWING IS THE PROPERTY OF THE DESIGN ASSOCIATES INC. AND SHALL NOT BE COPIED OR USED IN ANY MANNER WITHOUT PRIOR PERMISSION.

DRAWING PURPOSE-

TENDER DRAWING

EXECUTING AGENCY-

NBCC (INDIA) LIMITED
(Formerly National Buildings Construction Limited)
(A Government of India Enterprise)

NBCC Bhawan, Lodhi Road
New Delhi - 110 003, India
Telephone No : 011 - 24367314 - 17, 24367573
Fax : 011 - 24366995

DWG. NO.-

538/GSL/TD/AR/101

NOTE:-

EXISTING STRUCTURE

PROPOSED UGT WITH 3LAKH LITER FIRE

JOB NO. -	DWG. REF. NO.-	DATE-	SHEET SIZE-	SHEET NO-
538	----------	----------	A1	----------

MECHANICAL CONSULTANT-
DESIGN CENTER CONSULTING ENGINEERS, NEW DELHI

PLUMBING CONSULTANT-
DESIGN CENTER CONSULTING ENGINEERS, NEW DELHI

SCALE-	REVISION-	DATE OF ISSUE-	DRAWN BY-	CHECKED BY-
----------	----------	21.12.16	RAJEEV	MATINDER

ELECTRICAL CONSULTANT-
DESIGN CENTER CONSULTING ENGINEERS, NEW DELHI


STRUCTURE CONSULTANT-


LKT Engineering Consultants Ltd.
10/49, Subhash Nagar,
New Delhi-110027
Phone :+011-45565818
Tel/Fax:+011-25126129
info@lktengineering.com
http://www.lktengineering.com


MARK	DATE	DESCRIPTION
R2	--------	REVISION
R1	--------	REVISION
GFC	--------	GOOD FOR CONSTRUCTION
AC	--------	ADVANCE COPY


LEGEND:–


SYM.	DESCRIPTION
A	AMMETER
V	VOLT METER
PF	POWER FACTOR METER
HZ	FREQUENCY METER
MFM	MULTI FUNCTION METER(AVF & KWH)
KW	KILOWATT METER
ASS	AMMETER SELECTOR SWITCH
VSS	VOLTMETER SELECTOR SWITCH
CT	CURRENT TRANSFORMER
	INDICATING LAMP
PT	POTENTIAL TRANSFORMER
	GROUNDING
	MINIATURE CIRCUIT BREAKER
	MOULDED CASE CIRCUIT BREAKER
	AIR CIRCUIT BREAKER
	VACCUM CIRCUIT BREAKER
CF	CONTROL FUSE
TVM	TRIVECTOR METER
	OVER LOAD RELAY
	ISOLATOR
	CONTACTOR
	CHANGEOVER
	CAPACITOR BANK
	DG SET
	TRANSFORMER
UV	UNDER VOLTAGE RELAY
OV	OVER VOLTAGE RELAY
OT	OIL TEMPERATURE RELAY
WT	WINDING TEMPERATURE RELAY
85	BUCHOLZ RELAY
86	MASTER TRIP RELAY
32	REVERSE POWER RELAY
64	RESTRIDED EARTH FAULT RELAY
APFCR	POWER FACTOR CORRECTION RELAY

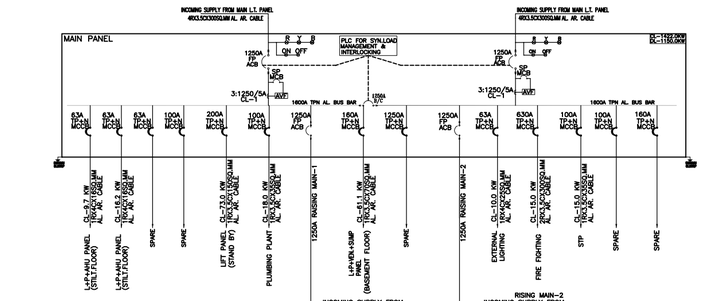


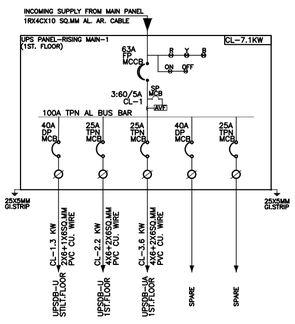


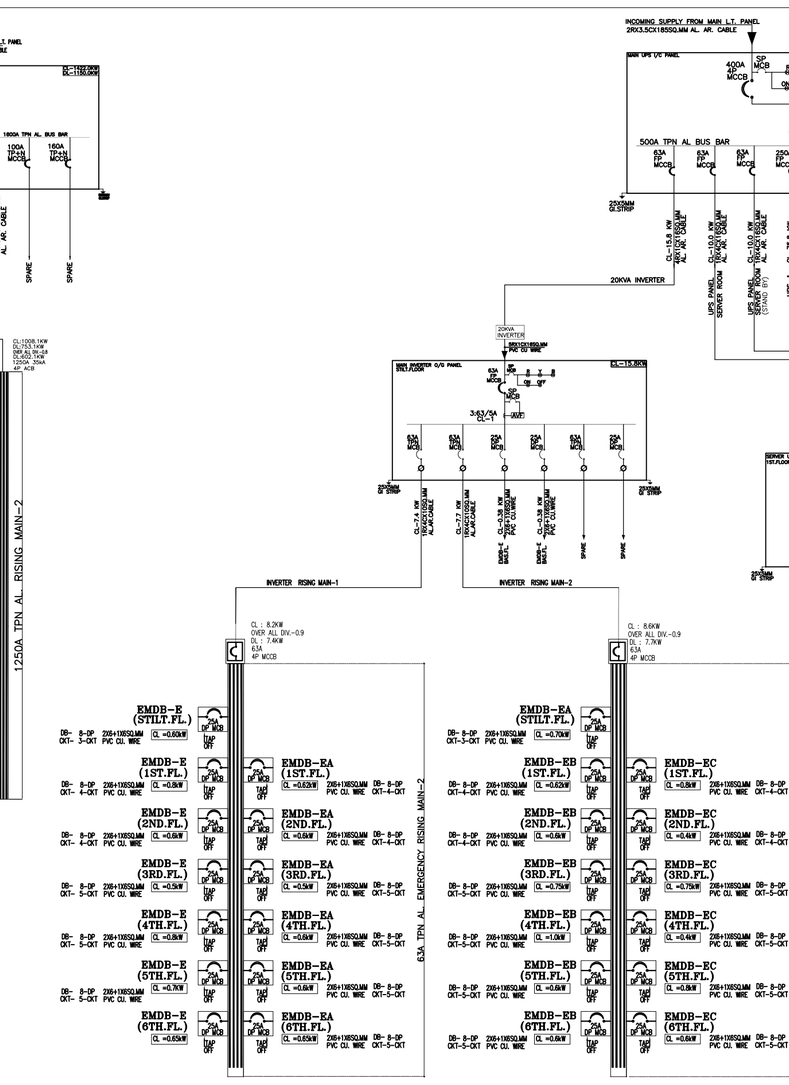


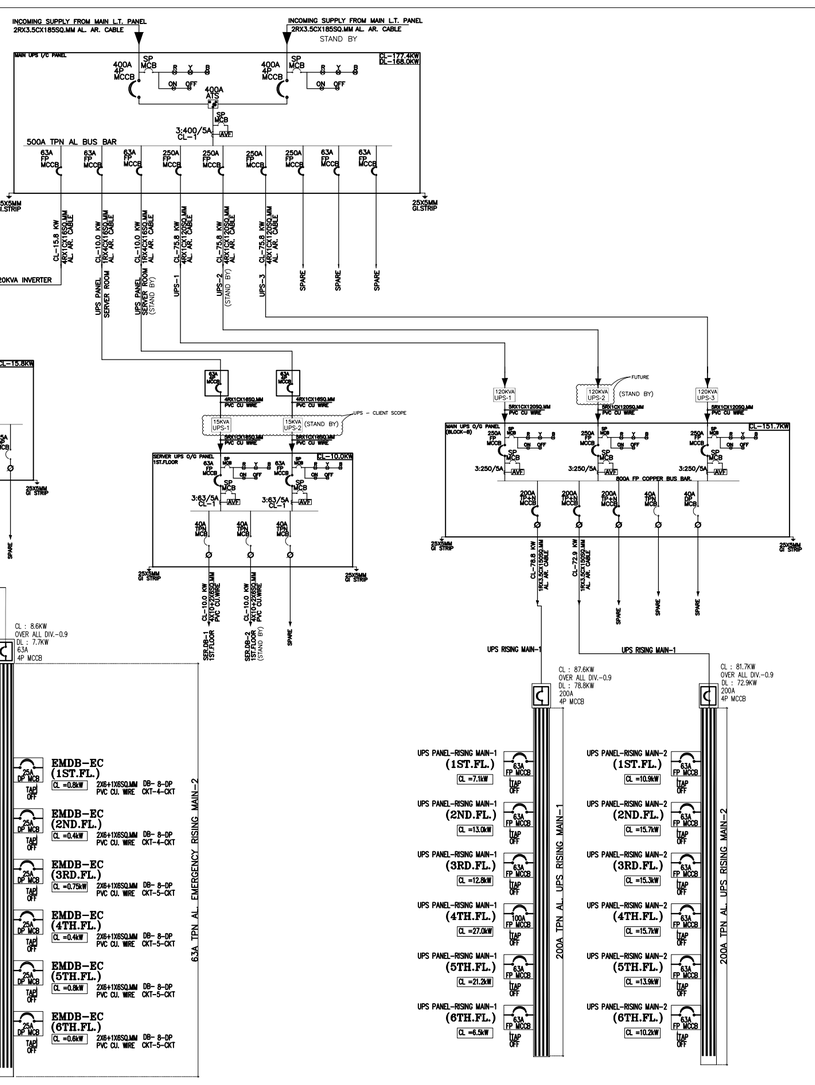


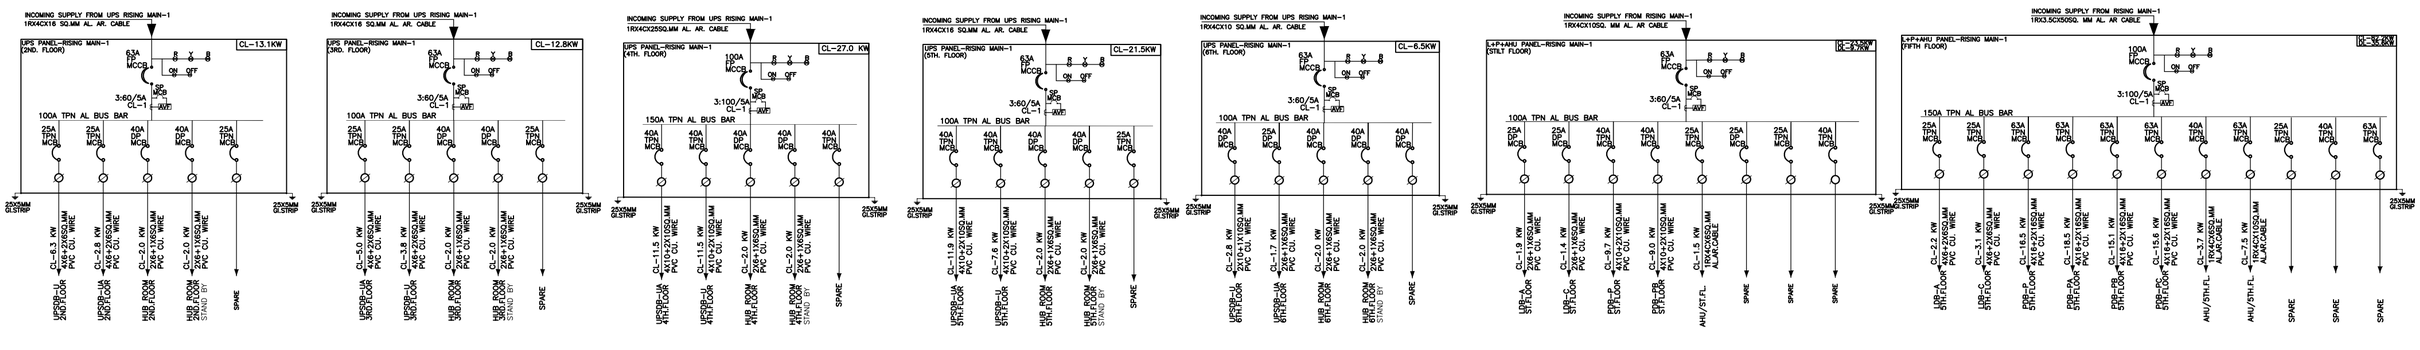


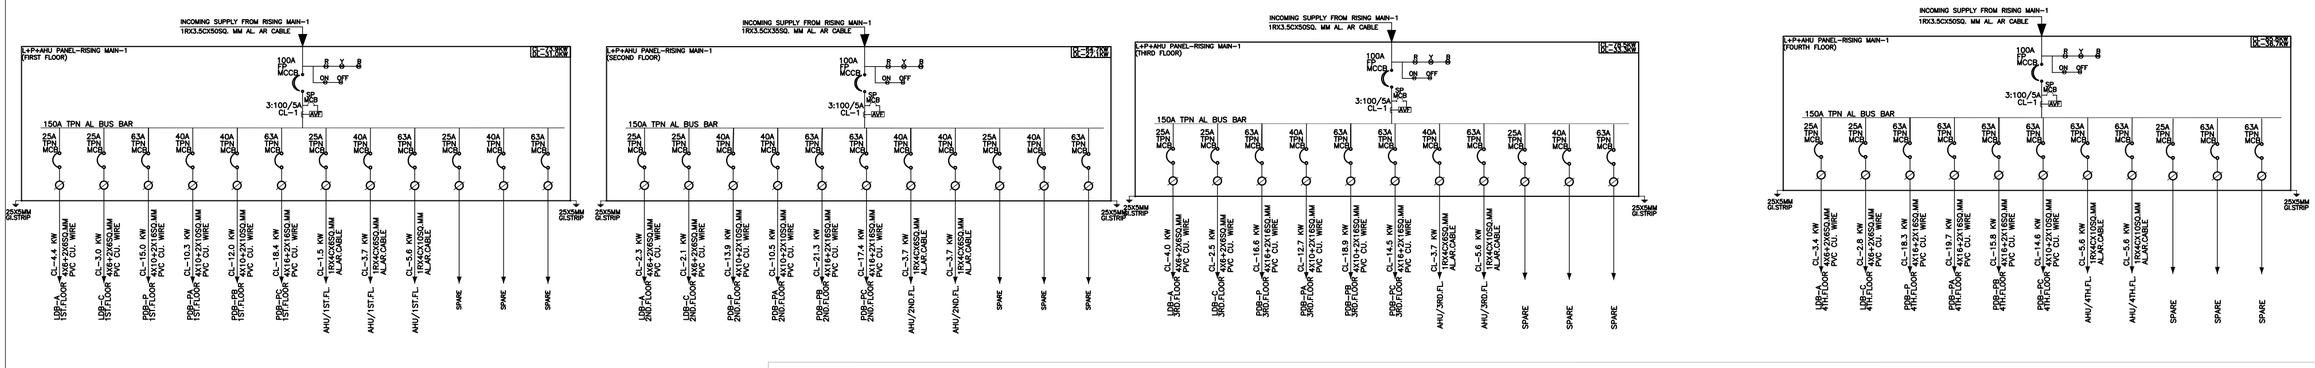

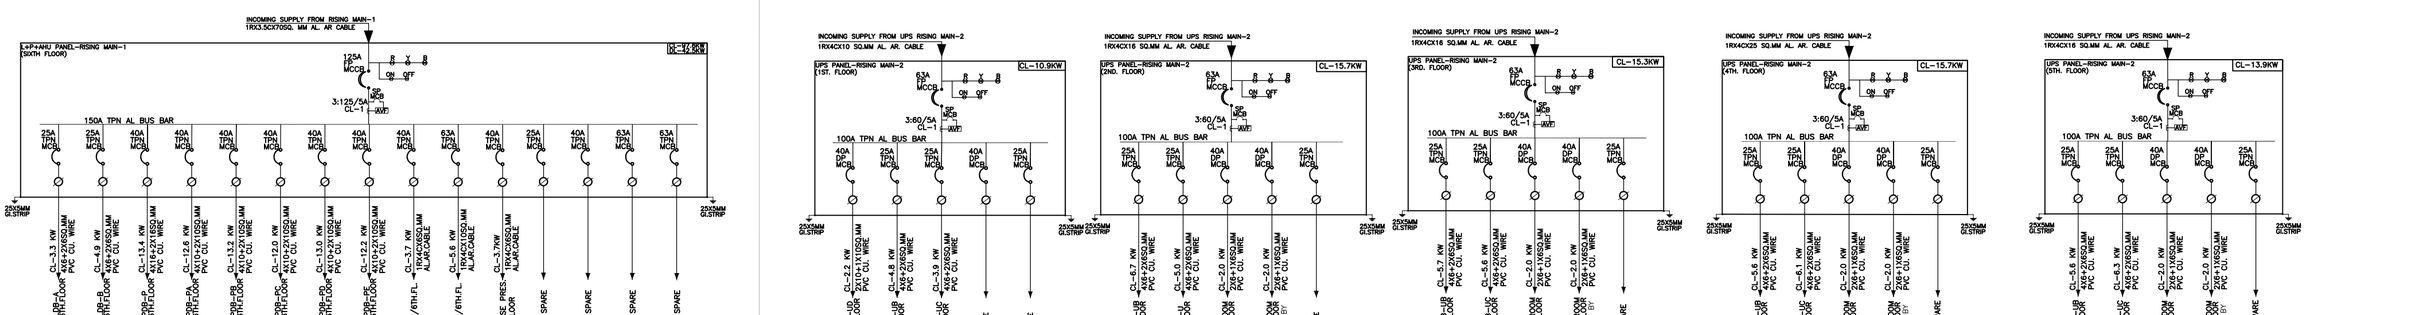

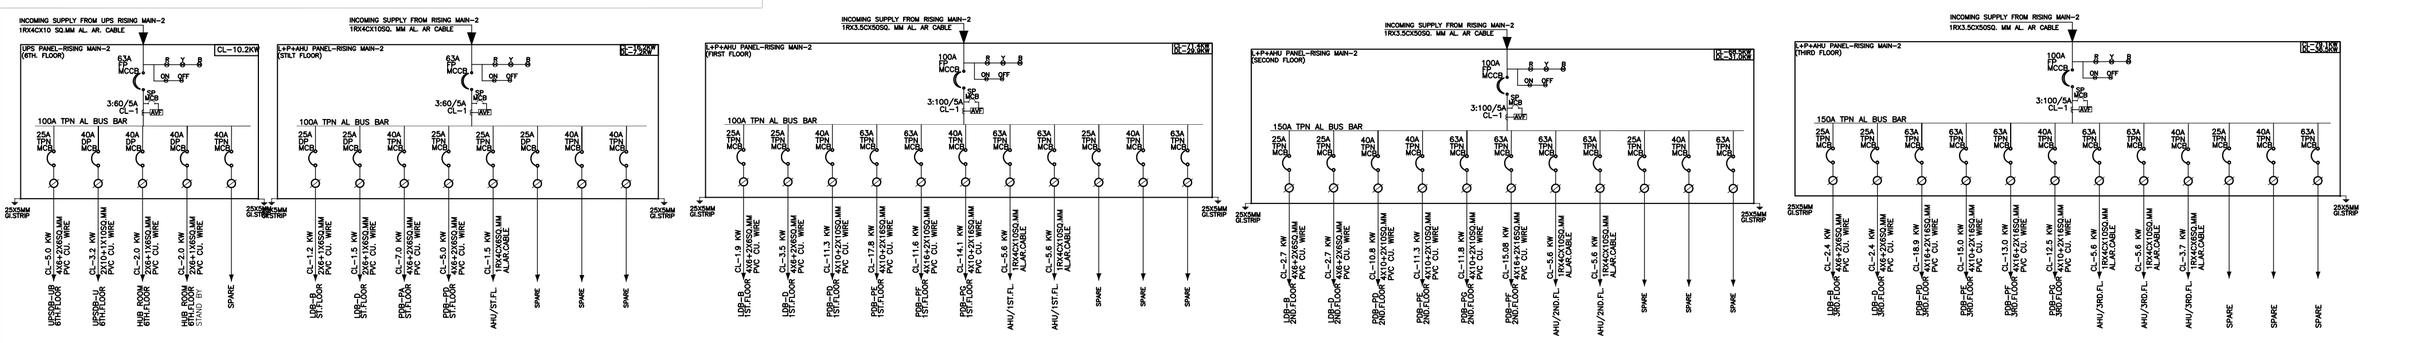

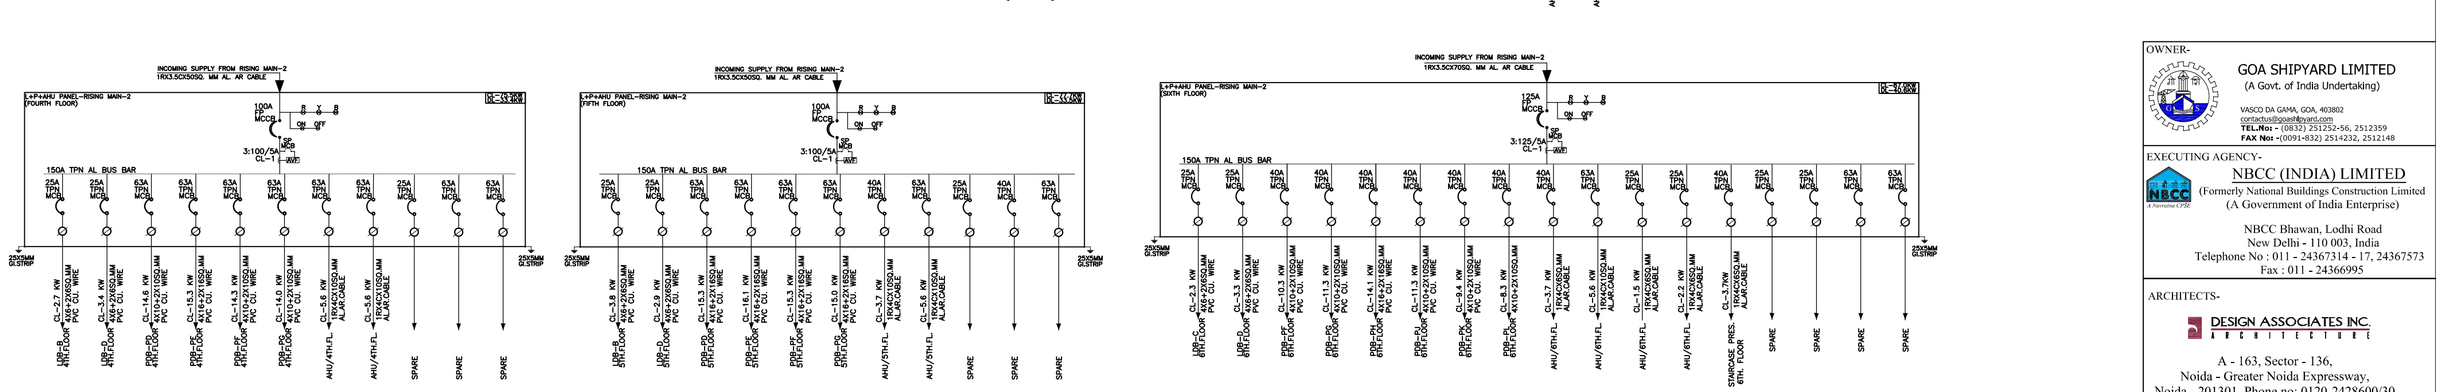

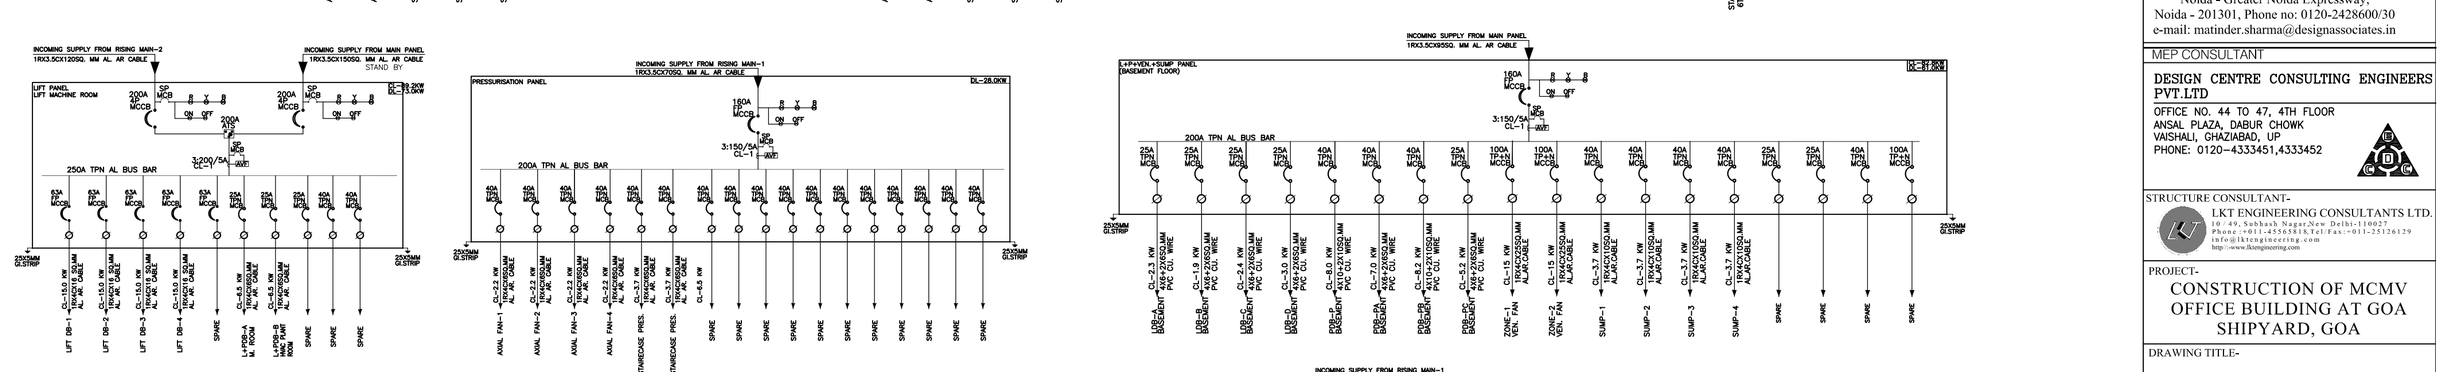

OWNER-
GOA SHIPYARD LIMITED
(A Govt. of India Undertaking)
VASCO DA GAMA, GOA, 403802
contactus@goashipyard.com
TEL.No: - (0832) 251252-56, 2512359
FAX No: -(0091+832) 2514232, 2512148

EXECUTING AGENCY-
NBCC (INDIA) LIMITED
(Formerly National Buildings Construction Limited
(A Government of India Enterprise)
NBCC Bhawan, Lodhi Road
New Delhi - 110 003, India
Telephone No : 011 - 24367314 - 17, 24367573
Fax : 011 - 24366995

ARCHITECTS-
DESIGN ASSOCIATES INC.
ARCHITECTURE
A - 163, Sector - 136,
Noida - Greater Noida Expressway,
Noida - 201301, Phone no: 0120-2428600/30
e-mail: matinder.sharma@designassociates.in

MEP CONSULTANT
DESIGN CENTRE CONSULTING ENGINEERS PVT.LTD
OFFICE NO. 44 TO 47, 4TH FLOOR
ANSAL PLAZA, DABUR CHOWK
VAISHALI, GHAZIABAD, UP
PHONE: 0120–4333451,4333452

STRUCTURE CONSULTANT-
LKT ENGINEERING CONSULTANTS LTD.
19/49, Subhash Nagar,New Delhi-110027
Phone:+011-45565818,Tel/Fax:+011-25126129
info@lktengineering.com
http:www.lktengineering.com

PROJECT-
CONSTRUCTION OF MCMV OFFICE BUILDING AT GOA SHIPYARD, GOA


DRAWING TITLE-
ELECTRICAL SINGLE LINE DIAGRAM

DRAWING PURPOSE-
TENDER DRAWING

JOB NO. -	DWG. REF. NO.-	DATE-
538	----------	----------
SCALE- NTS.	REVISION- ----------	DATE OF ISSUE- 20.12.16

DWG. NO.-
538/GSL/TD/EL/501

	SHEET SIZE-	SHEET NO-
	--------	----------
	DRAWN BY- GHANSHYAM	CHECKED BY- ARUN

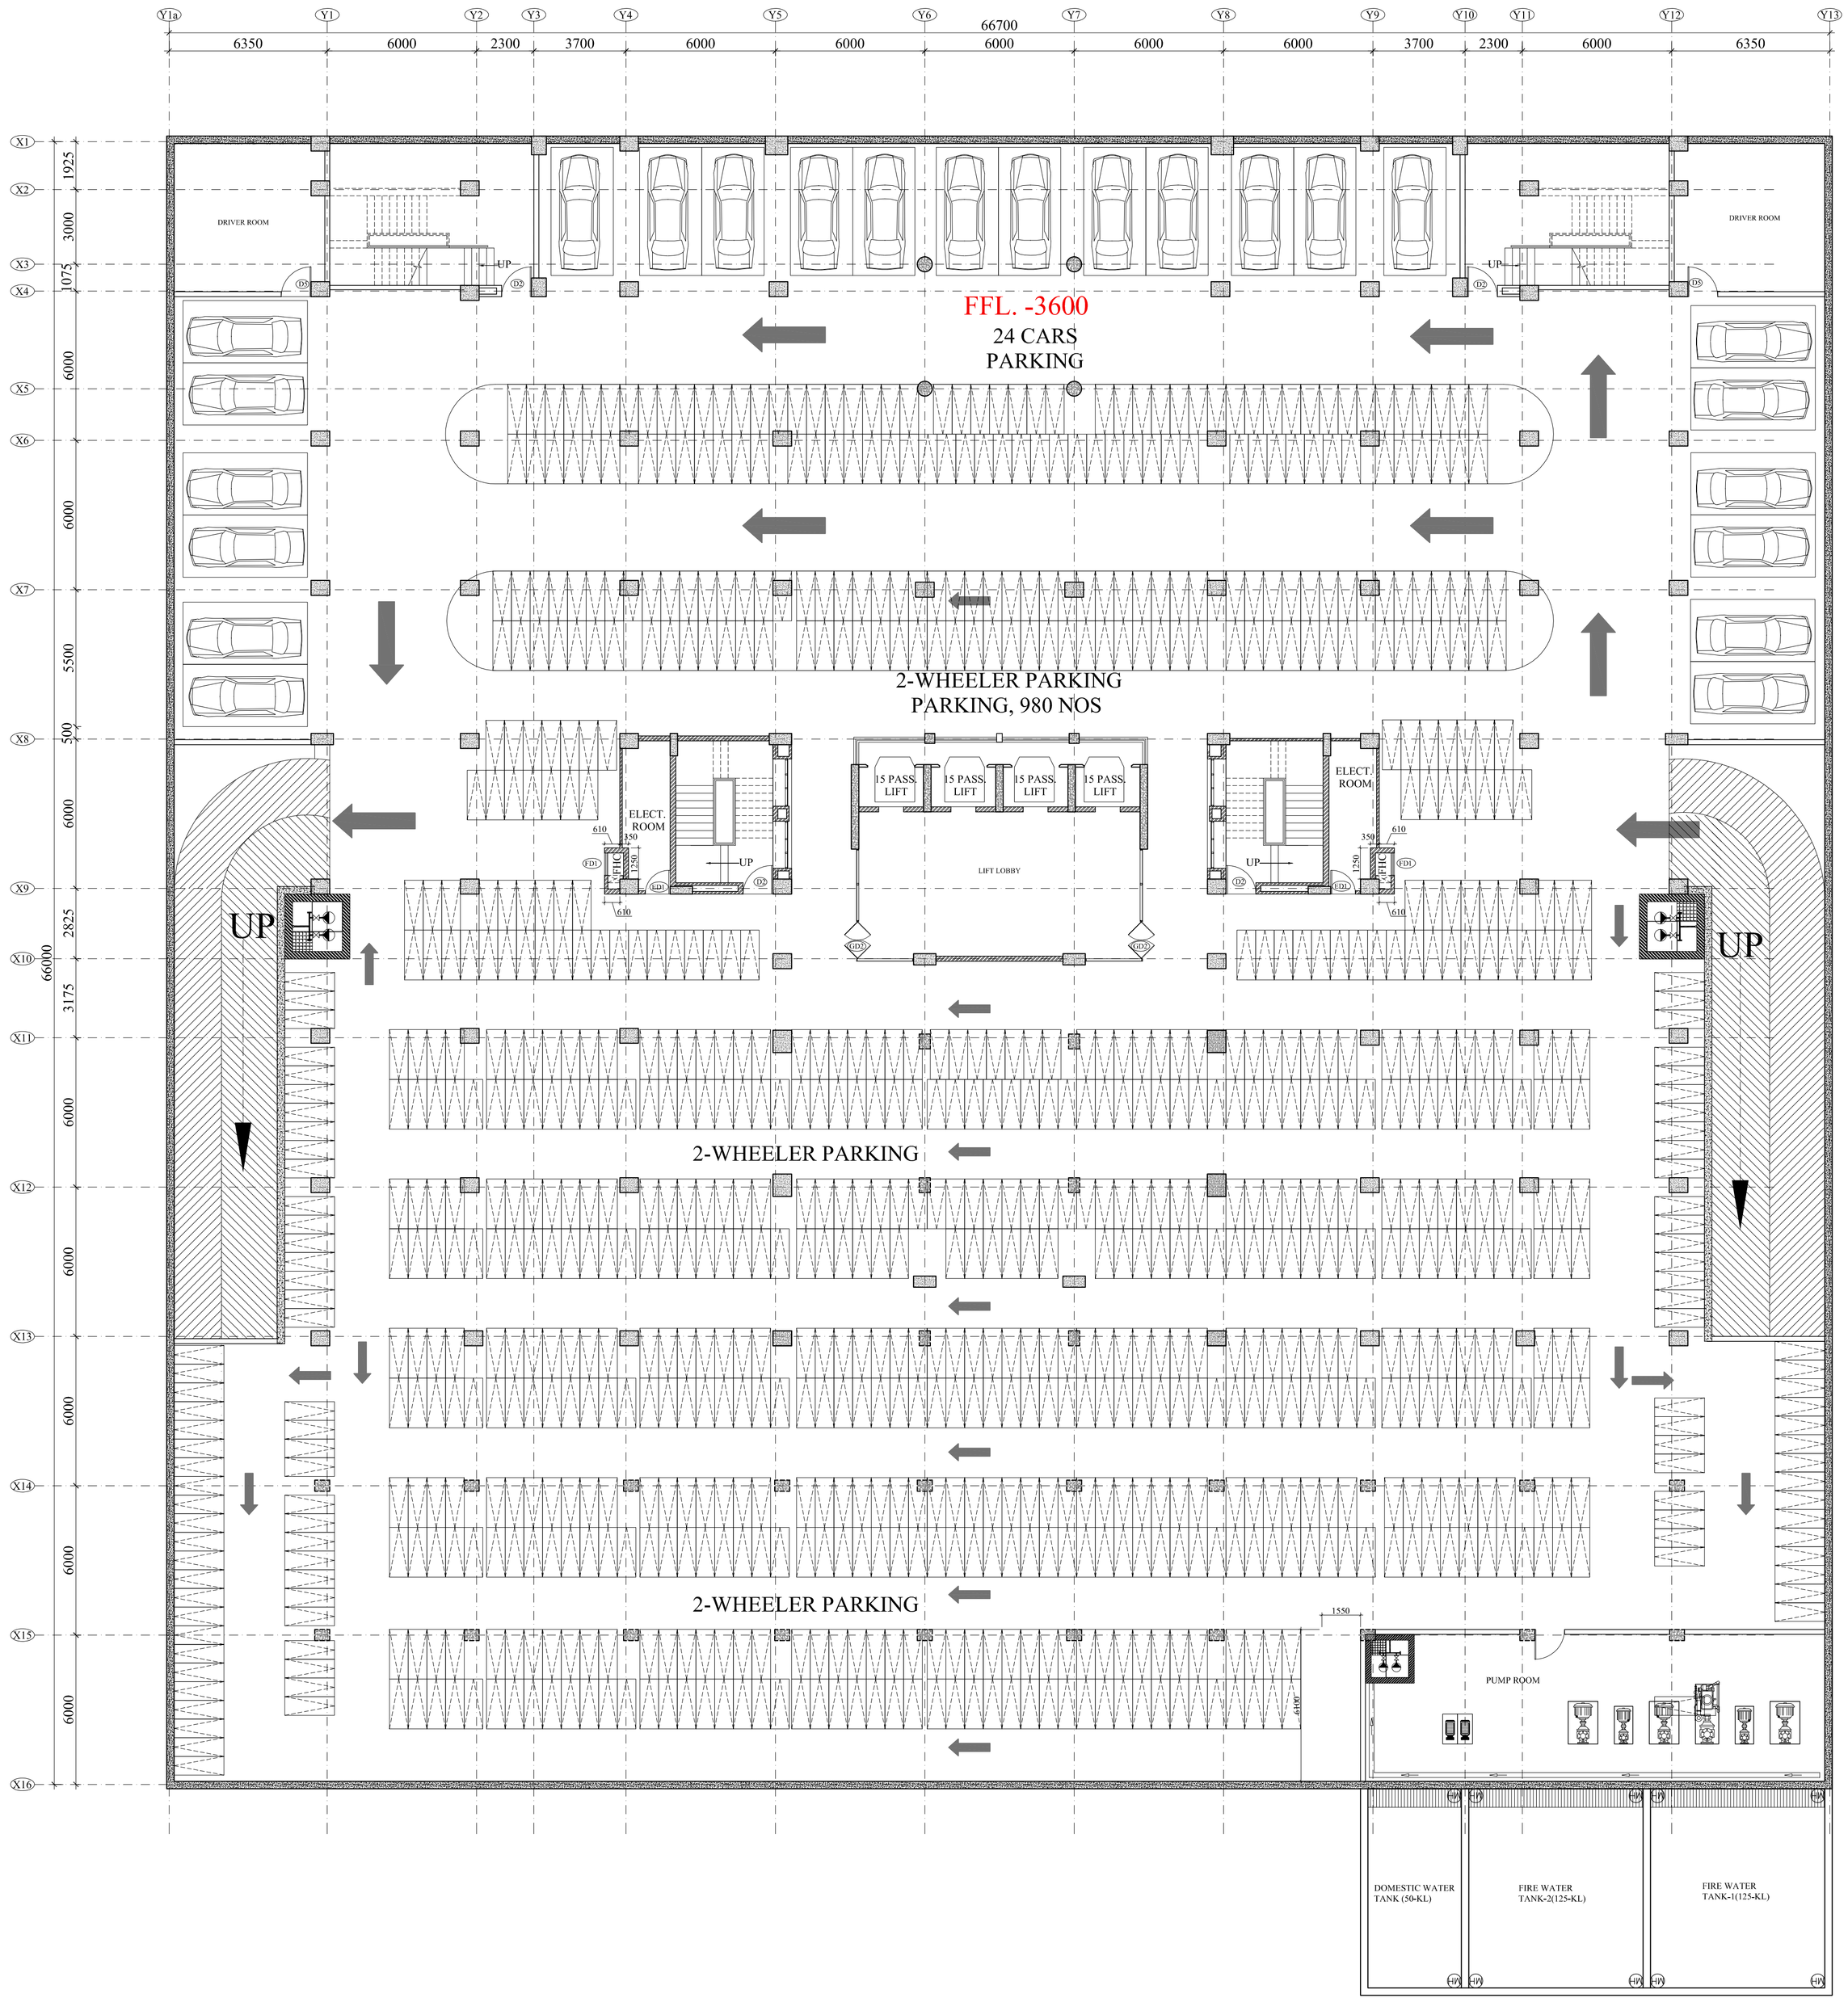

DOOR-WINDOW OPENING SCHEDULE

S.NO.	TYPE	WIDTH	CILL	LINTEL	DISCRIPTION
01	D1	1500	--------	2400	A.H.U. DOOR
02	D2	1200	--------	2400	STAIRCASE DOOR
03	D3	1200	--------	2400	KITCHEN DOOR
04	D3A	1200	--------	2400	PH TOILET DOOR
05	D4	1000	--------	2400	Swing Door w/vision Panel
06	D5	1000	--------	2400	Door for Toilet,Record etc.
07	D6	750	--------	2100	Attached TOILET DOOR
08	D7	2000	--------	2400	ACOUSTICAL DOOR
09	ED1	1200	--------	2400	ELECTRICAL DOOR
10	ED2	750	100	2100	ELECTRICAL DOOR
11	ED3	2000	--------	2400	ELECTRICAL DOOR
12	FD1	900	100	2100	FHC DOOR
13	GD1	1800	--------	2400	SLIDING Glass Door
14	GD2	1500	--------	2400	Double Panel Swing Glass Door
15	GD3	1000	--------	2400	GLASS DOOR
16	GD4	1000	--------	2400	SWING GLASS DOOR
17	GD5	1200	--------	2400	GLASS DOOR
18	GD5A	1200	--------	2400	SWING GLASS DOOR
19	GD6	1150	--------	2400	SWING GLASS DOOR
20	GD7	1800	--------	2400	AUTOMATIC SLIDING DOOR
21	L1	3000	100	B.O.B.	ALUMINIUM LOUVERS
22	L2	1800	100	B.O.B.	ALUMINIUM LOUVERS
23	L3	1000	100	B.O.B.	ALUMINIUM LOUVERS
24	L3A	2000	100	B.O.B.	ALUMINIUM LOUVERS
25	L4	17000	100	B.O.B.	ALUMINIUM LOUVERS
26	G1	16700	--------	AS/ELE.	Double heightGLAZING
27	G1A	16700	--------	AS/ELE.	Double heightGLAZING
28	G2	17000	--------	AS/ELE	GLAZING
29	G2A	17000	--------	AS/ELE	GLAZING
30	G3	16700	--------	AS/ELE	Triple height GLAZING
31	G4	8100	--------	AS/ELE	GLAZING
32	G5	2100	--------	AS/ELE	GLAZING
33	G5A	2100	--------	AS/ELE	GLAZING
34	G6	1900	--------	AS/ELE	GLAZING
35	G7	4600	--------	AS/ELE	GLAZING
36	G8	2100	--------	AS/ELE	GLAZING
37	G8A	2100	--------	AS/ELE	GLAZING
38	OP	As/Plan	--------	B.O.B.	OPENING

THIS DRAWING IS THE PROPERTY OF THE DESIGN ASSOCIATES INC. AND SHALL NOT BE COPIED OR USED IN ANY MANNER WITHOUT PRIOR PERMISSION.

KEY PLAN

NOTES:

1. ALL DIMENSIONS ARE IN MM.
2. ALL DIMENSIONS ARE TO BE READ AND NOT MEASURED.
3. ALL LEVELS ARE IN METERS.
4. GRID DIMENSIONS AND PLOT LINES ARE TO BE STRICTLY ADHERED TO.
5. ALL LEVELS INCLUDING FLOOR LEVELS, CILL & LINTEL LEVELS, LANDING LEVELS, PARAPET HEIGHT/ LEVELS, LEVELS OF HORIZONTAL PROJECTION & BANDS INCLUDING ANY SURFACE FEATURES INDICATED IN THE DRAWINGS ARE TO BE STRICTLY ADHERED TO.
6. IN CASE OF ANY DISCREPANCY BETWEEN ANY DRAWING, ARCHITECT HAS TO BE INFORMED PRIOR TO ANY EXECUTION.

R2		REVISION
R1		REVISION
GFC		GOOD FOR CONSTRUCTION
AC		ADVANCE COPY
MARK	DATE	DESCRIPTION

OWNER-

GOA SHIPYARD LIMITED
(A Govt. of India Undertaking)
VASCO DA GAMA, GOA, 403802
contactus@goashipyard.com
TEL.No: - (0832) 251252-56, 2512359
FAX No: -(0091-832) 2514232, 2512148

EXECUTING AGENCY-

NBCC (INDIA) LIMITED
(Formerly National Buildings Construction Limited
(A Government of India Enterprise)
NBCC Bhawan, Lodhi Road
New Delhi - 110 003, India
Telephone No : 011 - 24367314 - 17, 24367573
Fax : 011 - 24366995

ARCHITECTS-

DESIGN ASSOCIATES INC.
ARCHITECTURE
A - 163, Sector - 136,
Noida - Greater Noida Expressway,
Noida - 201301, Phone no: 0120-2428600/30
e-mail: matinder.sharma@designassociates.in

MECHANICAL CONSULTANT-
DESIGN CENTER CONSULTING ENGINEERS, NEW DELHI

ELECTRICAL CONSULTANT-
DESIGN CENTER CONSULTING ENGINEERS, NEW DELHI

PLUMBING CONSULTANT-
DESIGN CENTER CONSULTING ENGINEERS, NEW DELHI

STRUCTURE CONSULTANT-
LKT ENGINEERING CONSULTANTS LTD.
10/49, Subhash Nagar,New Delhi-110027
Phone :+011-45565818,Tel/Fax:+011-25126129
info@lktengineering.com
http:\-www.lktengineering.com

PROJECT-
CONSTRUCTION OF MCMV OFFICE BUILDING AT GOA SHIPYARD, GOA


DRAWING TITLE-
BASEMENT FLOOR PLAN

DRAWING PURPOSE-
TENDER DRAWING

JOB NO. -	DWG. REF. NO.-	DATE-
538	----------	----------
SCALE- 1:130	REVISION- ----------	DATE OF ISSUE- 03.01.17

DWG. NO.-
538/GSL/TD/AR/151

	SHEET SIZE-	SHEET NO-
	A1	01
	DRAWN BY- RAJEEV	CHECKED BY- MATINDER

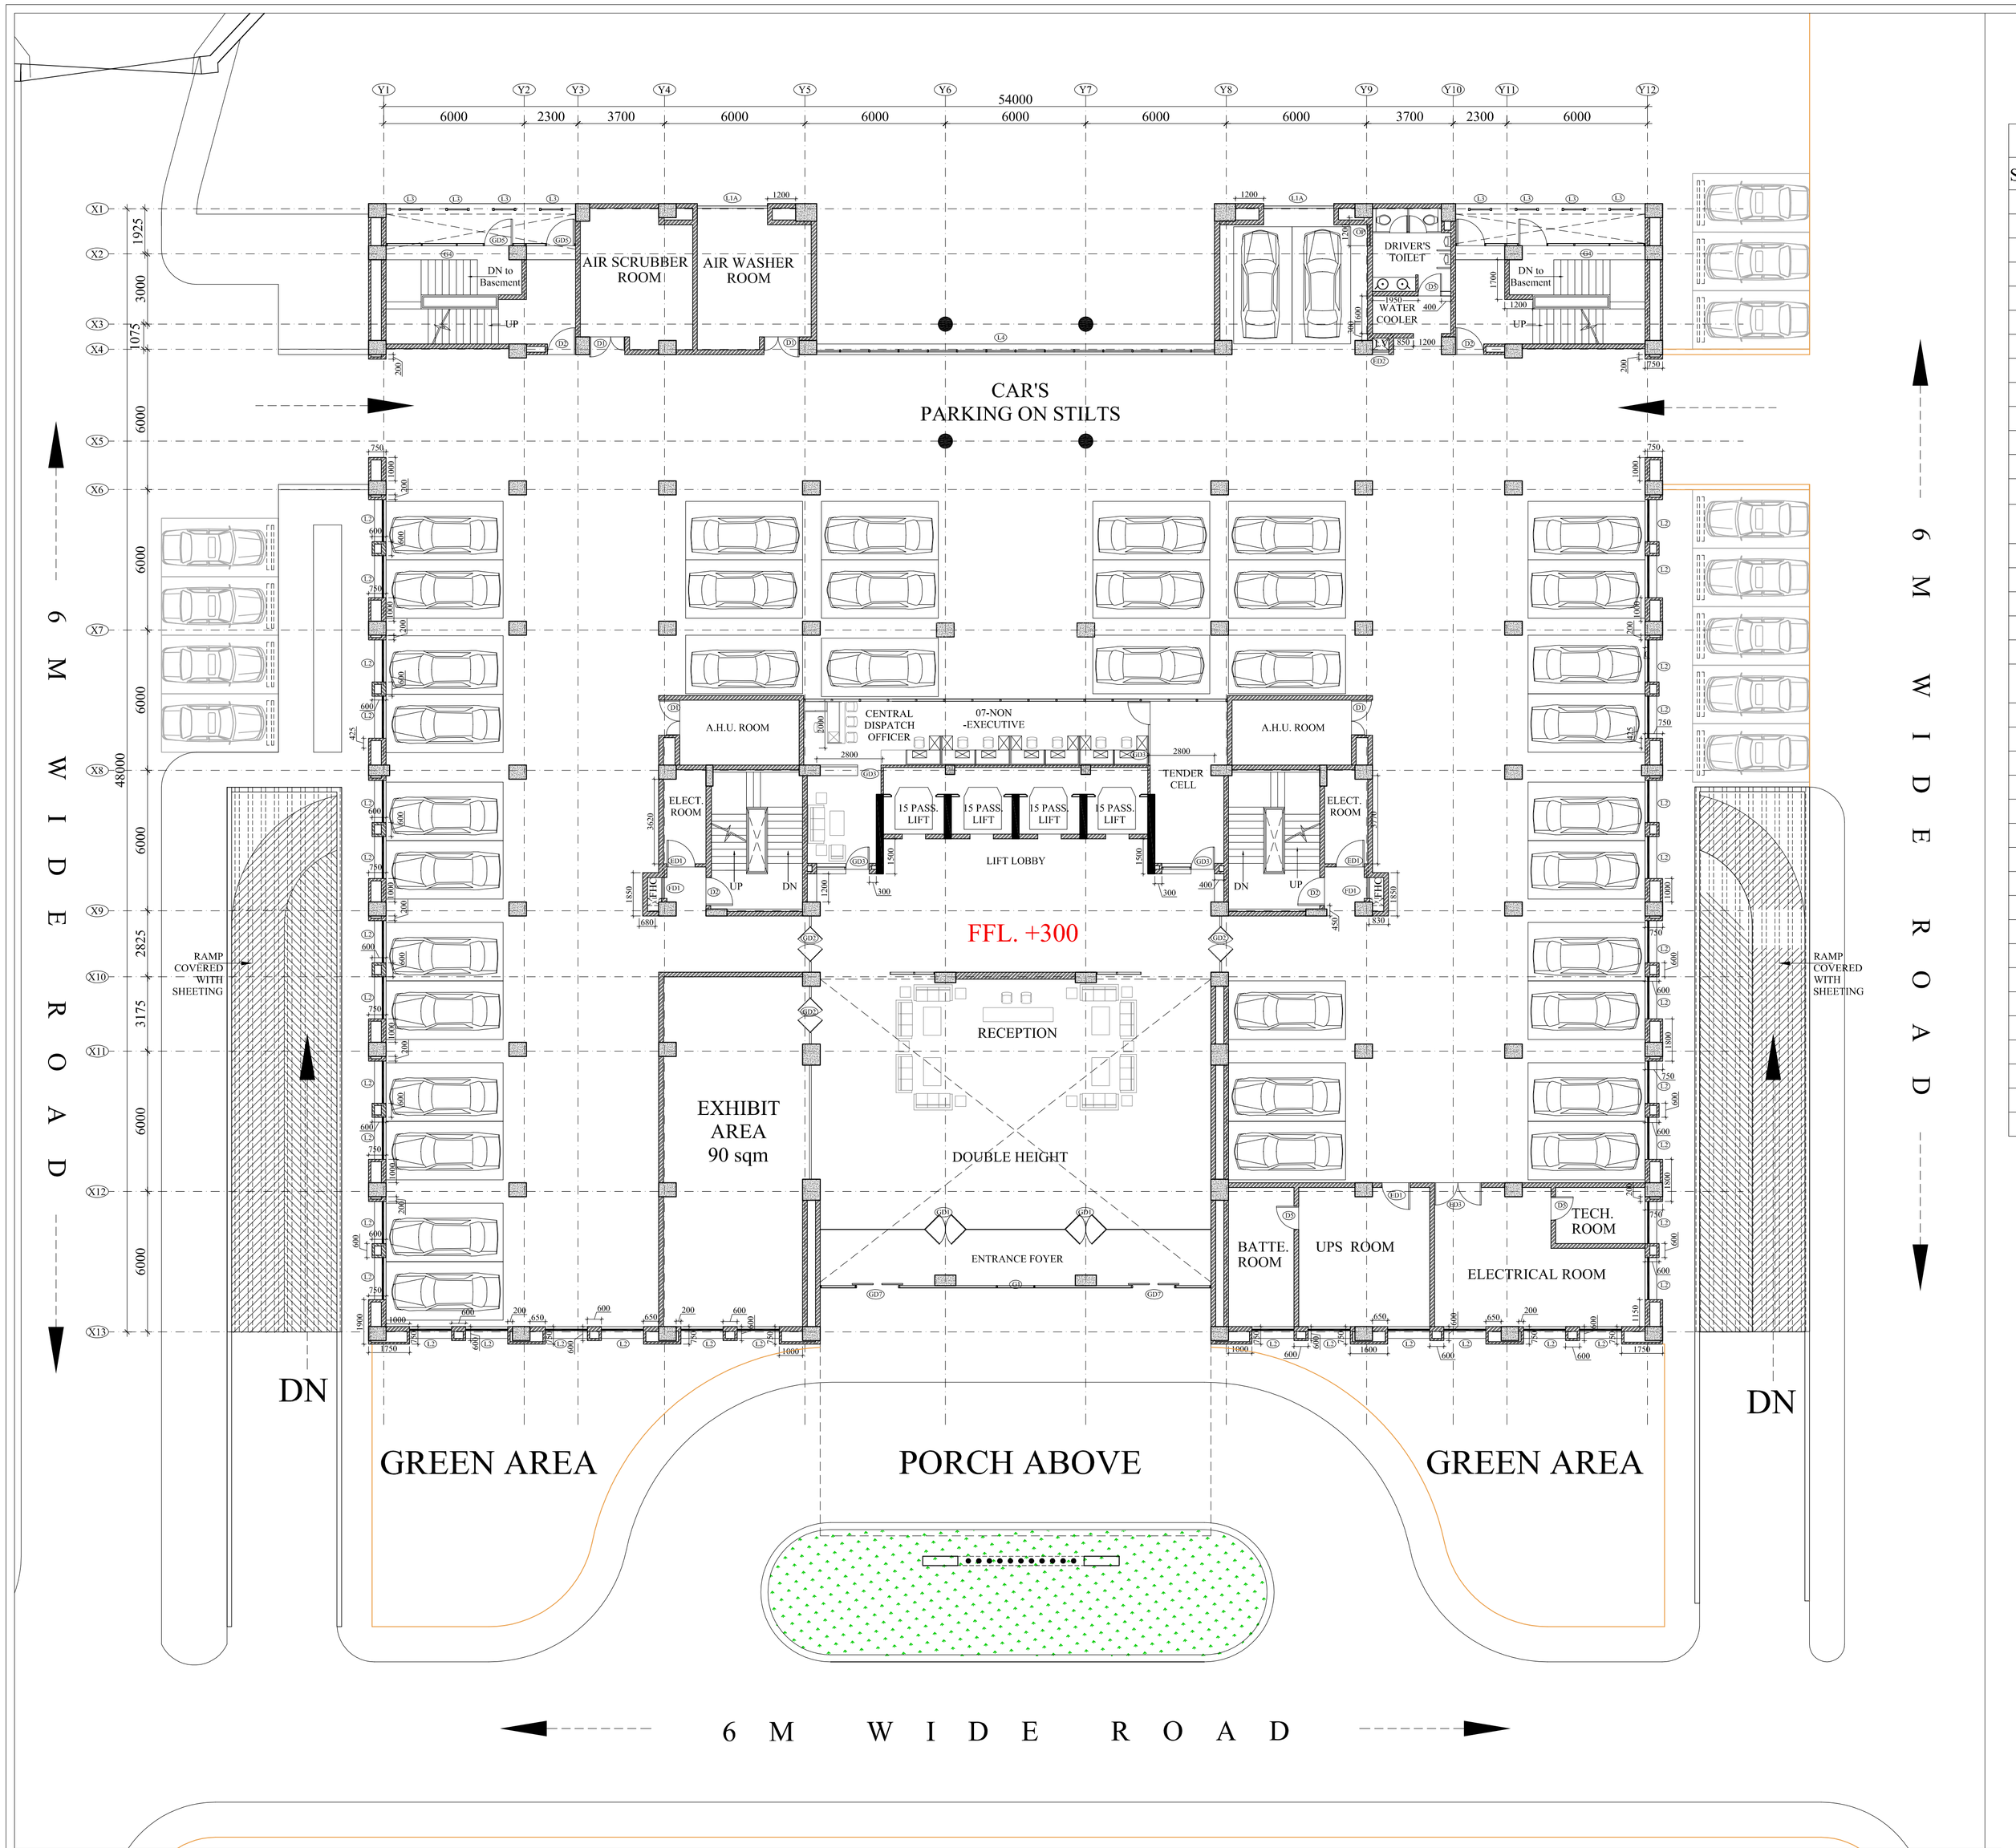

STILT FLOOR PLAN
(RECEPTION LOBBY,MCMV CETRAL DISPATCH +TENDER+EXHIBIT AREA)

DOOR-WINDOW OPENING SCHEDULE

S.NO.	TYPE	WIDTH	CILL	LINTEL	DISCRIPTION
01	D1	1500	-------	2400	A.H.U. DOOR (Fire door)
02	D2	1200	-------	2400	STAIRCASE DOOR
03	D3	1200	-------	2400	KITCHEN DOOR
04	D3A	1200	-------	2400	PH TOILET DOOR
05	D4	1000	-------	2400	Swing Door w/vision Panel
06	D5	1000	-------	2400	Door for Toilet,Record etc.
07	D6	750	-------	2100	Attached TOILET DOOR
08	D7	2000	-------	2400	ACOUSTICAL DOOR
09	ED1	1200	-------	2400	ELECTRICAL DOOR
10	ED2	750	100	2100	ELECTRICAL DOOR
11	ED3	2000	-------	2400	ELECTRICAL DOOR
12	FD1	900	100	2100	FHC DOOR
13	GD1	1800	-------	2400	SWING Glass Door
14	GD2	1500	-------	2400	Double Panel Swing Glass Door
15	GD3	1000	-------	2400	GLASS DOOR
16	GD4	1000	-------	2400	SWING GLASS DOOR
17	GD5	1200	-------	2400	GLASS DOOR
18	GD5A	1200	-------	2400	SWING GLASS DOOR
19	GD6	1150	-------	2400	SWING GLASS DOOR
20	GD7	1800	-------	2400	AUTOMATIC SLIDING DOOR
21	L1	3000	100	B.O.B.	ALUMINIUM LOUVERS
22	L2	1800	100	B.O.B.	ALUMINIUM LOUVERS
23	L3	1000	100	B.O.B.	ALUMINIUM LOUVERS
24	L3A	2000	100	B.O.B.	ALUMINIUM LOUVERS
25	L4	17000	100	B.O.B.	ALUMINIUM LOUVERS
26	G1	16700	--------	AS/ELE.	Double heightGLAZING
27	G1A	16700	--------	AS/ELE.	Double heightGLAZING
28	G2	17000	--------	AS/ELE	GLAZING
29	G2A	17000	--------	AS/ELE	GLAZING
30	G3	16700	--------	AS/ELE	Triple height GLAZING
31	G4	8100	--------	AS/ELE	GLAZING
32	G5	2100	--------	AS/ELE	GLAZING
33	G5A	2100	--------	AS/ELE	GLAZING
34	G6	1900	--------	AS/ELE	GLAZING
35	G7	4600	--------	AS/ELE	GLAZING
36	G8	2100	--------	AS/ELE	GLAZING
37	G8A	2100	--------	AS/ELE	GLAZING
38	OP	As/Plan	--------	B.O.B.	OPENING

THIS DRAWING IS THE PROPERTY OF THE DESIGN ASSOCIATES INC. AND SHALL NOT BE COPIED OR USED IN ANY MANNER WITHOUT PRIOR PERMISSION.

KEY PLAN

NOTES:

1. ALL DIMENSIONS ARE IN MM.
2. ALL DIMENSIONS ARE TO BE READ AND NOT MEASURED.
3. ALL LEVELS ARE IN METERS.
4. GRID DIMENSIONS AND PLOT LINES ARE TO BE STRICTLY ADHERED TO.
5. ALL LEVELS INCLUDING FLOOR LEVELS, CILL & LINTEL LEVELS, LANDING LEVELS, PARAPET HEIGHT/ LEVELS, LEVELS OF HORIZONTAL PROJECTION & BANDS INCLUDING ANY SURFACE FEATURES INDICATED IN THE DRAWINGS ARE TO BE STRICTLY ADHERED TO.
6. IN CASE OF ANY DISCREPANCY BETWEEN ANY DRAWING, ARCHITECT HAS TO BE INFORMED PRIOR TO ANY EXECUTION.

MARK	DATE	DESCRIPTION
R2		REVISION
R1		REVISION
GFC		GOOD FOR CONSTRUCTION
AC		ADVANCE COPY

OWNER-

GOA SHIPYARD LIMITED
(A Govt. of India Undertaking)
VASCO DA GAMA, GOA, 403802
contactus@goashipyard.com
TEL.No: - (0832) 251252-56, 2512359
FAX No: -(0091-832) 2514232, 2512148

EXECUTING AGENCY-

NBCC (INDIA) LIMITED
(Formerly National Buildings Construction Limited
(A Government of India Enterprise)
NBCC Bhawan, Lodhi Road
New Delhi - 110 003, India
Telephone No : 011 - 24367314 - 17, 24367573
Fax : 011 - 24366995

ARCHITECTS-

DESIGN ASSOCIATES INC.
A - 163, Sector - 136,
Noida - Greater Noida Expressway,
Noida - 201301, Phone no: 0120-2428600/30
e-mail: matinder.sharma@designassociates.in

MECHANICAL CONSULTANT-
DESIGN CENTER CONSULTING ENGINEERS, NEW DELHI

ELECTRICAL CONSULTANT-
DESIGN CENTER CONSULTING ENGINEERS, NEW DELHI

PLUMBING CONSULTANT-
DESIGN CENTER CONSULTING ENGINEERS, NEW DELHI


STRUCTURE CONSULTANT-
LKT ENGINEERING CONSULTANTS LTD.
10/49, Subhash Nagar,New Delhi-110027
Phone:+011-45565818,Tel/Fax:+011-25126129
info@lktengineering.com
http://www.lktengineering.com

PROJECT-
CONSTRUCTION OF MCMV OFFICE BUILDING AT GOA SHIPYARD, GOA

DRAWING TITLE-
STILT FLOOR PLAN

DRAWING PURPOSE-
TENDER DRAWING

JOB NO. -	DWG. REF. NO.-	DATE-
538	----------	----------
SCALE- 1:130	REVISION- ----------	DATE OF ISSUE- 03.01.17
DWG. NO.- 538/GSL/TD/AR/152		
	SHEET SIZE- A1	SHEET NO- 02
	DRAWN BY- RAJEEV	CHECKED BY- MATINDER

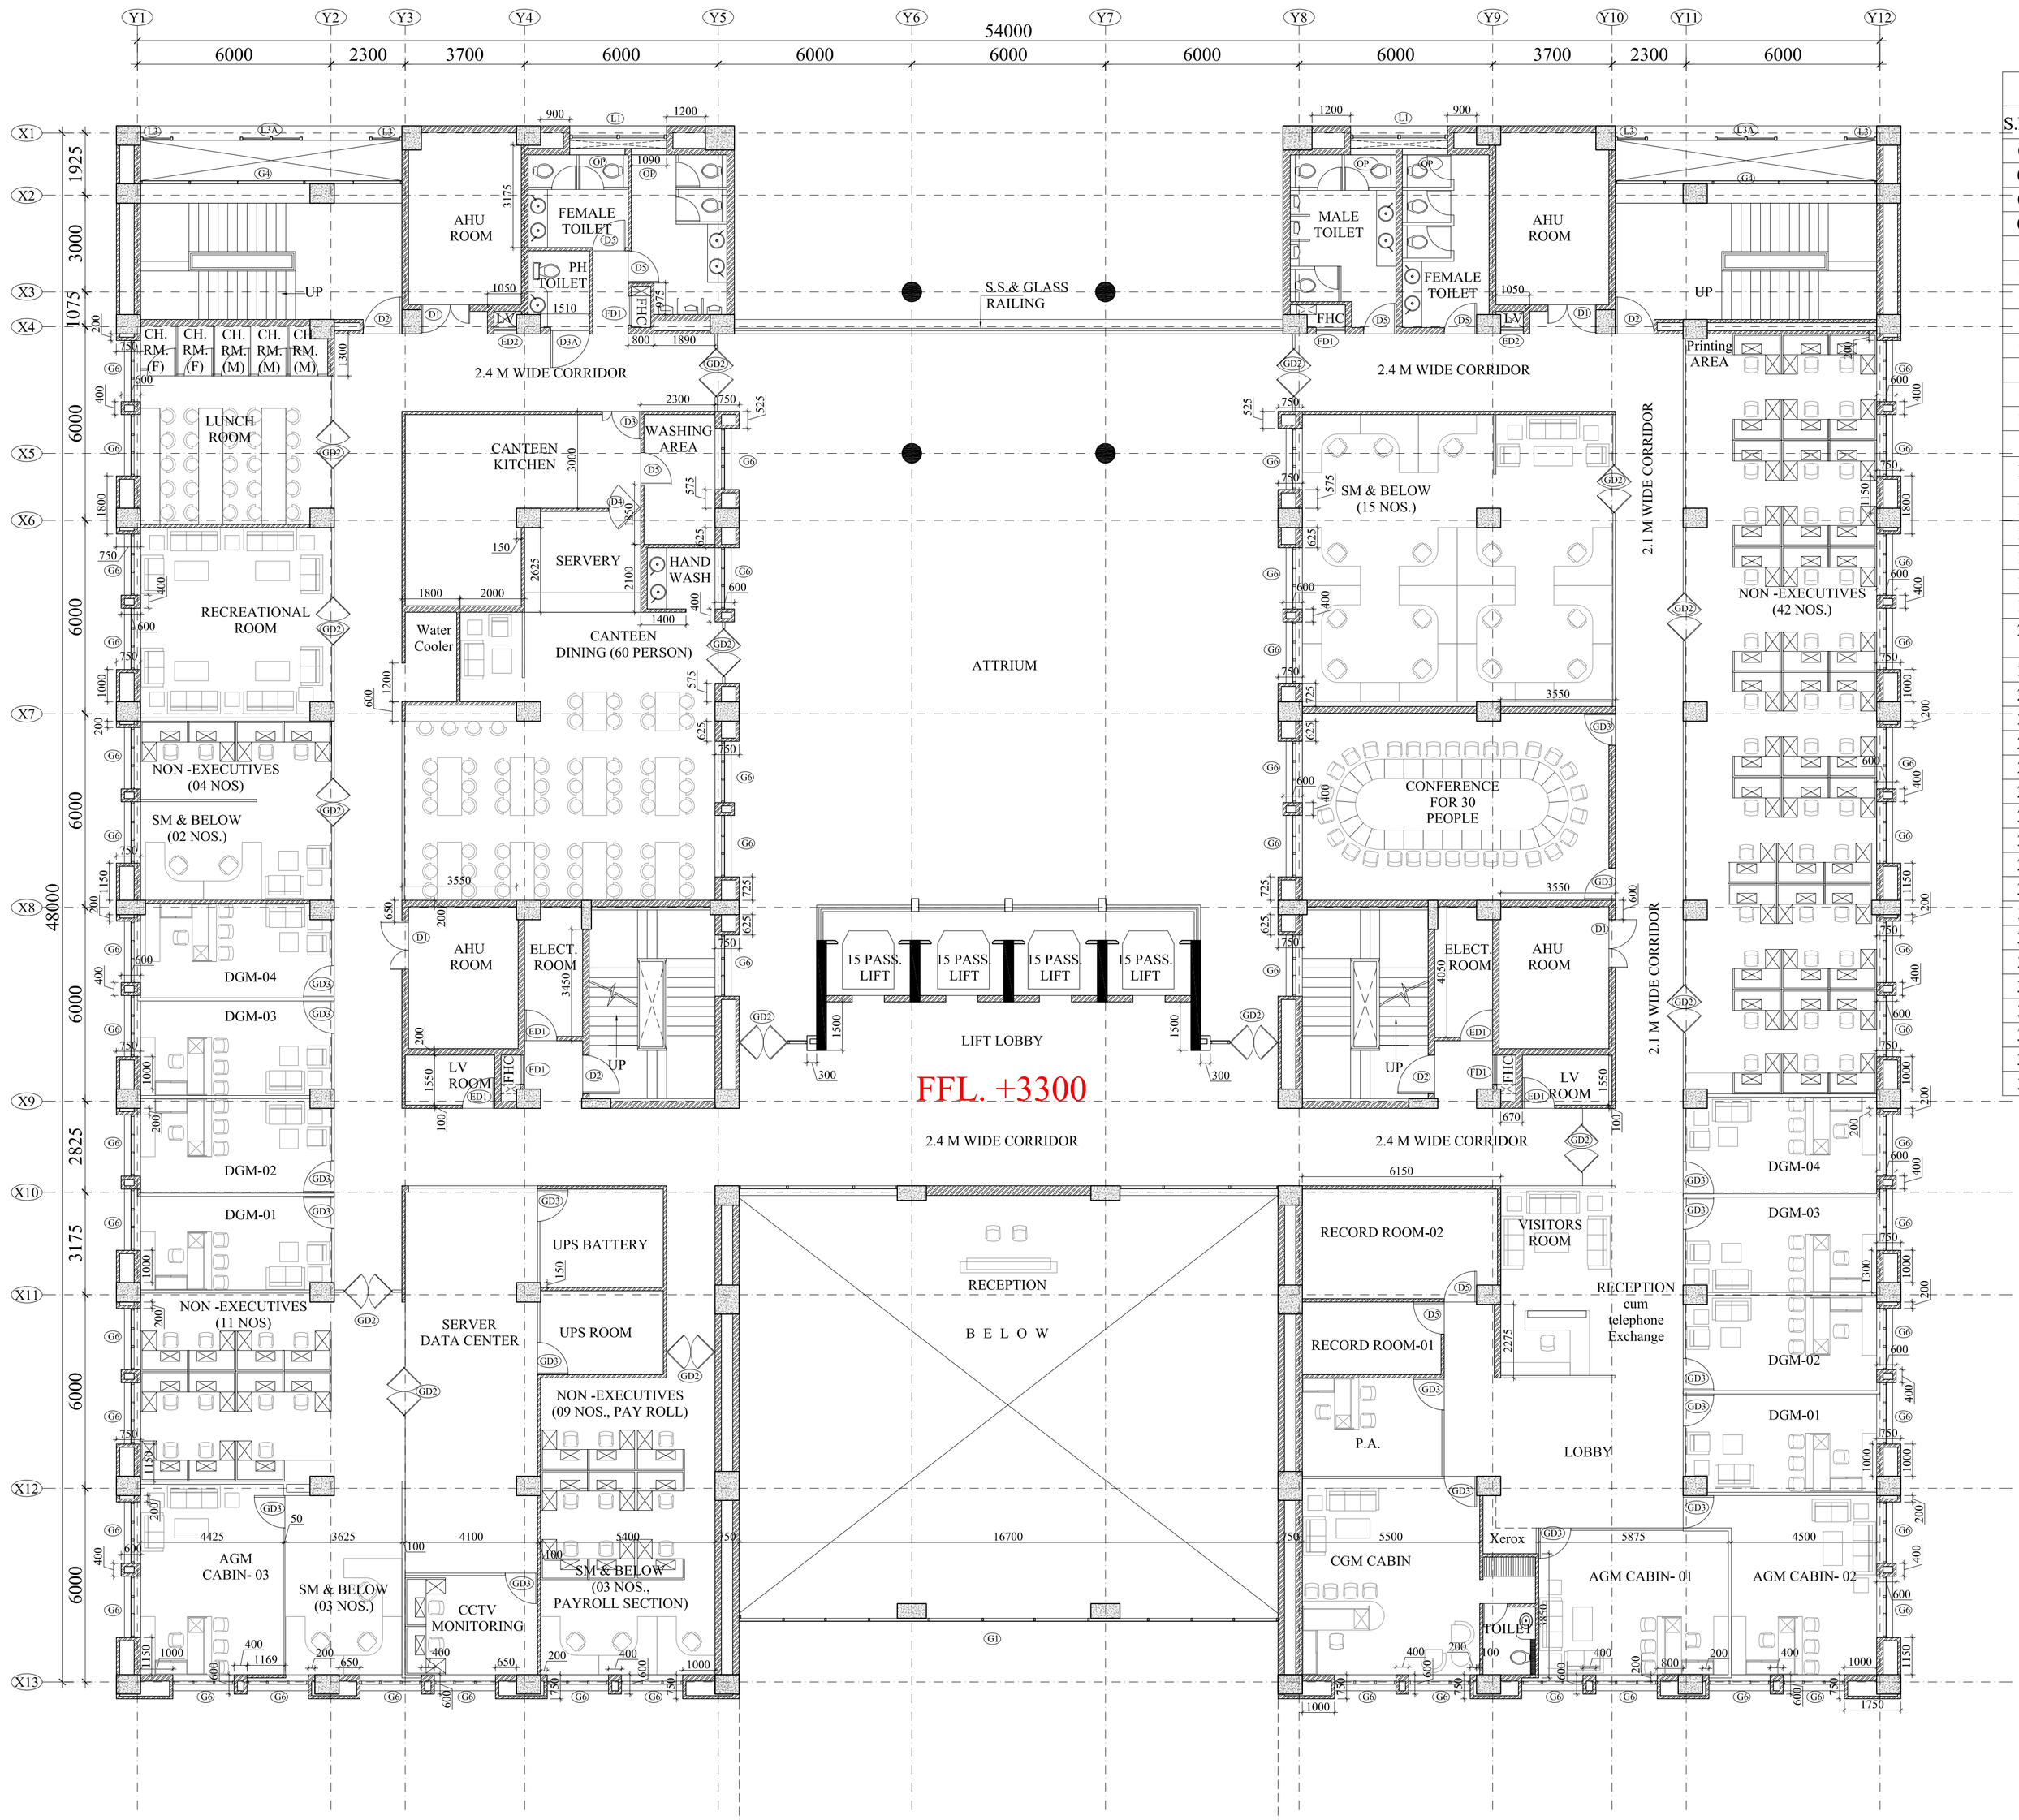

FIRST FLOOR PLAN
(MCMV HR&A +MCMV IT+MCMV PAYROLL +SUNDRY+CANTEEN+LUNCH ROOM)

DOOR-WINDOW OPENING SCHEDULE

S.NO.	TYPE	WIDTH	CILL	LINTEL	DISCRIPTION
01	D1	1500	-------	2400	A.H.U. DOOR
02	D2	1200	-------	2400	STAIRCASE DOOR
03	D3	1200	-------	2400	KITCHEN DOOR
04	D3A	1200	-------	2400	PH TOILET DOOR
05	D4	1000	-------	2400	Swing Door w/vision Panel
06	D5	1000	-------	2400	Door for Toilet,Record etc.
07	D6	750	-------	2100	Attached TOILET DOOR
08	D7	2000	-------	2400	ACOUSTICAL DOOR
09	ED1	1200	-------	2400	ELECTRICAL DOOR
10	ED2	750	100	2100	ELECTRICAL DOOR
11	ED3	2000	-------	2400	ELECTRICAL DOOR
12	FD1	900	100	2100	FHC DOOR
13	GD1	1800	-------	2400	SLIDING Glass Door
14	GD2	1500	-------	2400	Double Panel Swing Glass Door
15	GD3	1000	-------	2400	GLASS DOOR
16	GD4	1000	-------	2400	SWING GLASS DOOR
17	GD5	1200	-------	2400	GLASS DOOR
18	GD5A	1200	-------	2400	SWING GLASS DOOR
19	GD6	1150	-------	2400	SWING GLASS DOOR
20	GD7	1800	-------	2400	AUTOMATIC SLIDING DOOR
21	L1	3000	100	B.O.B.	ALUMINIUM LOUVERS
22	L2	1800	100	B.O.B.	ALUMINIUM LOUVERS
23	L3	1000	100	B.O.B.	ALUMINIUM LOUVERS
24	L3A	2000	100	B.O.B.	ALUMINIUM LOUVERS
25	L4	17000	100	B.O.B.	ALUMINIUM LOUVERS
26	G1	16700	--------	AS/ELE.	Double heightGLAZING
27	G1A	16700	--------	AS/ELE.	Double heightGLAZING
28	G2	17000	--------	AS/ELE	GLAZING
29	G2A	17000	--------	AS/ELE	GLAZING
30	G3	16700	--------	AS/ELE	Triple height GLAZING
31	G4	8100	--------	AS/ELE	GLAZING
32	G5	2100	--------	AS/ELE	GLAZING
33	G5A	2100	--------	AS/ELE	GLAZING
34	G6	1900	--------	AS/ELE	GLAZING
35	G7	4600	--------	AS/ELE	GLAZING
36	G8	2100	--------	AS/ELE	GLAZING
37	G8A	2100	--------	AS/ELE	GLAZING
38	OP	As/Plan	--------	B.O.B.	OPENING

THIS DRAWING IS THE PROPERTY OF THE DESIGN ASSOCIATES INC. AND SHALL NOT BE COPIED OR USED IN ANY MANNER WITHOUT PRIOR PERMISSION.

KEY PLAN

NOTES:

1. ALL DIMENSIONS ARE IN MM.
2. ALL DIMENSIONS ARE TO BE READ AND NOT MEASURED.
3. ALL LEVELS ARE IN METERS.
4. GRID DIMENSIONS AND PLOT LINES ARE TO BE STRICTLY ADHERED TO.
5. ALL LEVELS INCLUDING FLOOR LEVELS, CILL & LINTEL LEVELS, LANDING LEVELS, PARAPET HEIGHT/ LEVELS, LEVELS OF HORIZONTAL PROJECTION & BANDS INCLUDING ANY SURFACE FEATURES INDICATED IN THE DRAWINGS ARE TO BE STRICTLY ADHERED TO.
6. IN CASE OF ANY DISCREPANCY BETWEEN ANY DRAWING, ARCHITECT HAS TO BE INFORMED PRIOR TO ANY EXECUTION.

R2		REVISION
R1		REVISION
GFC		GOOD FOR CONSTRUCTION
AC		ADVANCE COPY
MARK	DATE	DESCRIPTION

OWNER-

GOA SHIPYARD LIMITED
(A Govt. of India Undertaking)
VASCO DA GAMA, GOA, 403802
contactus@goashipyard.com
TEL.No: - (0832) 251252-56, 2512359
FAX No: -(0091-832) 2514232, 2512148

EXECUTING AGENCY-

NBCC (INDIA) LIMITED
(Formerly National Buildings Construction Limited
(A Government of India Enterprise)
NBCC Bhawan, Lodhi Road
New Delhi - 110 003, India
Telephone No : 011 - 24367314 - 17, 24367573
Fax : 011 - 24366995

ARCHITECTS-

DESIGN ASSOCIATES INC.
ARCHITECTURE
A - 163, Sector - 136,
Noida - Greater Noida Expressway,
Noida - 201301, Phone no: 0120-2428600/30
e-mail: matinder.sharma@designassociates.in

MECHANICAL CONSULTANT-
DESIGN CENTER CONSULTING ENGINEERS, NEW DELHI

ELECTRICAL CONSULTANT-
DESIGN CENTER CONSULTING ENGINEERS, NEW DELHI

PLUMBING CONSULTANT-
DESIGN CENTER CONSULTING ENGINEERS, NEW DELHI

STRUCTURE CONSULTANT-
LKT ENGINEERING CONSULTANTS LTD.
10/49, Subhash Nagar,New Delhi-110027
Phone :+011-45565818,Tel/Fax:+011-25126129
info@lktengineering.com
http:\www.lktengineering.com

PROJECT-
CONSTRUCTION OF MCMV OFFICE BUILDING AT GOA SHIPYARD, GOA

DRAWING TITLE-
FIRST FLOOR PLAN

DRAWING PURPOSE-
TENDER DRAWING

JOB NO. -	DWG. REF. NO.-	DATE-
538	----------	----------
SCALE-	REVISION-	DATE OF ISSUE-
1:110	----------	03.01.17

DWG. NO.-
538/GSL/TD/AR/153

	SHEET SIZE-	SHEET NO-
	A1	03
	DRAWN BY-	CHECKED BY-
	RAJEEV	MATINDER