


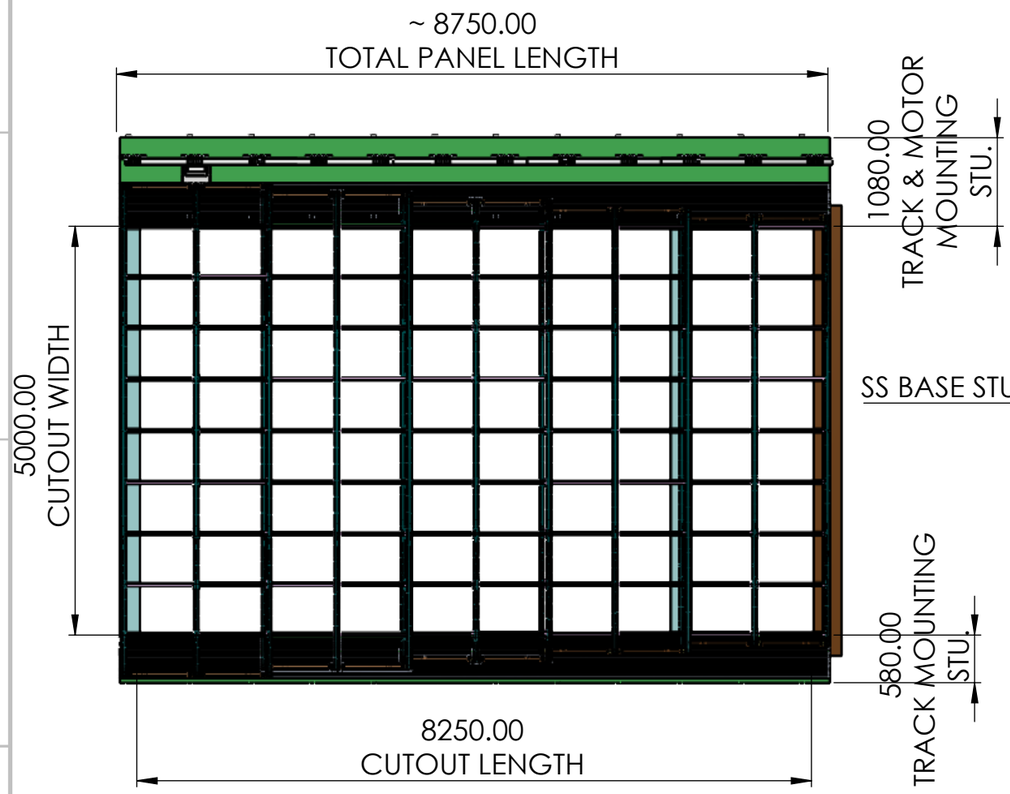


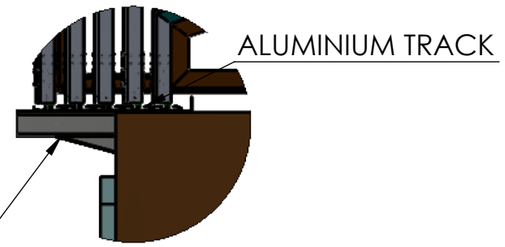


DETAIL A
SCALE 1 : 20

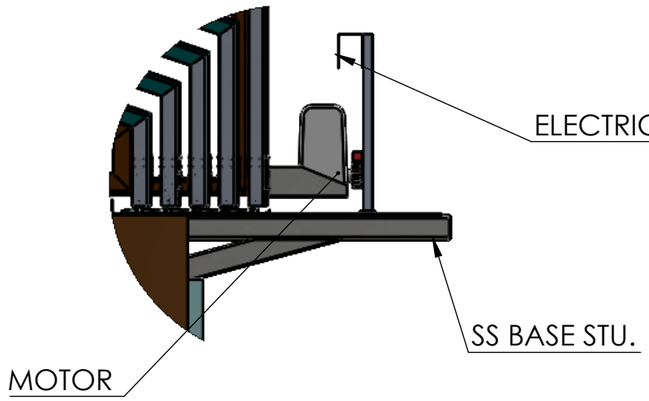


DETAIL B
SCALE 1 : 20

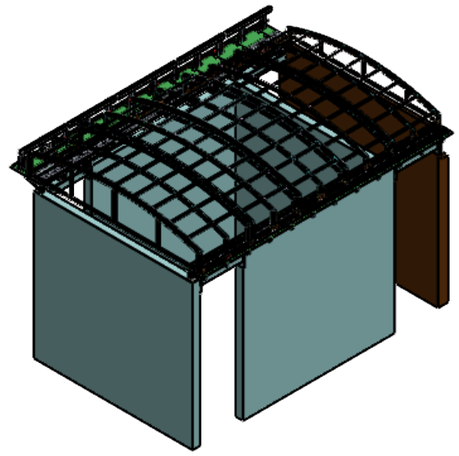


100% CLOSE

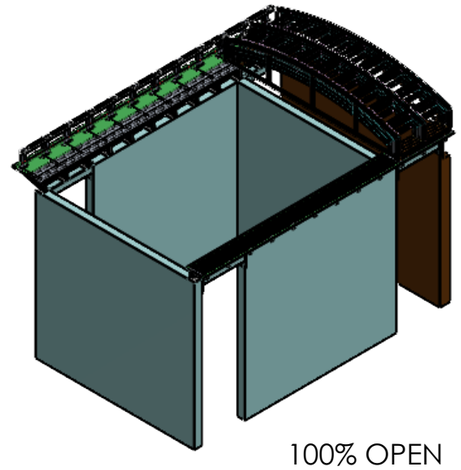

100% OPEN

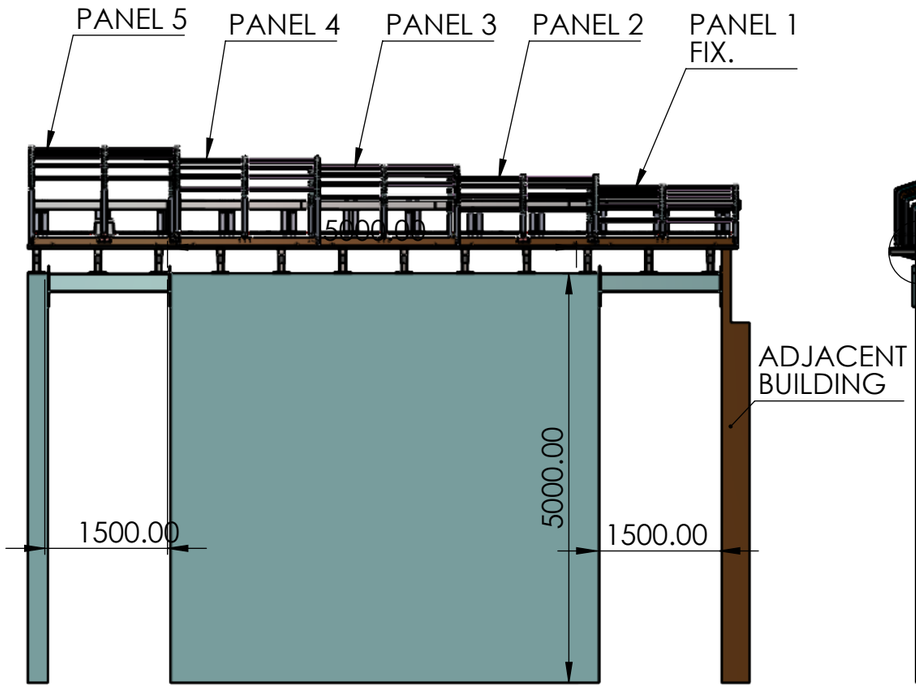

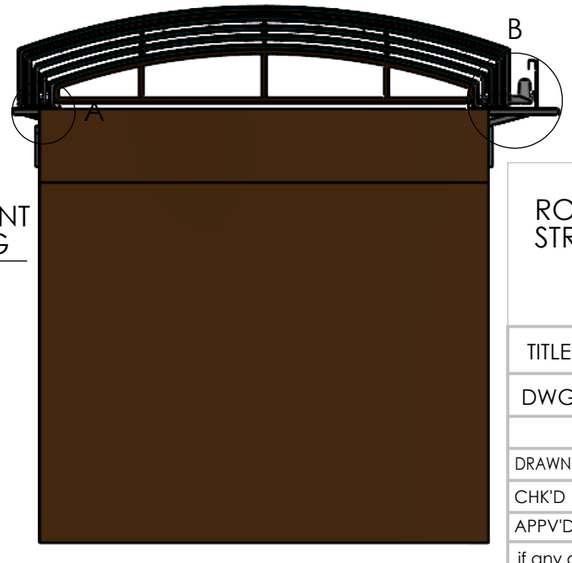

ROOFING SHEET - ALUMINIUM PANEL MIN THICKNESS 1 MM
STRUCTURAL MEMBERS - TRACK MOUNTING BASE FRAME STRUCTURE ABOVE THE WALL MADE UP WITH SS.

TITLE - RETRACTABLE ROOF				NIHVA TECHNOLOGIES PVT.LTD.PUNE
DWG NO - NTPL-PM-01-00-00-00				Website - www.nihva.com
	NAME	SIGNATURE	DATE	PROJECT NO - NTPL-PM-189
DRAWN	J.P		17-11-2025	PRODUCT - RETRACTABLE ROOF
CHK'D	B.S.		17-11-2025	SITE LOCATION - TRIVANDRUM
APPV'D	V.T.		17-11-2025	
if any queries contact - Design@nihva.com				REVISION - QTY - 1
ALL DIMENSION ARE IN mm		A3		SCALE - SHEET 1 OF 1