



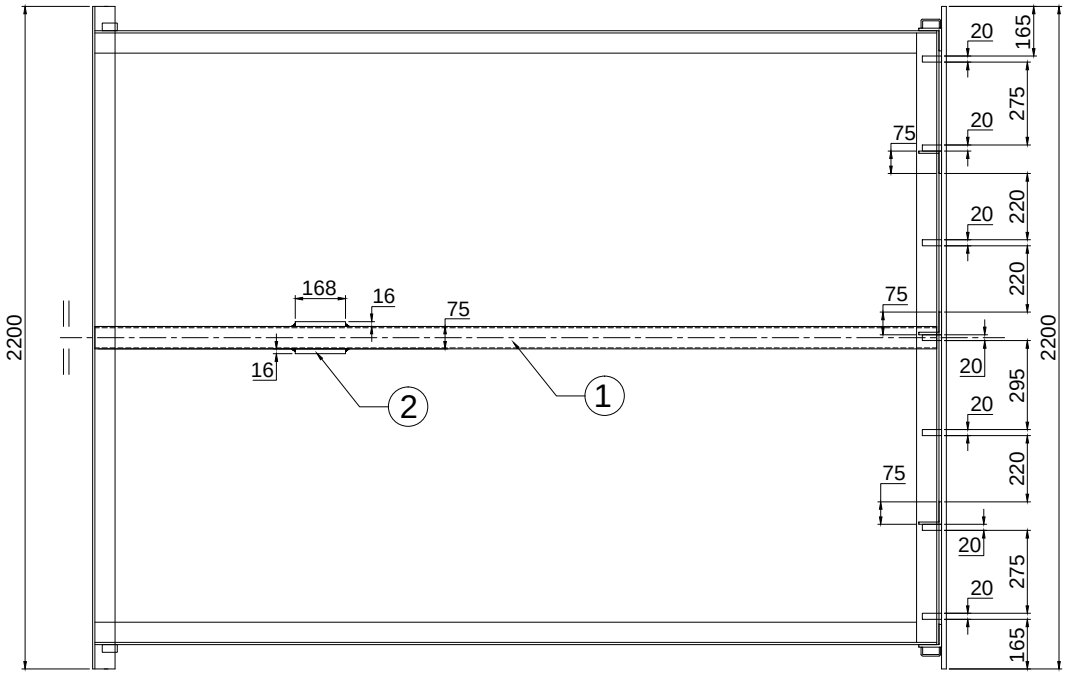


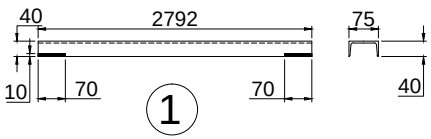

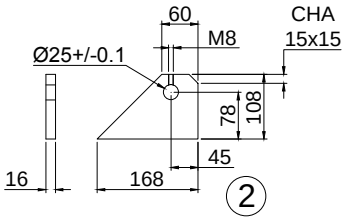

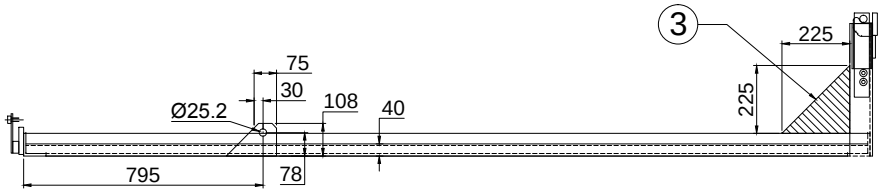

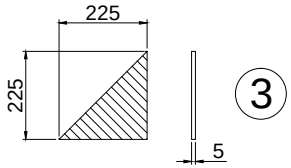

NOTE:~ MTL : MS

1. ISMC 75 X 40 X 2792L = 1 NO (NOTCH) (SEE DRG)
2. PROFILE 108 X 16 X 168L = 2 NOS (SEE DRG)
3. GUSSET 225 X 5 X 225L = 2 NOS (SEE DRG)

TOLERANCE - ±5mm

This drawing & design is the property of NIHVA TECHNOLOGIES. Not to be sold or copied to any other concern.

TITLE: DECK CYL MOUNTING			NIHVA TECHNOLOGIES PVT. LTD. PUNE Tel : 020 66304033 Email:- info@nihva.com Website:- www.nihva.com
NAME	SIGN	DATE	
DRAWN P.A			CLIENT -
CHECK SHEKHAR			PROJECT - DLBJ1001
APPRD. SHEKHAR			SITE LOCATION -
If any queries contact : design@nihva.com			DWG. NO. : NIHVA/17-18/ REV- 0
ALL DIMENSION ARE IN mm			SCALE: NTS WT: SHEET: 01 OF 01