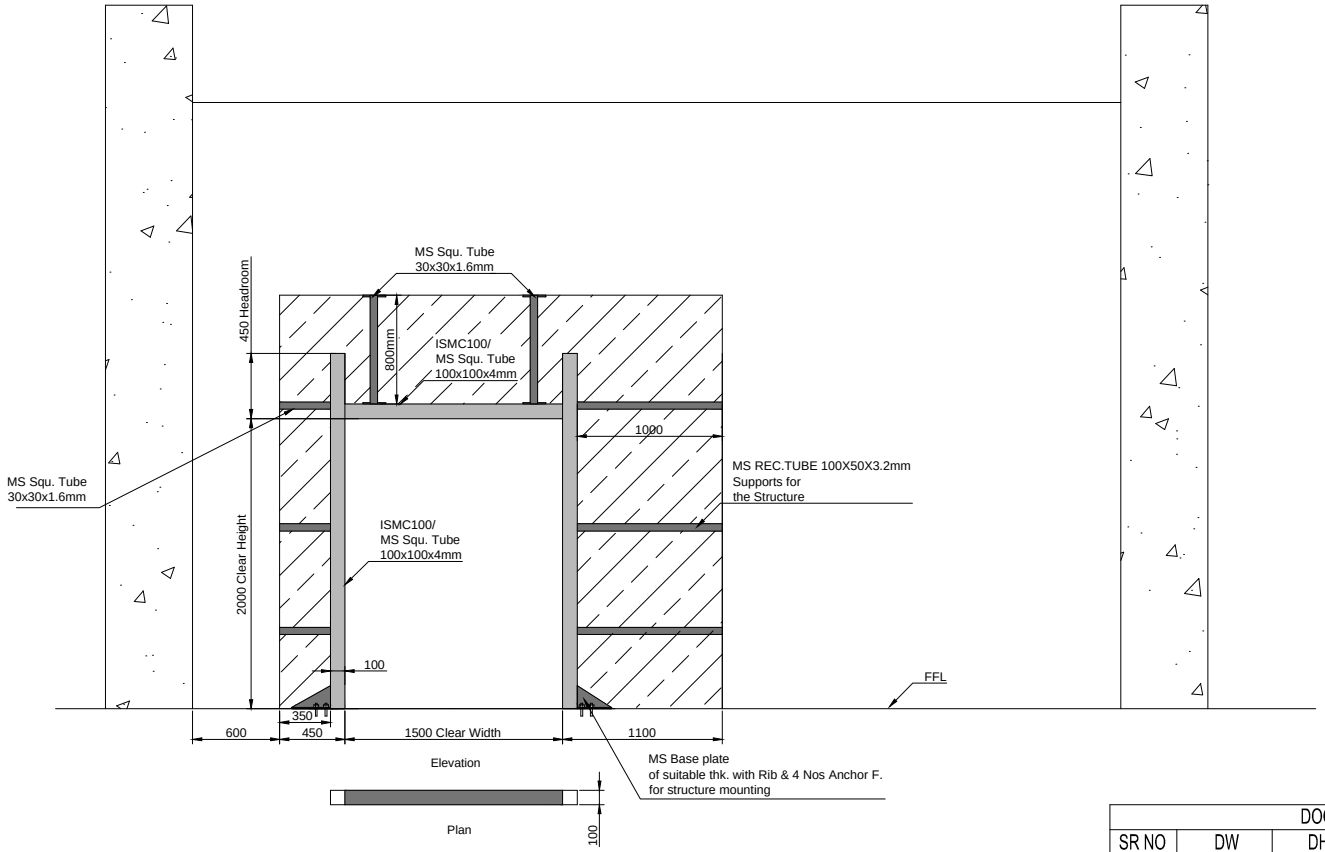

DOOR DIMENSION				
SR NO	DW	DH	MOTOR LOCATION	QUANTITY
1	1500	2000	RIGHT HAND SIDE	01

This drawing & designing is the property of NIHVA TECHNOLOGIES. Not to be sold or copied to any other concern.

TITLE: STRUCTURE FOR HSD HS9020G

NIHVA TECHNOLOGIES PVT. LTD.
NIHVA TECHNOLOGIES PVT. LTD. PUNE
Tel : 020 66304033
Email:- info@nihva.com
Website:- www.nihva.com

	NAME	SIGN	DATE
DRAWN	SURAJ		23/05/18
CHECK	PRADEEP		23/05/18
APPROVAL	PRADEEP		23/05/18

CLIENT - Fibro,India
PROJECT -
SITE - Chakan
If any queries contact : design@nihva.com
DWG. NO. : NIHVA/17-18/0037/01
REV- 01
ALL DIMENSION ARE IN mm
SCALE: NTS
WT:
SHEET: 01 OF 01

Note-
1. All Civil work will be in clients scope.

REV-
1. STRUCTURE MS TUBE SIZE CHANGED