


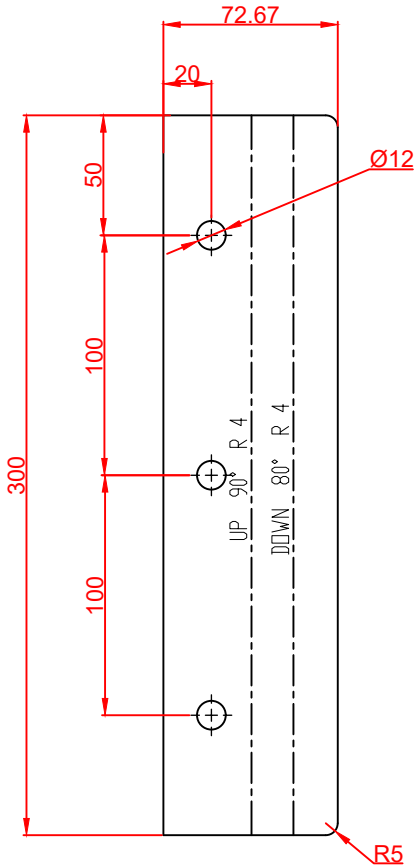


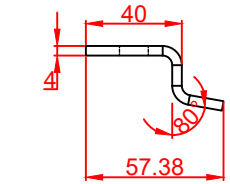

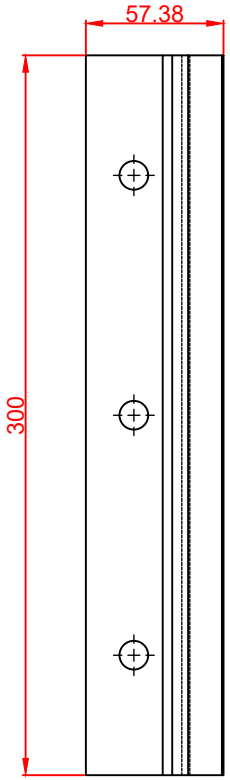

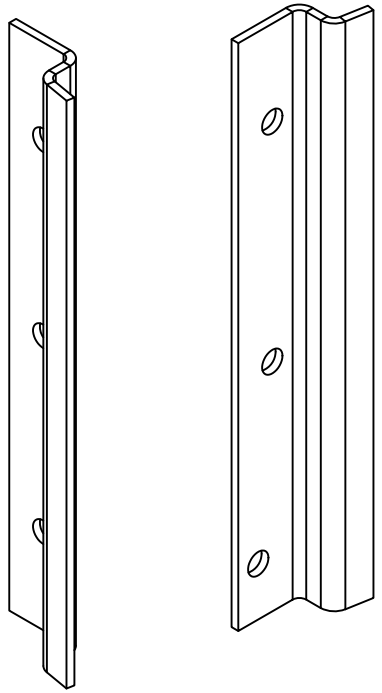

QTY. - 72 NOS.
INTERLOCK
BRACKET - Z TYPE
MTRL - MS

This drawing & design is the property of NIHVA TECHNOLOGIES. Not to be sold or copied to any other concern.

TITLE:- 3 LEAF CRM DOOR 04				NIHVA TECHNOLOGIES PVT. LTD. PUNE Tel : 020 66304033 Email:- info@nihva.com Website:- www.nihva.com
	NAME	DATE	SIGN	
DRAWN	M.SUTAR	03/05/2022		CLIENT - NIHVA TECHNOLOGIES PVT.LTD
CHECK	M.SUTAR	03/05/2022		LOCATION -
APPRD.				PRODUCT - SLIDING DOOR
If any queries contact : design@nihva.com				DWG NO:-NIHVA/22-23/VDR/0016 REV- 0
ALL DIMENSION ARE IN mm				SCALE: NTS SCALE:-- 1:1 SHEET: 01 OF 01

	Date	Revised By