




DETAIL C
SCALE 1 : 20

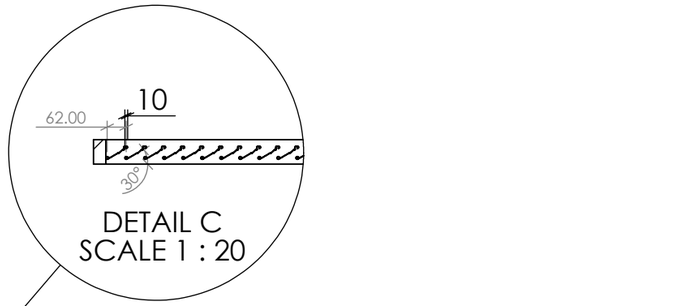

SECTION A-A
SCALE 1 : 40

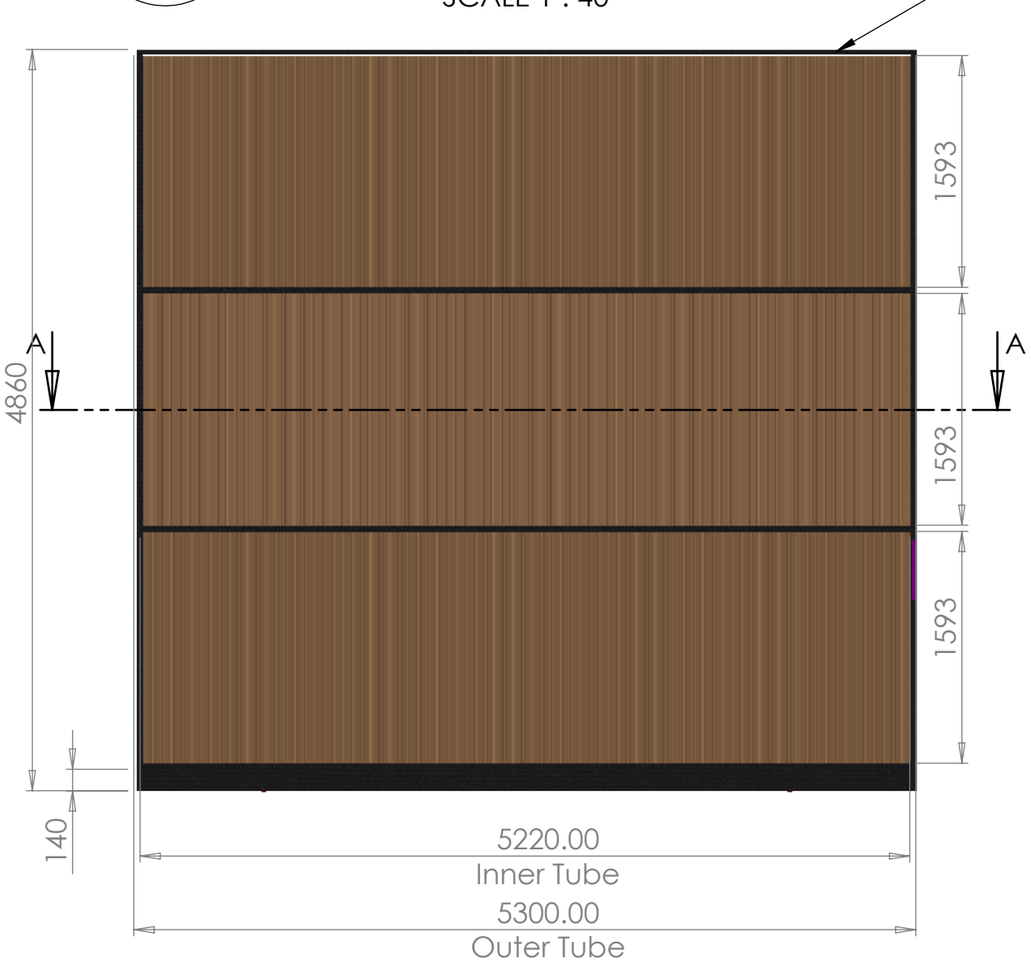



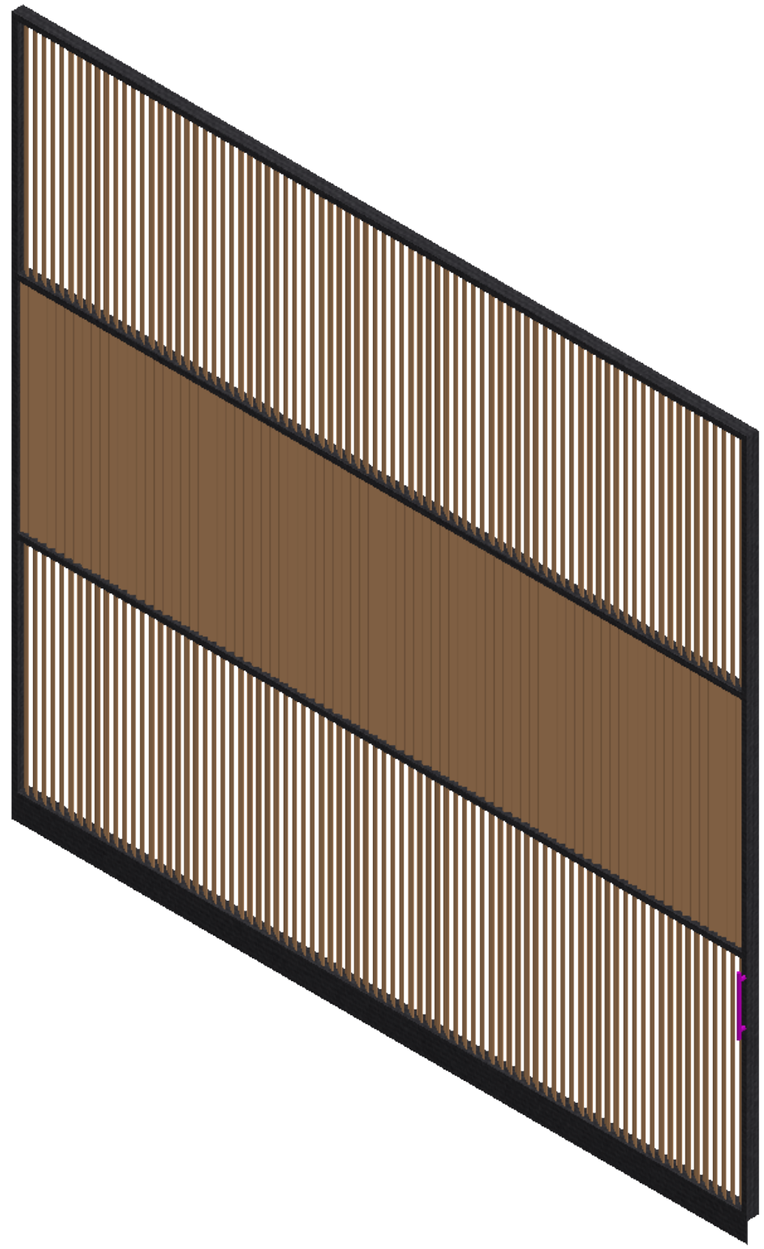

TITLE - Single leaf				NIHVA TECHNOLOGIES PVT.LTD.PUNE Website - www.nihva.com
	NAME	SIGNATURE	DATE	CLIENT - Panchshil Privilege
DRAWN	S.J		13.04.2024	PRODUCT - Manual Sliding Gate For DG Substance
CHK'D	A.K		13.04.2024	SITE LOCATION - Kharadi, Pune
APPV'D	V.T		13.04.2024	
if any queries contact - design1@nihva.com				DWG NO - NIHVA/24-25/00XX / REVISION -
ALL DIMENSION ARE IN mm			A3	SCALE - / SHEET 1 OF 1