

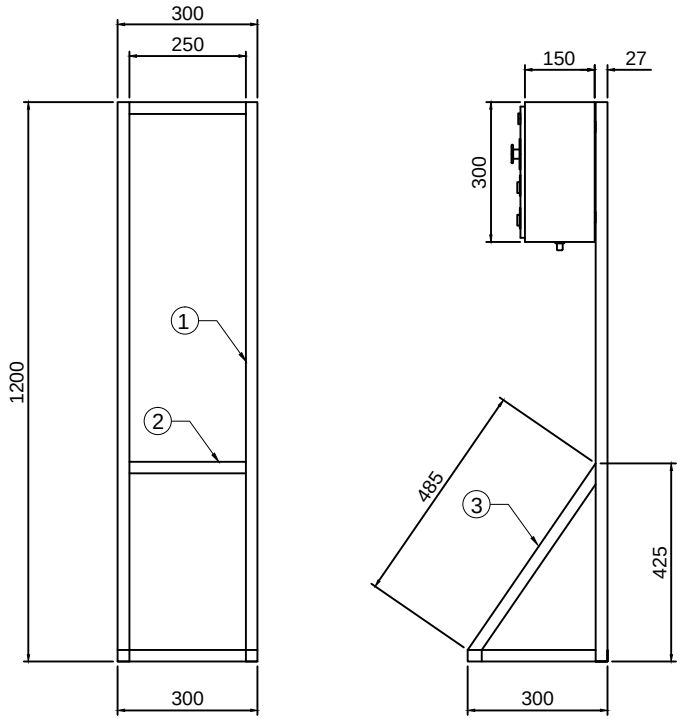


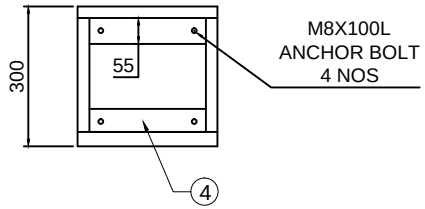

1. SQ. TUBE 25 X 25 X 2.6 X 1200L = 2 NOS
2. SQ. TUBE 25 X 25 X 2.6 X 250L = 6 NOS
3. SQ. TUBE 25 X 25 X 2.6 X 485L = 2 NOS
4. FLAT 50 X 5 X 250L = 2 NOS
5. ANCHOR BOLT M8 X 100L = 4 NOS

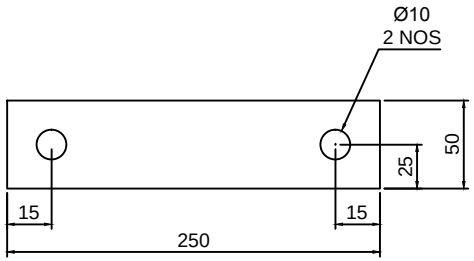

4

TOLERANCE - ±5mm

This drawing & design is the property of NIHVA TECHNOLOGIES. Not to be sold or copied to any other concern.

TITLE				
CONTROL PANEL & STAND				NIHVA TECHNOLOGIES PVT. LTD. PUNE Tel : 020 66304033 Email:- info@nihva.com Website:- www.nihva.com
	NAME	SIGN	DATE	
DRAWN	P.A		08.08.2020	CLIENT -
CHECK	G.J		08.08.2020	PROJECT -
APPRD.				SITE LOCATION -
If any queries contact : design@nihva.com				DWG. NO. : NIHVA/20-21/VDR/0035
ALL DIMENSION ARE IN mm				SCALE: NTS / WT: / REV- 0