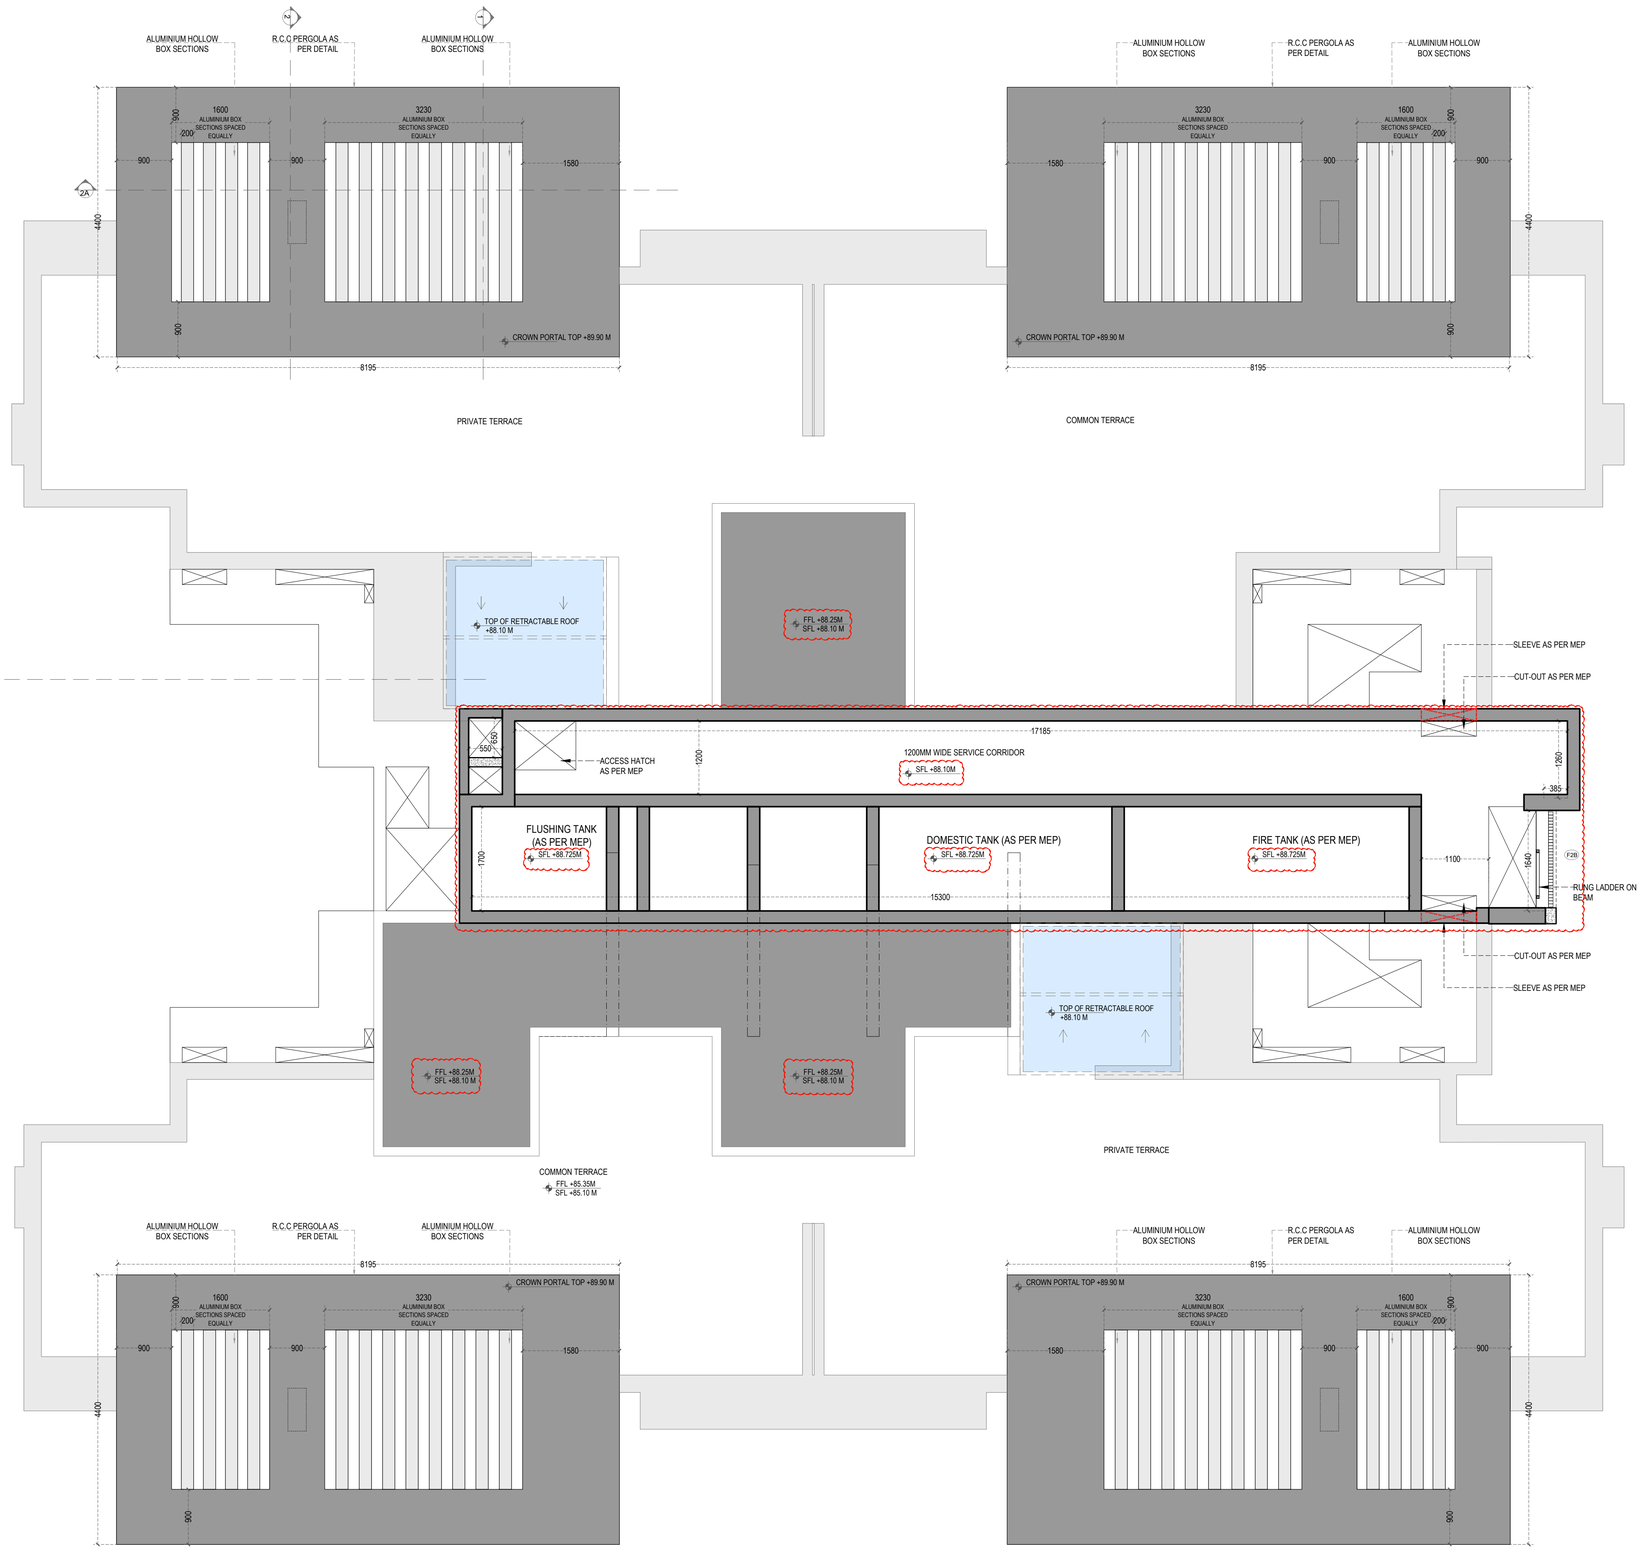


WALL & SUNK HATCH SCHEDULE

	R.C.C WALL & COLUMN
	200 MM NON STRUCTURAL WALL
	150 MM NON STRUCTURAL WALL
	200 MM BLOCK WORK
	100 MM BLOCK WORK
	150 MM LEDGE WALL IN BLOCKWORK
	100 MM LEDGE WALL IN BLOCKWORK
	METAL GRATING SERVICE SLAB
	RCC SERVICE SLAB

LEGEND - SUNK

SUNK DEPTH	HATCH
200 MM	
300 MM	
65 MM	
450 MM	

LEGEND - COLUMN REDUCTION LEVELS	
TYPE	HATCH
REDUCTION AT PLINTH BEAM BOTTOM LEVEL	
NOTCH IN BEAM	
LOCAL LINTEL/ RCC DROP PARDI	


LEGEND	
TYPE	HATCH
DRIP MOULD	
GROOVES AT BEAM BOTTOM	
VERTICAL GROOVES	
SLEEVES @ SLAB	
SLEEVES @ CEILING	

DOOR SCHEDULE (FOR TYPICAL FLOOR)

NO.	LOCATION	WIDTH (CIVIL OPENING)	LINTEL (FRM SFL)	CILL (FRM SFL)	DESCRIPTION
FD1B	STAIRCASE	1200	2100	-	SINGLE LEAF FIRE RATED WOODEN FLUSH DOOR (DETAIL AS PER VENDOR)
FD2	LOBBY	1100	2100	-	SINGLE LEAF FIRE RATED METAL DOOR (DETAIL AS PER VENDOR)
FD3	IBMS ROOM	1200	2100	200	SINGLE LEAF FIRE RATED METAL DOOR (DETAIL AS PER VENDOR)
DD1D	F.H.C/ ELE SHAFTS	1200X1675 (W X H)	2100	425	DOUBLE LEAF FIRE RATED METAL DOOR (DETAIL AS PER VENDOR)
DD1E	ELV SHAFT	1100X1675 (W X H)	2100	425	DOUBLE LEAF FIRE RATED METAL DOOR (DETAIL AS PER VENDOR)
DD1F	PLB SHAFT	600 X1675 (W X H)	2100	425	SINGLE LEAF FIRE RATED METAL DOOR (DETAIL AS PER VENDOR)
DD2B	STAIRCASE ELE SHAFT	1450 X1675 (W X H)	2100	425	DOUBLE LEAF FIRE RATED METAL DOOR (DETAIL AS PER VENDOR)
D5	PRIVATE TERRACE	-	-	-	SINGLE LEAF DOOR (DETAIL AS PER VENDOR)

WINDOW SCHEDULE

NO.	LOCATION	CIVIL OPENING (W X H)	LINTEL (FRM SFL)	CILL (FRM SFL)	DESCRIPTION
LW1B	LOBBY WINDOW	1000 X 900	2100	1200	DOUBLE LEAF OPENABLE GLASS PANEL WINDOW WITH FRICTION HINGE
LW5	STAIRCASE WINDOW	850 X1200	2550 (FROM ML)	1350 (FROM ML)	SINGLE LEAF OPENABLE GLASS PANEL WINDOW WITH FRICTION HINGE

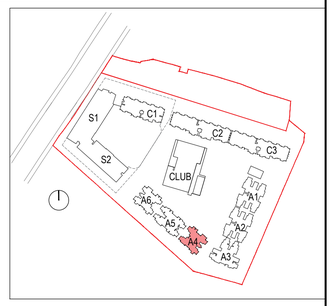

GENERAL NOTES

1 : All dimensions are in millimeters and levels in meters unless specified otherwise.
2 : Do not scale the drawing; follow written dimensions.
3 : All dimensions are unfinished dimensions unless specified otherwise.
4 : Any discrepancies should be brought to the notice of the Architect prior to execution of job / procuring materials at site.
5 : This drawing is the property of Kapadia Associates and should not be reproduced, copied, handed over to a third party or used for any purpose other than for which it has been issued.
6 : This drawing is to be read in conjunction with all relevant structural & services drawings.

NOTE:
1. PLEASE READ IN CONJUNCTION WITH KITCHEN DETAIL,TOILET DETAIL, FIN DETAIL & RAILING DETAIL, STAIRCASE DETAILS.
2. 10MM ADDITIONAL COVER HAS BEEN INCLUDED IN THE SHEAR WALL THICKNESS, WHEREVER REQUIRED FOR GROOVE.
3. HIGHLIGHTED AREAS ARE UNDER DISCUSSION

REVISION INDEX

REV. NO.	DATE	REMARKS
R00	29-04-2026	VFC ISSUED

CLIENT
LODHA GROUP

PROJECT TITLE
LODHA RISERVO - A4
VIKHROLI,MUMBAI

DRAWING TITLE & NO.
AR-KA-A4-209-OHT LEVEL PLAN

DRAWING STAGE
WORKING DRAWING

SCALE	REV. NO.	REV. DATE
1:50	R00	29-04-2026

STAMP & SIGNATURE

Digitally signed by: SUPRIYA UKIDAVE
Date: 2026.04.29 19:53:13 +06'30'

KAPADIA ASSOCIATES
architecture • urban design
112-114, Peninsula Centre,Dr. S.S. Rao Road,Parel East, Mumbai 400012
Tel : 91-22-6660 2838 / 39 E-mail : kapl@kapl.in Website : www.kapl.in