

Revision		Date	By
A	Measure for hoist, BOM and ballons added, TH 11907 (was 11872).	2022-01-18	MA
B	Costumer steel added. Layout adjusted.	2022-03-01	FV
C	Text changed at detail 1	2022-03-14	MA

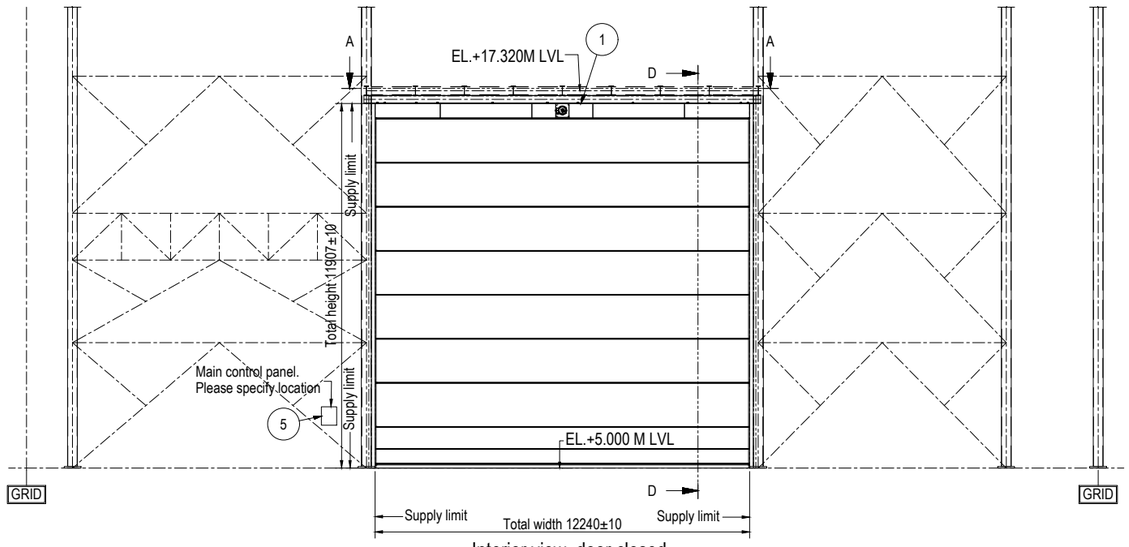


Interior view, door closed

ELEVATION VIEW - EAST SIDE MEGA DOOR ARRANGEMENT


(SCALE 1:100)

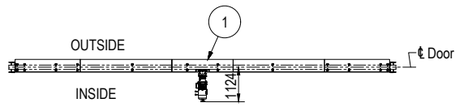


SECTION A-A

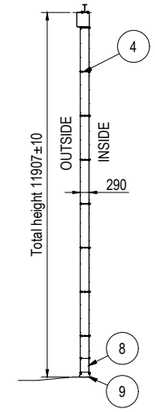

SECTION D-D

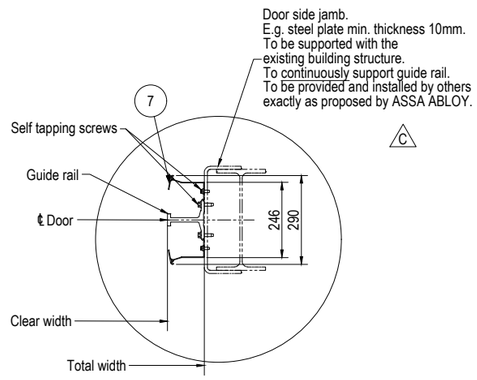


Detail 1 (1 :10)

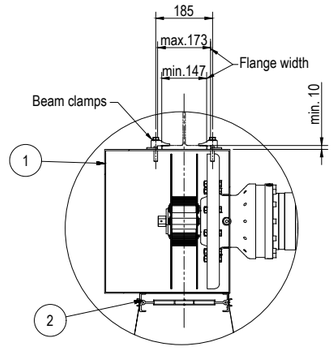

Detail 2 (1 :10)


Door head steel.
To be supported with the
existing building structure.
Designed, provided and installed by
others than ASSA ABLOY.

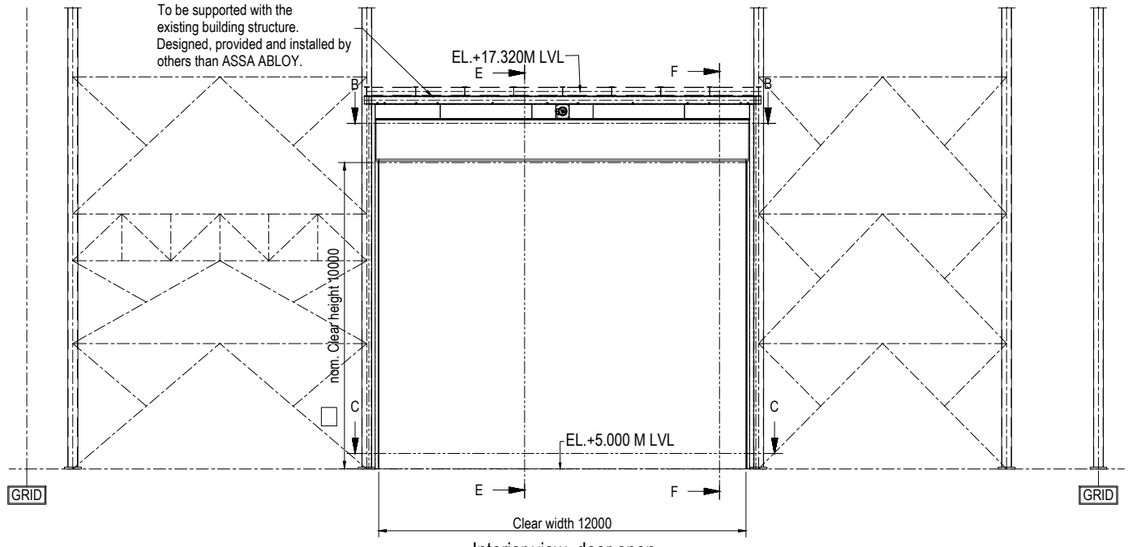


Interior view, door open

ELEVATION VIEW - EAST SIDE MEGA DOOR ARRANGEMENT

(SCALE 1:100)

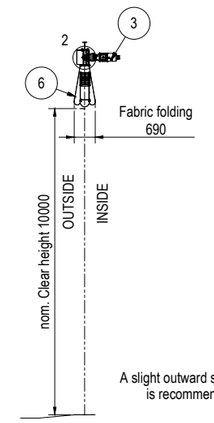


SECTION E-E

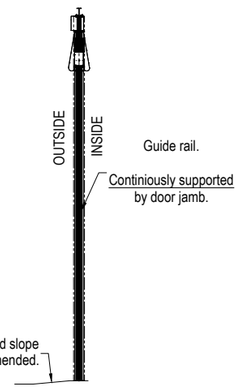

SECTION F-F



SECTION B-B

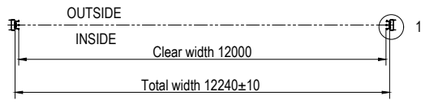

SECTION C-C

ITEM	QTY	DESCRIPTION	MATERIAL
9	1	Bottom seal	EPDM
8	1	Bottom beam	S355
7	2	Guide rail	6005-T6
6	1	Door fabric	PVC
5	1	Main control panel	
4	7	Intermediate beam	6005-T6
3	1	Hoist	
2	1	Top beam	6005-T6
1	1	Header box	S355

DOOR IDENTITY NUMBER: 84705001-004

LOAD DIAGRAM & NOTES, ref. to drwng. no. 74451

DESIGNED: MA		SIZE: A1	SCALE: 1:100
CODE: 84705 (ITEM NO)		If not otherwise stated: Tolerances ISO 2768-m EN ISO 13920-B	
DATE: 2021-10-11		Cutting class ISO 9013-442	
ASSA ABLOY		Weld class ISO 5817-C	
		Surface finish Smooth raw surface	

Seabird Karwar

India

Megadoor 12000 x10000

Interface drawing

DRAWING NO: 74450

REVISION: C

PLOT DATE

This document is the property of ASSA ABLOY Entrance Systems AB and shall not be reproduced or disclosed to a third party or used for any other unauthorized purpose.