
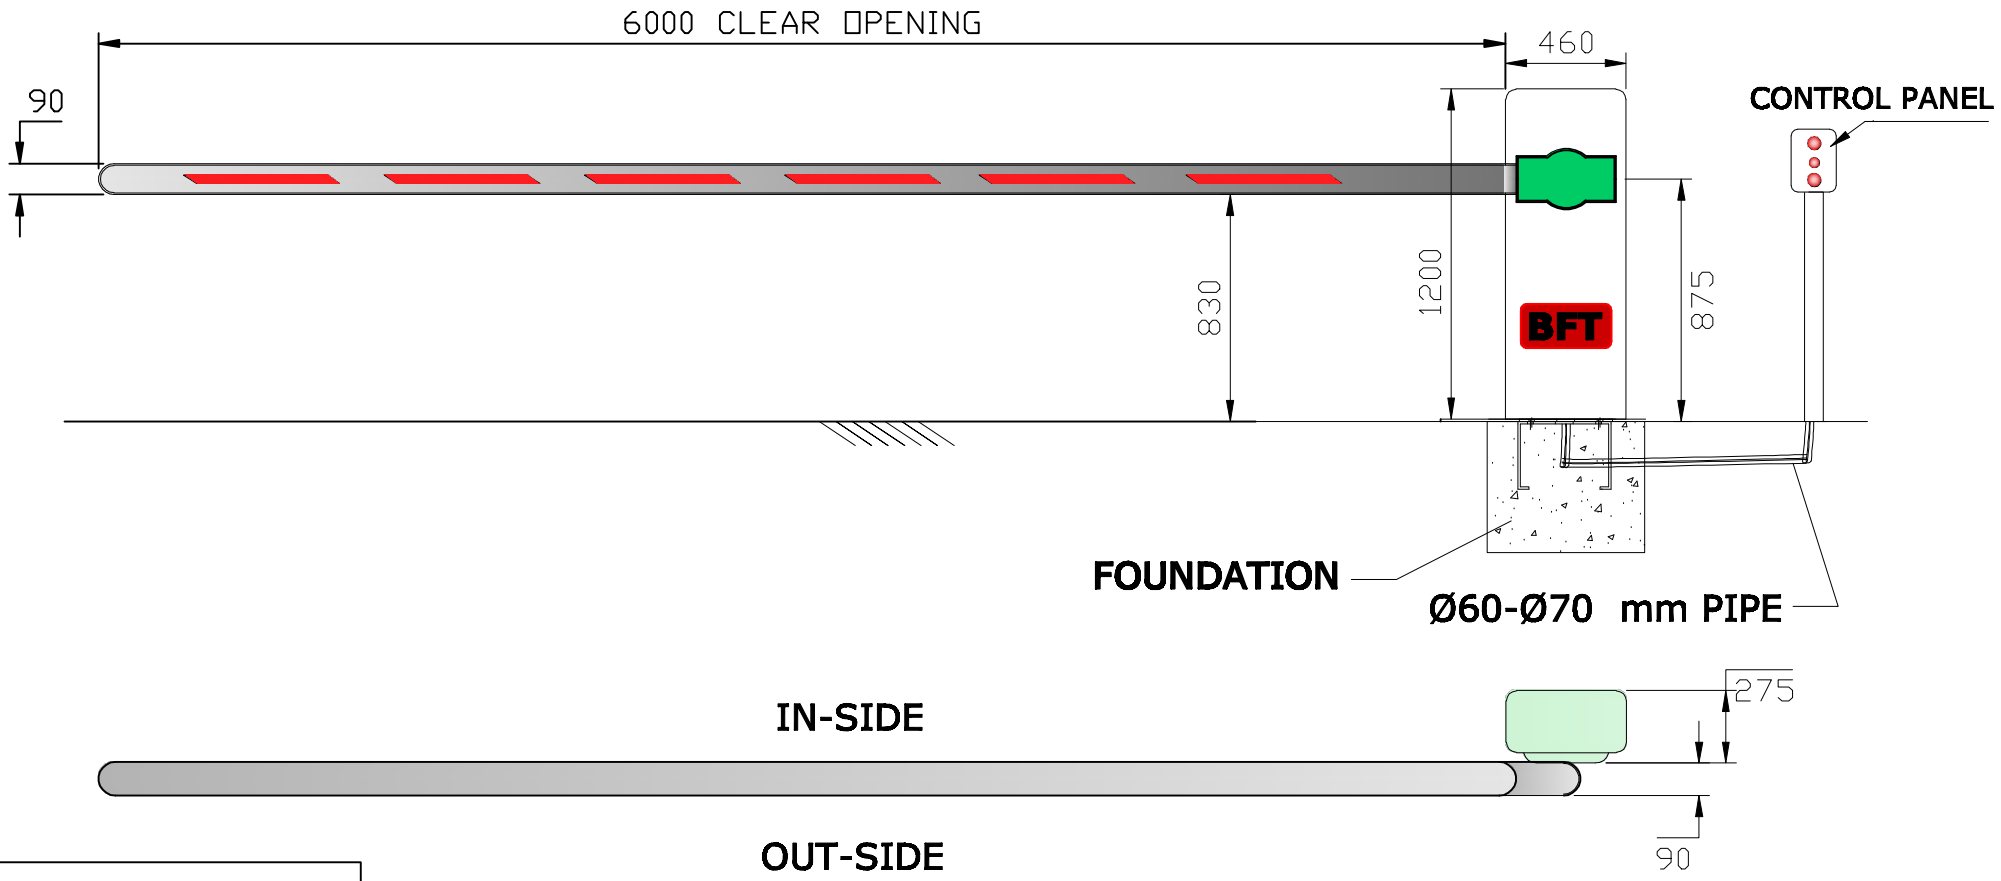


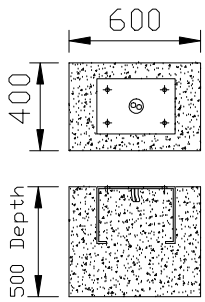

FOUNDATION DETAILS

This drawing & designing is the property of NIHVA TECHNOLOGIES. Not be sold or copy to any other concern.

TITLE

BOOM BARRIER FOUNDATION DETAILS

CLIENT APPROVAL

NIHVA TECHNOLOGIES PVT. LTD.

NIHVA TECHNOLOGY PVT. LTD. PUNE
Tel : 020 66304033
Email:- info@nihva.com
Website:- www.nihva.com

	SIGN	DATE	
DRAWN	ABHIJIT	30/03/15	CLIENT -INDOSPACE
CHECK	ANIL	30/03/15	PROJECT-ERICSON
MFG			SITE -CHAKAN
Ref. No.			DWG. NO. -NIHVA/15-16/020
ALL DIMENSION ARE IN mm			SCALE:01 | WT: | SHEET:01
			If any queries contact : projects@nihva.com