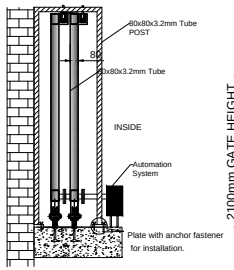

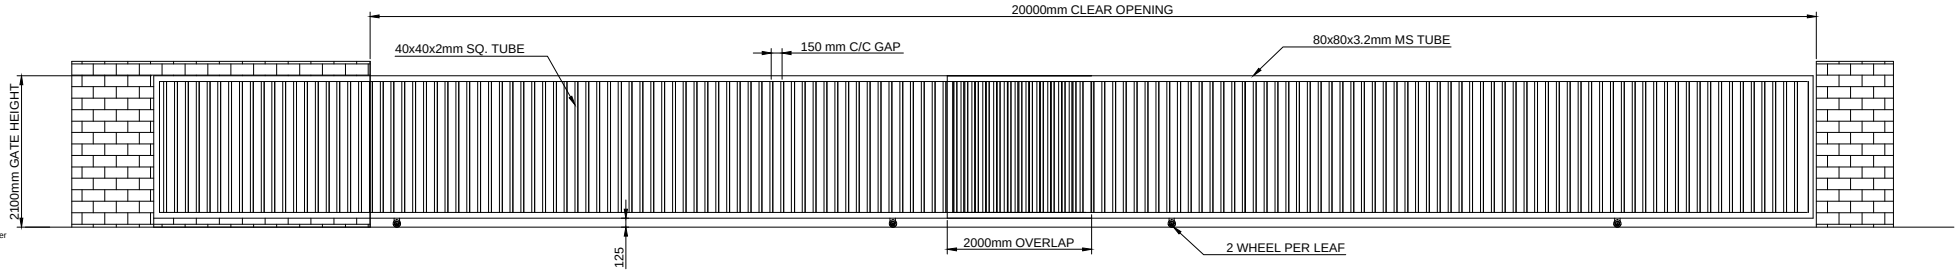

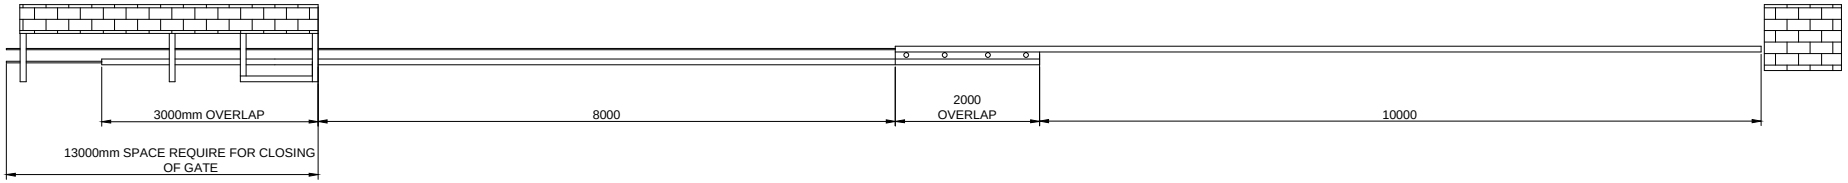

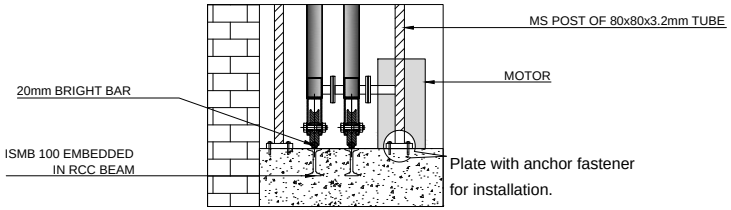

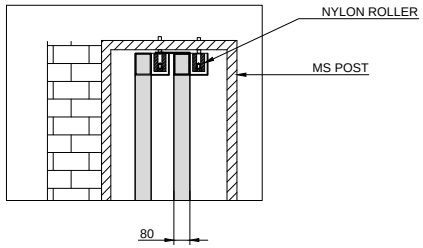

Clear Opening size -8000mm x 1850mm
& Wicket gate opening size-1000x1400mm

NOTE :- *ALL REQ. CIVIL WORK WILL BE IN CLIENT SCOPE.

This drawing & designing is the property of NIHVA TECHNOLOGIES. Not be sold or copy to any other concern.

TITLE
DOUBLE LEAF TELESCOPIC SLIDING GATE

NIHVA TECHNOLOGIES PVT. LTD.
NIHVA TECHNOLOGY PVT. LTD. PUNE
Tel : 020 66304033
Email:- info@nihva.com
Website:- www.nihva.com

	SIGN	DATE	
DRAWN	OMKAR	13/08/16	CLIENT - VIEGA INDIA
CHECK	ANIL	13/08/16	PROJECT -
REV.	01		SITE -
APPROVAL			DWG. NO. : NIHVA/16-17/0054
If any queries contact : projects@nihva.com			SCALE: NTS / WT: / SHEET: 01 OF 01
ALL DIMENSION ARE IN mm			