
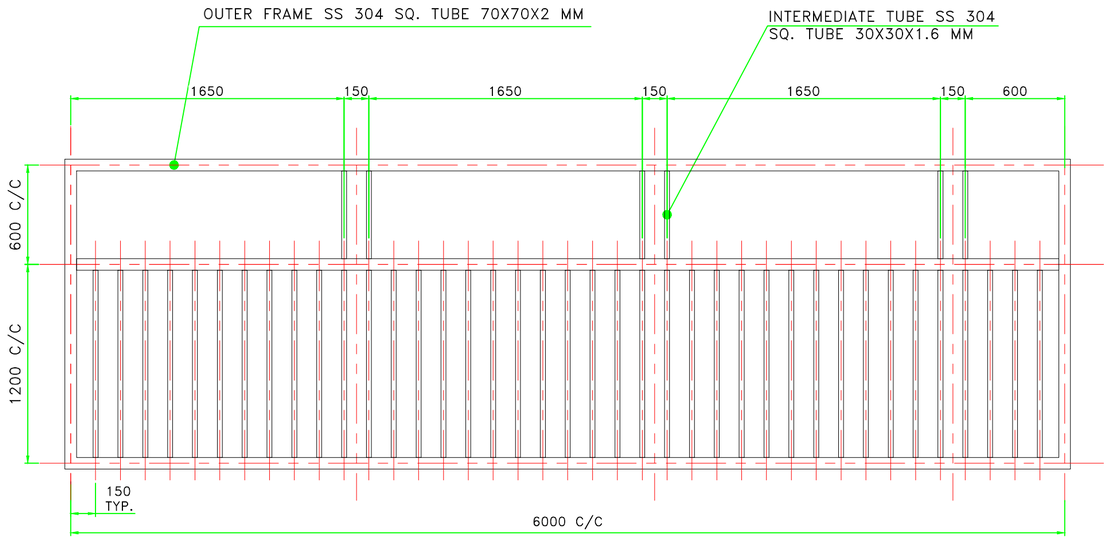



SUPPORTING COLUMN WITH NYLON ROLLERS–SS 304 SQ. TUBE 70X70X2 MM

6 METER WIDE SLIDING GATE DETAILS

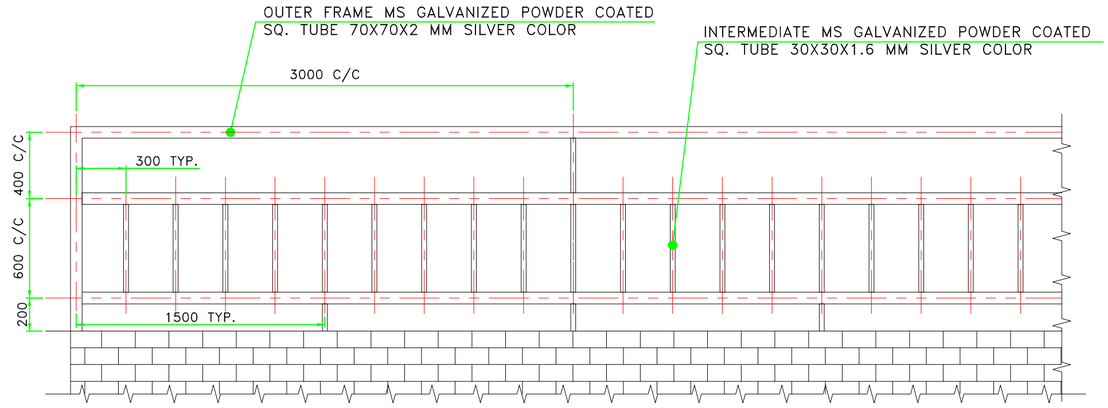

TYP. DETAIL FIXED GRILL DETAILS

PLEASE QUOTE SEPARATE DETAILS/ PRICE FOR FIXED GRILL CONSIDERING MATERIAL SS 304

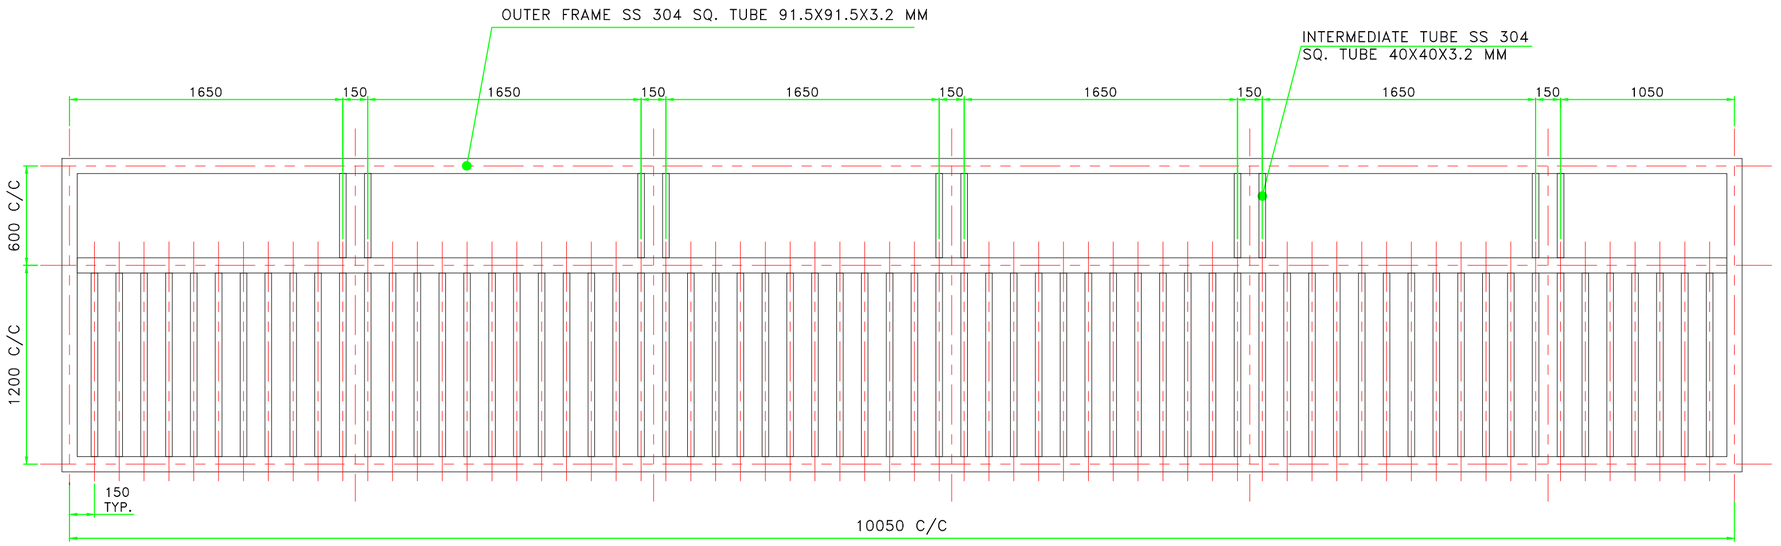

SUPPORTING COLUMN WITH NYLON ROLLERS–SS 304 SQ. TUBE 91.5X91.5X3.2 MM

10 METER WIDE SLIDING GATE DETAILS

NOTE:–
ABOVE ALL DIMENSIONS MAY CHANGE SLIGHTLY DURING DETAIL ENGINEERING.

REV. NO.	DATE	DESCRIPTION	BY	APPROVED

REVISIONS

DO NOT SCALE IF IN DOUBT PLEASE ASK

THIS DRAWING IS THE PROPERTY OF ESPIC CONSULTING PRIVATE LIMITED. THIS MUST NOT BE COPIED OR REPRODUCED IN ANY MANNER OR DESIGN DISCLOSED OR PARTS MANUFACTURED THERE OF WITHOUT WRITTEN PERMISSION OF ESPIC CONSULTING PVT.LTD.

ESPIC
Engineering Solutions For Projects & Industrial Constructions

Espic Consulting Private Limited
3rd FLOOR, SAPPHIRE TWINS–RIGHT WING,
PU–3, SCHEME NO.54, AB ROAD, INDORE–452010 INDIA.

TITLE
ENTRANCE GATE & FENCE DETAILS

CLIENT	JSW MI STEEL SERVICE CENTER PVT. LTD. KHED CITY DIST.–PUNE (M.S.)	PROJECT	SERVICE CENTER
DRAWN BY	GIRISH	CHECKED BY	V.K.Jain
APPROVED BY	D.K. JAIN	DATE	14–10–14
SCALE	1:58	DRG NO.	323–A–020
SHEET	2 OF 2	SIZE	A1
REV.	0		