

ISSUED FOR EXECUTION

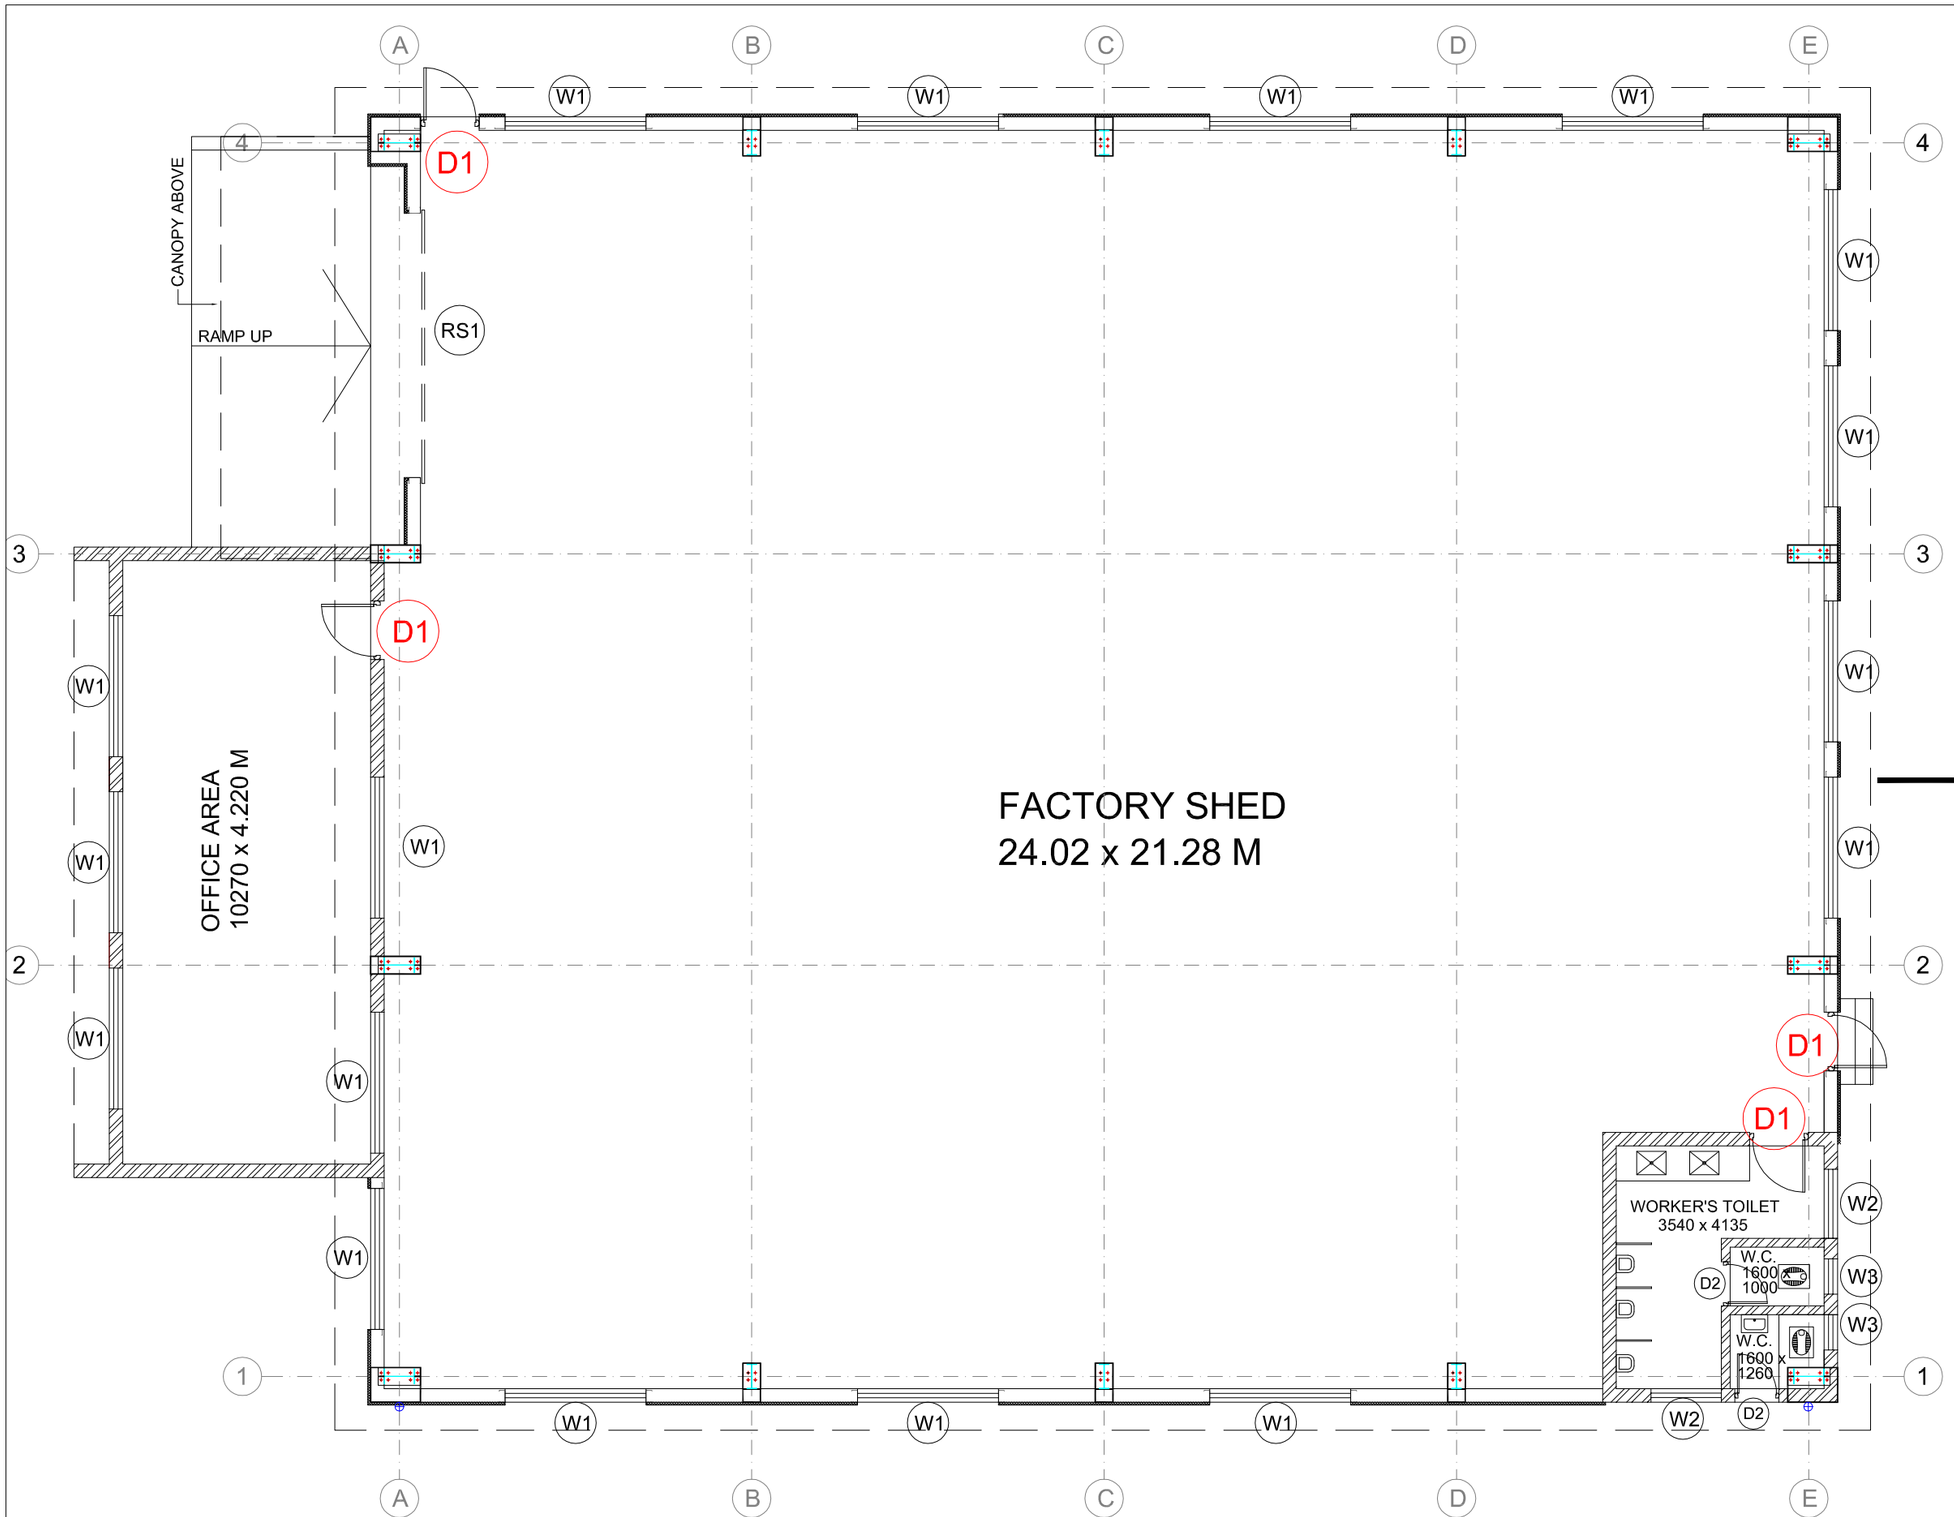

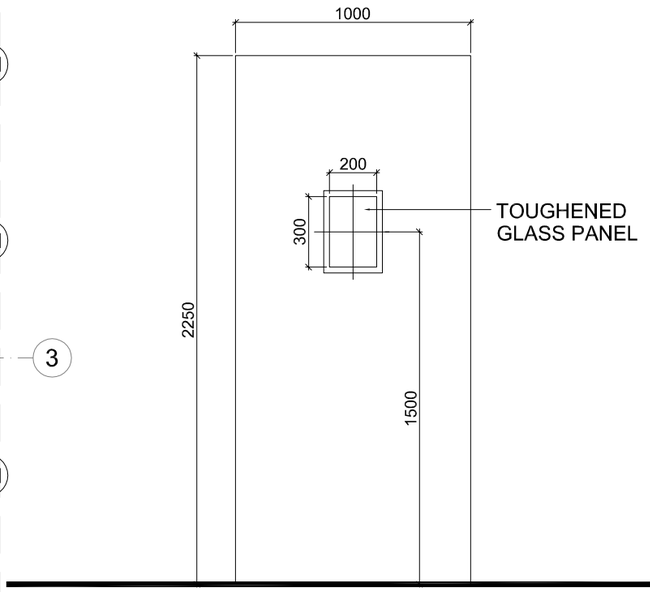

D1 = 1000 x 2250 MM
QTY. = 4 NOS.

DESCRIPTION

DOOR DETAIL

PROJECT

PROPOSED FACTORY AND OFFICE BUILDING FOR ECOMAX ON PLOT NO. F-30, MIDC RANJANGAON, TAL. SHIRUR, DIST. PUNE.

GENERAL NOTES

* ALL DIMENSIONS ARE IN MM.
* FOLLOW WRITTEN DIMENSION.
* DO NOT SCALE THE DRAWING.
* ALL WALLS ARE 230 MM THK. EXCEPT MENTIONED OTHERWISE.

SCHEDULE OF DOORS.

S.NO.	MARK	WALL OPENING WIDTH X HEIGHT	REMARKS

SCHEDULE OF WINDOWS.

S.NO.	MARK	WALL OPENING WIDTH X HEIGHT	REMARKS

S.NO.	DATE	REMARK	S.NO.	DATE	REMARK
1.	22 / 11 / 2016	R0			

DATE : NOVEMBER 22, 2016

SCALE : N.T.S.

DRAWN BY :

NORTH

DRAWING NO.

siddharth durve
architect

F6/17, SAKAL NAGAR,
BANER ROAD,
PUNE - 411007
PH. NO. - 9890895908