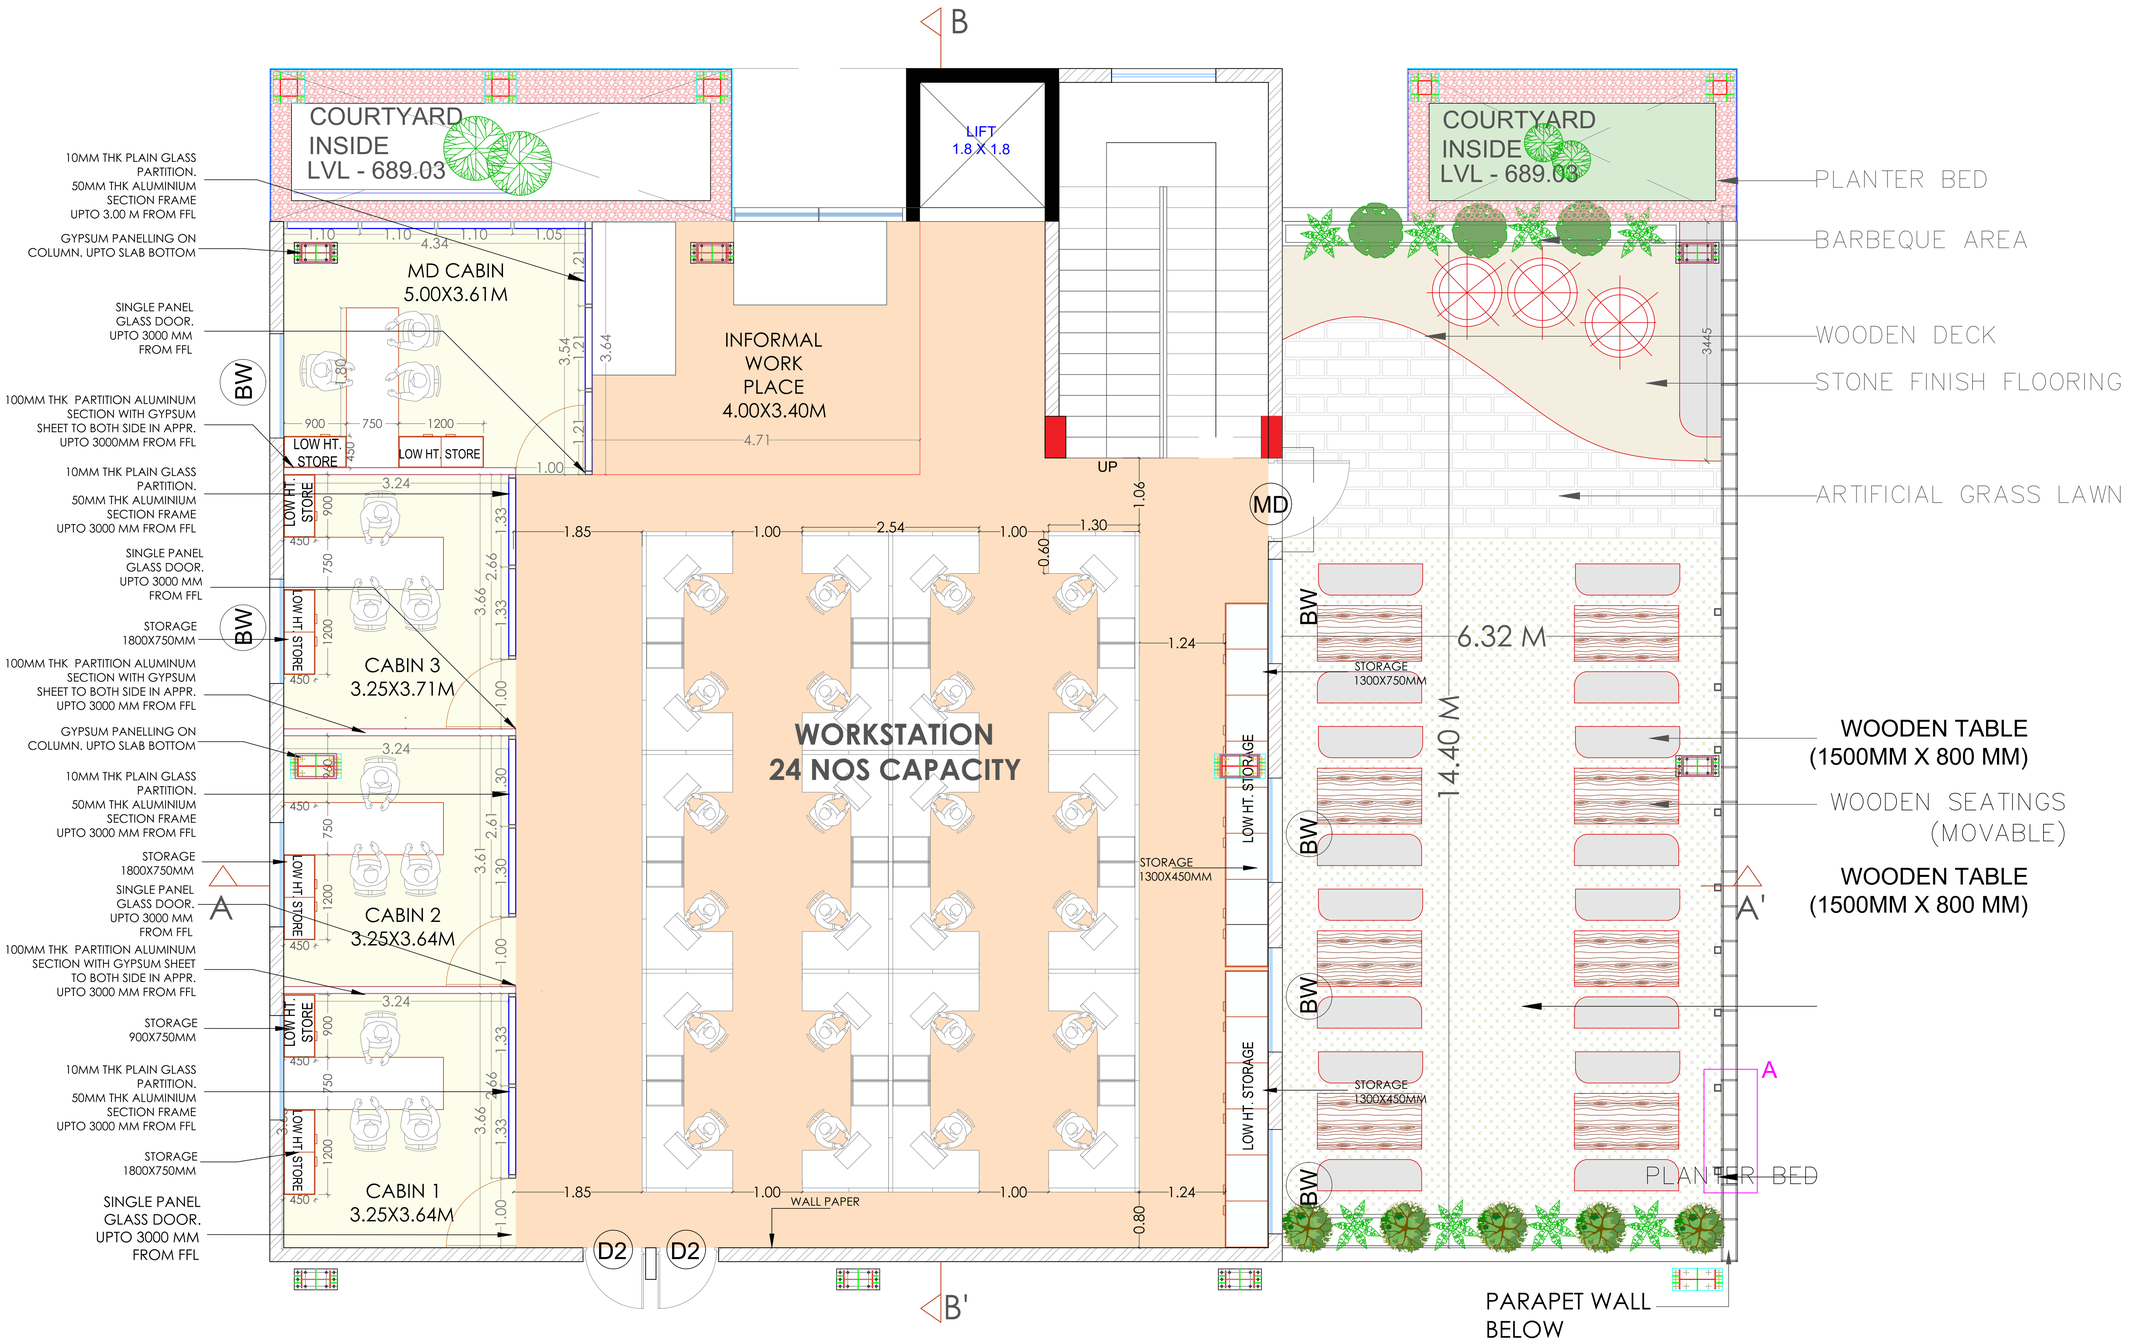


OFFICE AND CANTEEN FIRST FLOOR PLAN

SHEET NO - 07

REVISION NO.

NO.	DATE	DESCRIPTION

*** NOTES:
1. PLEASE DO NOT SCALE THE DRAWING. FOLLOW WRITTEN DIMENSIONS.
2. ALL DIMENSIONS GIVEN ARE IN METERS.
3. IN CASE OF CONTROVERSIES CONTACT THE ARCHITECT IMMEDIATELY.
4. FOR STRUCTURAL DETAILS PLEASE REFER R.C.C. DWG
5. DO NOT REFER PREVIOUS DWG
6. REFER STRUCTURAL DRAWING ALONG WITH THIS DRAWING.

SIGN / SEAL -

PRASHANT DESHMUKH & ASSOCIATES
ARCHITECTURAL & ENGINEERING CONSULTANTS

FIRST FLOOR PLAN

PRASHANT DESHMUKH AND ASSOCIATES
ARCHITECTURAL & ENGINEERING CONSULTANTS
1/62-B, PADMADARSHAN SOC.,
PUNE - SATARA ROAD, PUNE - 411 009.
TELEFAX :- 2422 78 96 32907142 24218714

CLIENT	BURKERT FLUID CONTROL SYSTEM			
PROJECT	BURKERT FLUID CONTROL SYSTEM , MINDEWADI			
SCALE	DATE	DRAWN BY	DEALT BY	REV
NTS	27.06.2024	SHIVOUNSH	OMKAR	
CHK BY	PRATIK D			