

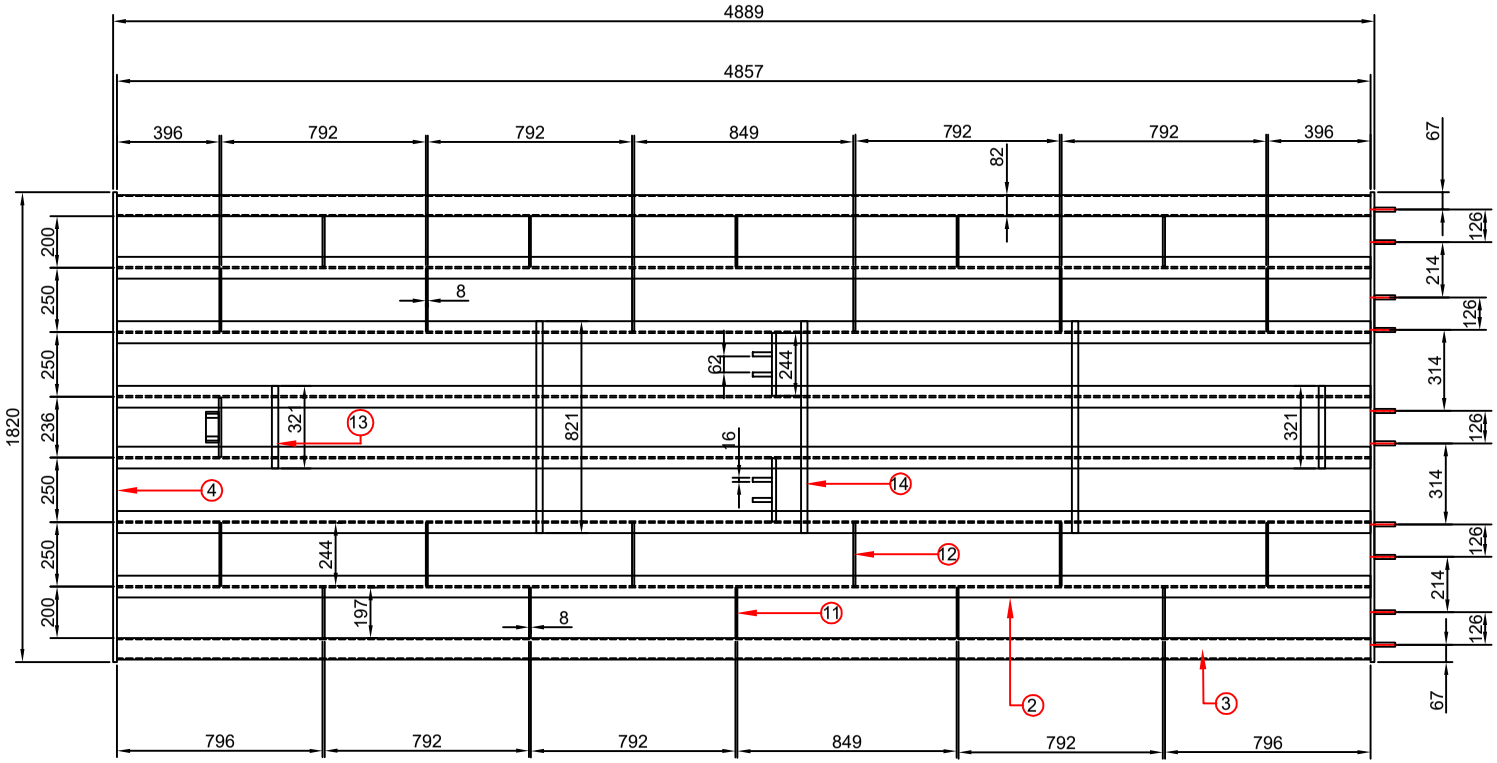


BOM			
SL NO.	DESCRIPTION	SPECIFICATION	QTY
1	CHEQ.SHEET	1820X5000X8THK	1NO
2	ISMB	175X85X4857L	6NOS
3	RECT. TUBE	145X82X4857LX4.8THK	2NOS
4	MS FLAT	175X16X1820L	2NOS
5	MS FLAT	50X16X115L	2NOS
6	MS FLAT	50X5X120L	1NO
7	MS FLAT	50X10X230L	1NO
8	PROFILE	75X16X75L	4NOS
9	MS FLAT	100X16X244L	2NOS
10	PROFILE	80X16X100L	10NOS
11	MS FLAT	145X8X197L	10NOS
12	MS FLAT	150X8X244L	12NOS
13	RECT.TUBE	50X25X321LX3THK	2NOS
14	RECT.TUBE	50X25X821LX3THK	3NOS
15	PROFILE	50X16X75L	3NOS
16	L BEND		
17	SIDE COVER		

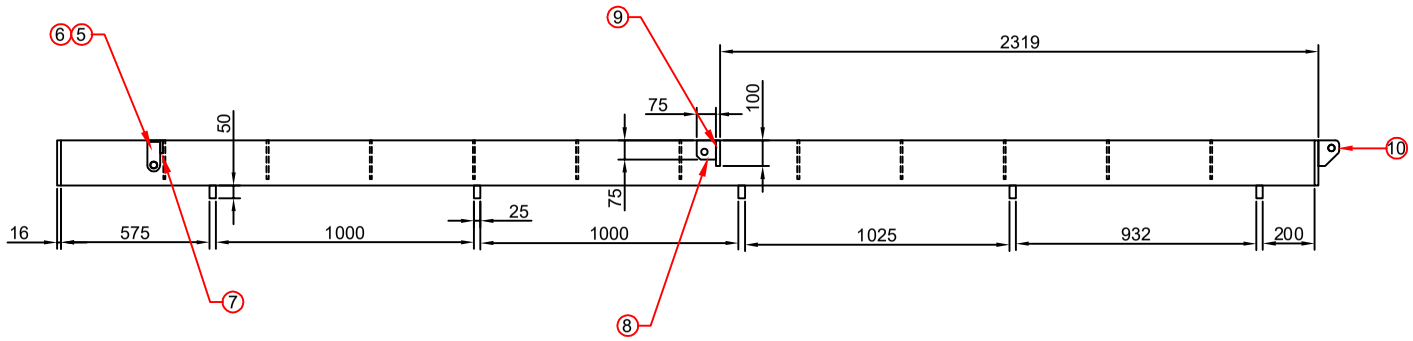

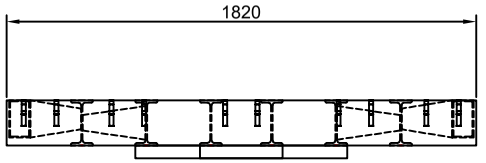

This drawing & design is the property of NIHVA TECHNOLOGIES. Not to be sold or copied to any other concern.

TITLE:- DECK ASSEMBLY

NIHVA TECHNOLOGIES PVT. LTD.

NIHVA TECHNOLOGIES PVT. LTD. PUNE
Tel : 020 66304033
Email:- info@nihva.com
Website:- www.nihva.com

	NAME	DATE	SIGN
DRAWN	SUJATA	20/11/2021	
CHECK	G.PATIL	20/11/2021	
APPRD.	A.K	20/11/2021	

If any queries contact : design@nihva.com

ALL DIMENSION ARE IN mm

CLIENT -

LOCATION -

PRODUCT -

DWG NO:-NIHVA/21-22/MFG/003 REV- 0

SCALE: NTS SCALE:-- 1:1 SHEET: 01 OF 01

Rev No.	Revision	Date	Revised By