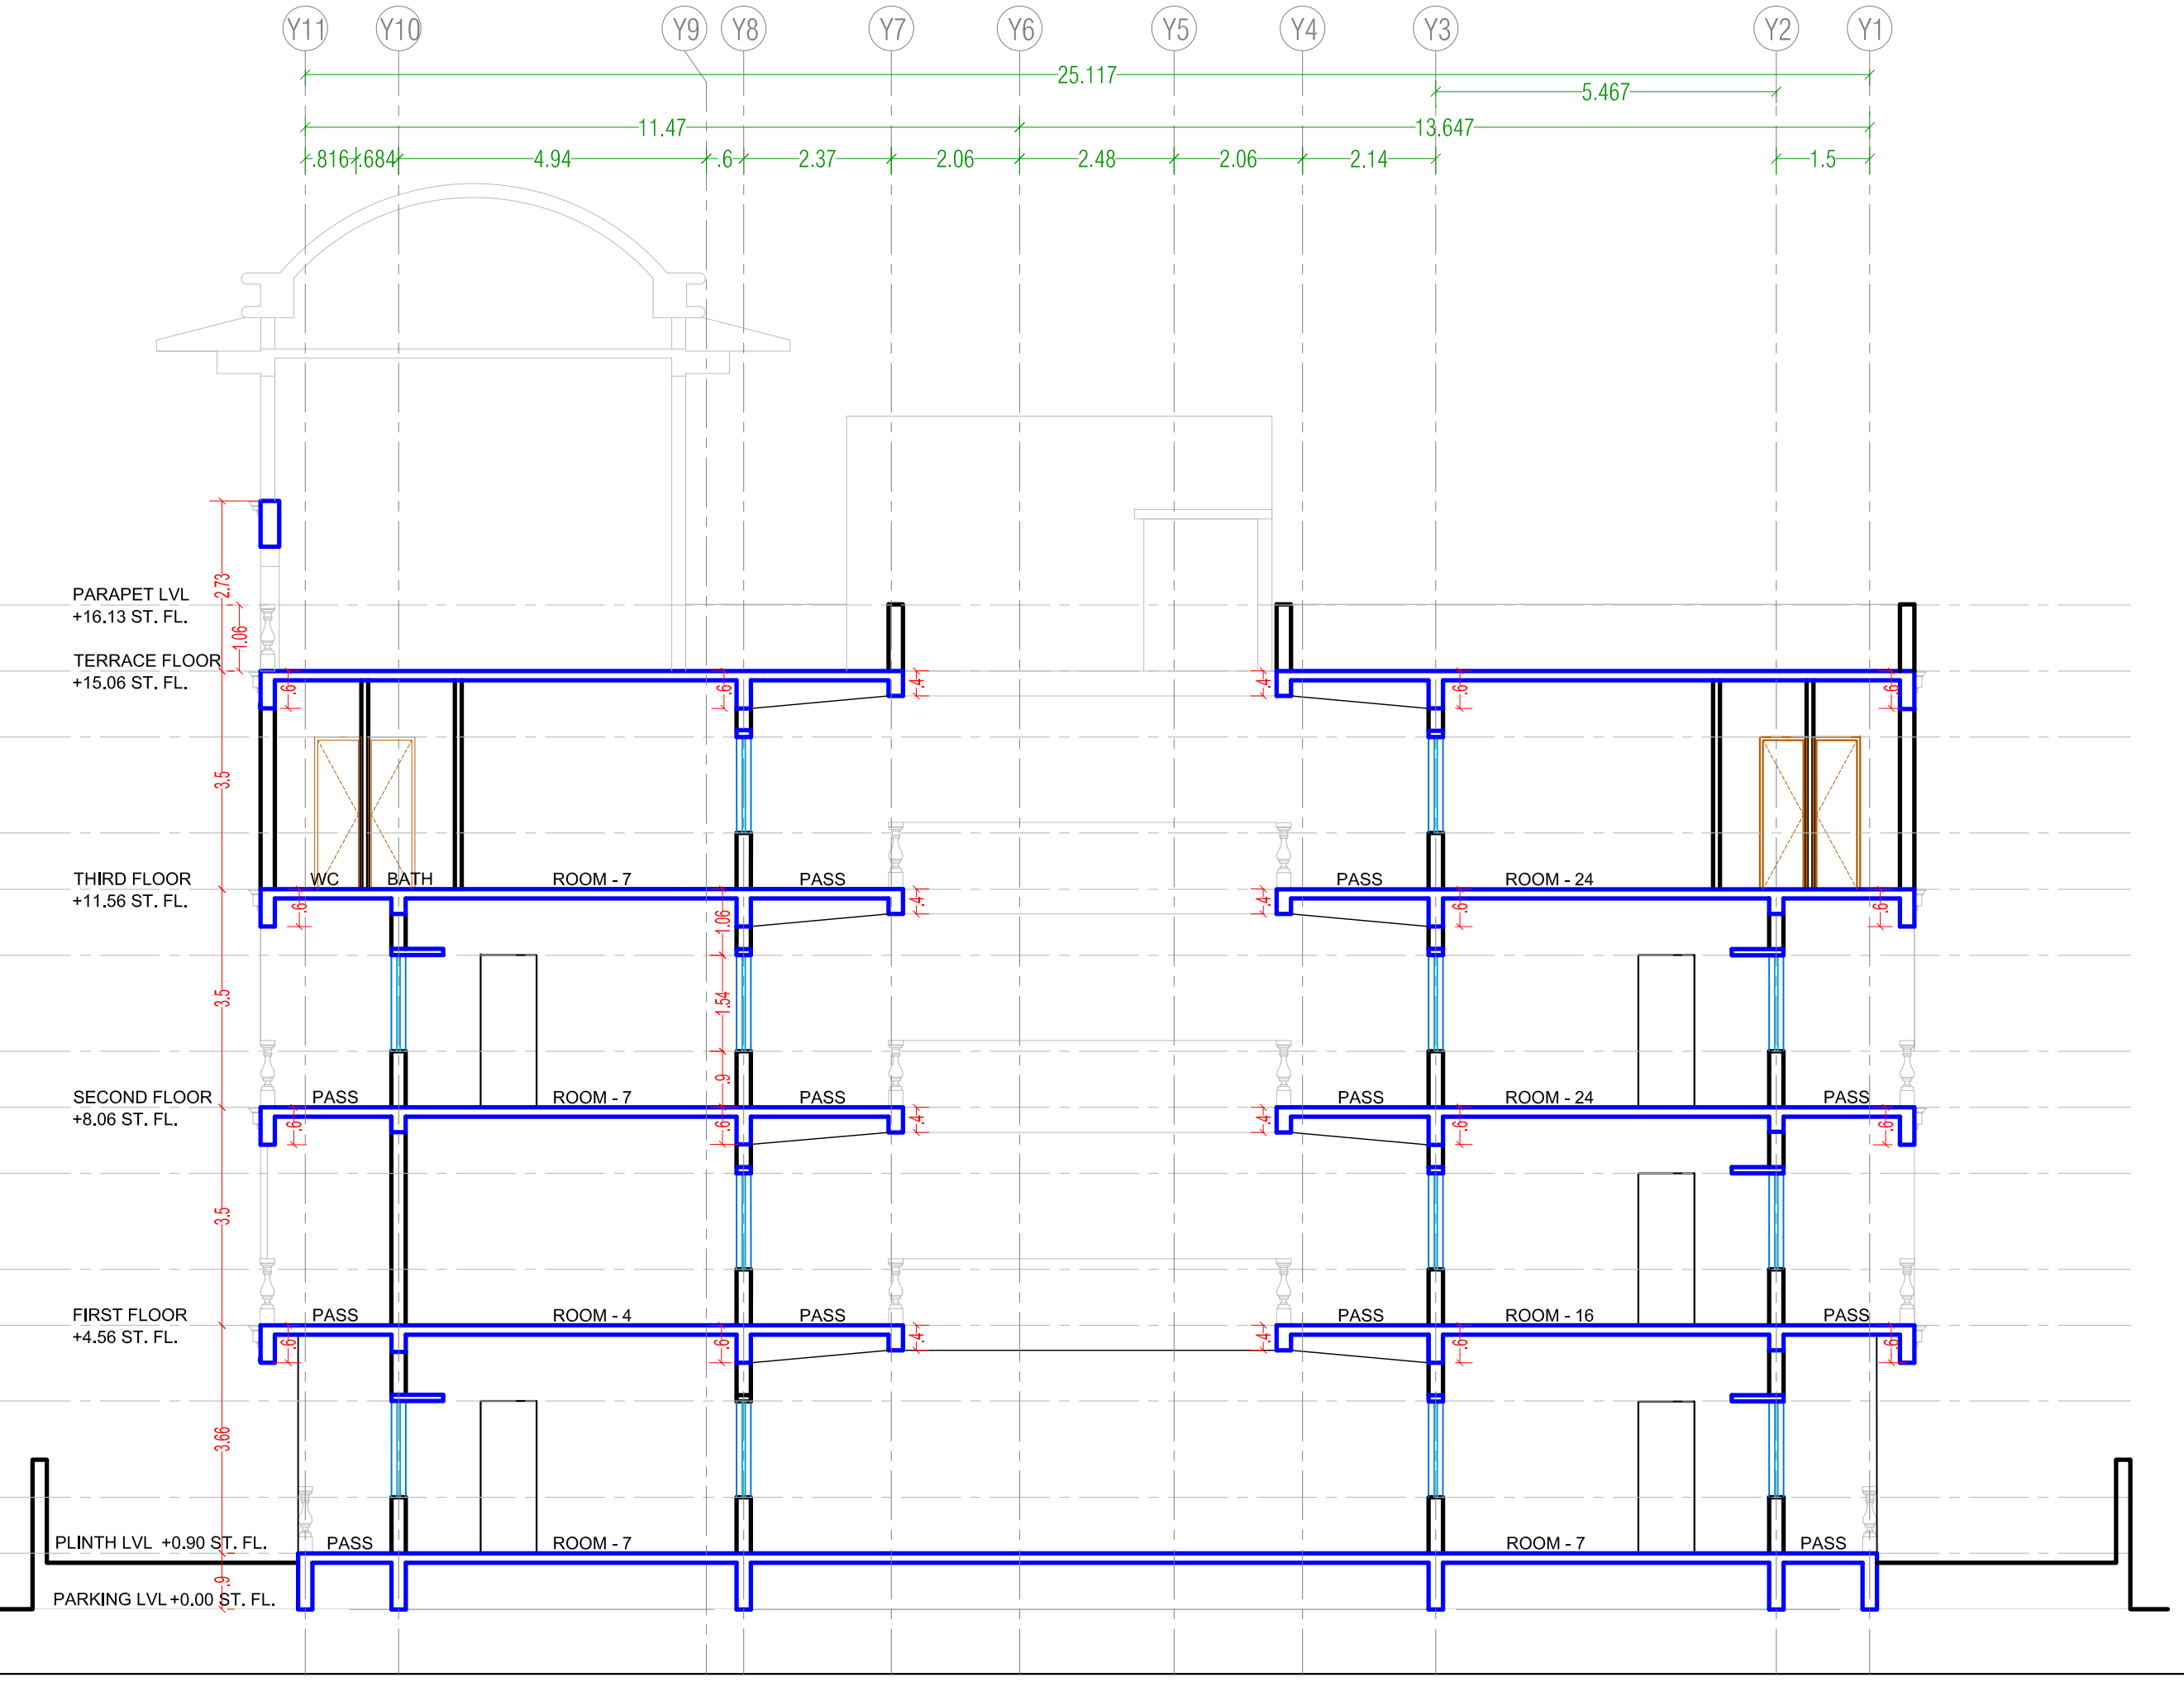


RELIGIOUS BUILDING OF GIRIVIHAR AT PALITANA

SECTION - BB

DRAWING GOOD FOR CONSTRUCTION

DRAWING NOTE :–

(1) ANY QUERY OF DRAWING OR SITE EXECUTION PLEASE CONTACT ARCHITECT OFFICE.

(2) ANY QUERY ABOUT STRUCTURE LEVEL PLEASE CONTACT STRUCTURE ENGINEER & ALSO CONSULT ARCHITECT THAN EXECUTE.

(3) PLEASE PROVIDE SLEEVE FOR DRAINAGE PIPE OR WATER PIPE ; NO JARI OR CUTTING ALLOWED IN RCC WORK.

(4) PLEASE ALSO REFER ELEVATION & SECTION DRAWING

HATCH LEGEND

SUNK

DRAINAGE LEGEND

4"Ø P.V.C. RAIN WATER PIPE
DRAINAGE PIPE

LINTLE & SILL DETAIL

LINTLE = BB (OUTER DOOR + OUTER WINDOW + OUTER VENTILATION)

LINTLE = 7'-0" (INSIDE DOOR)
SILL = 0'-6", 3'-6" (WINDOW)

SILL=0.90(IN RM)
SILL=0.61 (IN OFFICE+HALL)
SILL=1.07 (IN KITCHEN)
SILL =1.54 (IN TOILET)

SHORTCUT LEGEND :–

BB	- BEAM BOTTOM	G	- GAPE
TT	- TOP TO TOP	MDW	- MAIN DOOR+WINDOW
R	- RESIDUE	D	- DOOR
LWM	- LIGHT WT MATERIAL	W	- WINDOW
		V	- VENTILATION
		KW	- KITCHEN WINDOW
		MLW	- MID LANDING WINDOW
		LW	- LANDING WINDOW

	DATE	NO	REVISION DATE
	30-12-22	–	
SCALE	DRAWN BY		
N.T.S.	DARPIT		

DESIGN BY:–
S G ARCHITECHTS
O – 0278 2515147