
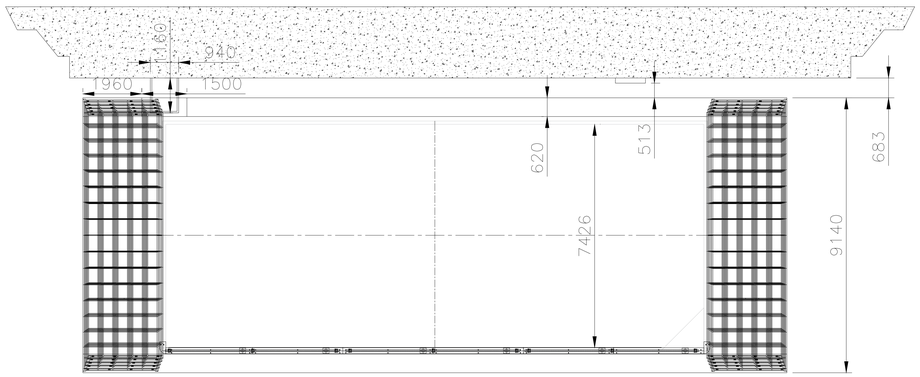


TOP VIEW

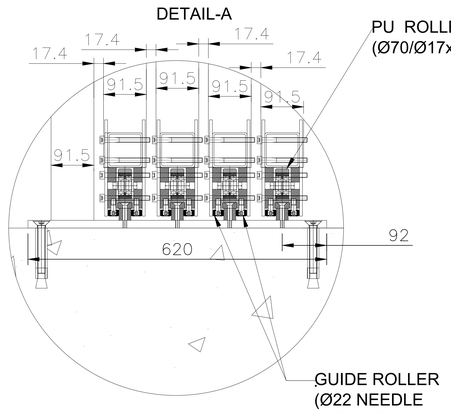

PU ROLLER
(Ø70/Ø17x28THK)


GUIDE ROLLER
(Ø22 NEEDLE
ROLLER
BEARING)

MATERIAL LIST:


Sliding,fixed segments & side wall−10+2Nos,:

sr.no.	Description	MS.Weight	Al.Wt.	acrylic	Total Kgs.
1	Fixed segment−1	341.7	42	107.0	491.0
2	sliding segment−2	423.0	39	101.3	563.5
3	sliding segment−3	419.20	38.25	100.5	558.0
4	sliding segment−4	415.55	38.05	94.60	548.20
5	sliding segment−5	411.90	37.50	94.60	544
6	sliding segment−6	411.90	37.50	94.60	544
7	sliding segment−7	415.55	38.05	94.60	548.20
8	sliding segment−8	419.20	38.25	100.5	558.0
9	sliding segment−9	423.0	39	101.3	563.5
10	sliding segment−10	339.6	42	107	489
11	LH Side wall	185	21.5	96.5	303
12	RH Side wall	185	21.5	96.5	303
13	RAIL&PLATE−1	2010			2010
14	RAIL&PLATE−2	2010			2010
	TOTAL	8410.60	432.6	1189	10033Kgs.

CLOSED CONDITION

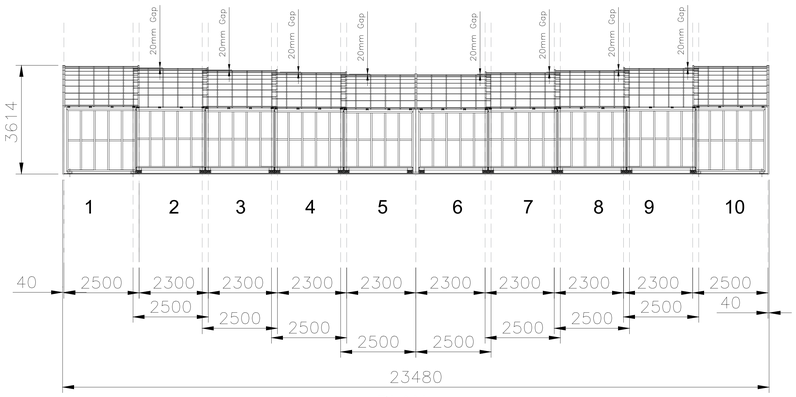


PLAN

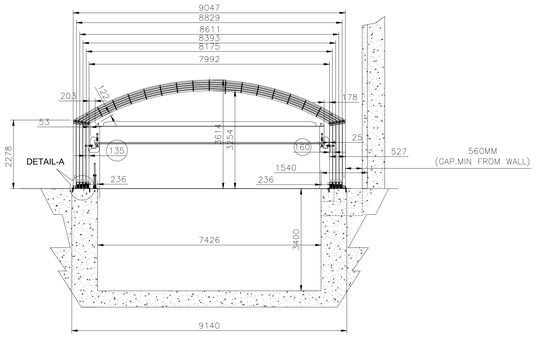

RH-SIDE VIEW

OPEN CONDITION

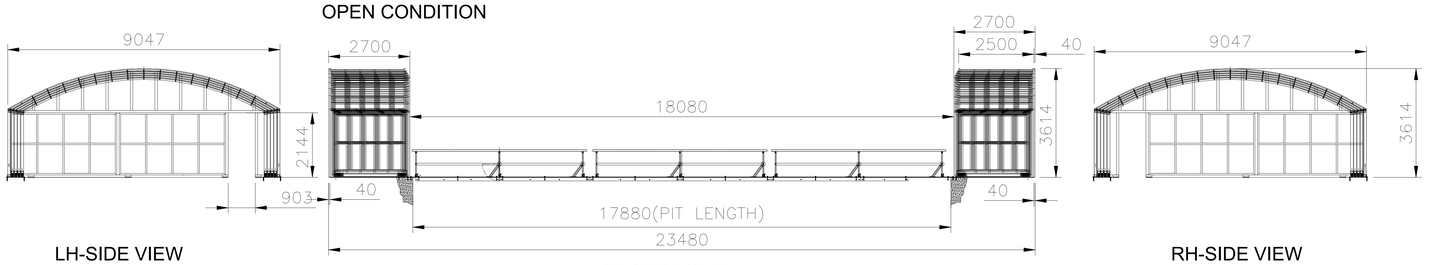

LH-SIDE VIEW

FRONT VIEW

RH-SIDE VIEW

Note:

* Rec.Pipe−50x25X2THK−882.7meter=148Nos. =1787.50Kgs.
* Rec.Pipe−80x40X2THK−202.92meter=34Nos. = 698.00Kgs.
* SQ.Pipe− 72x72X2THK−92.19meter=16Nos. = 386.30 Kgs.
* SQ.Pipe−91.5x91.5X2THK−85.40meter=15Nos.= 458.60Kgs.

Total weight of pipe material=3330.4Kgs.

Total weight of other M.S.accessories=5082.2Kgs.

Total weight.:10033.00Kgs.Approx.

M.No.	MODIFICATION	DRN	DATE	CHD.

MEASUREMENTS TO BE SPECIALLY CHECKED

DO NOT SCALE THE DRAWING.

REMOVE ALL BURRS AND SHARP CORNERS.

IF IN DOUBT,ASK.

NEGATE SHARP CORNERS.

THIS DRG.IS THE SOLE PROPERTY OF TRANSFORMER & RECTIFIER (I) LTD. AHMEDABAD. & SHOULD BE RETURNED ON REQUEST.IT SHOULD NOT BE COPIED OR COMMUNICATED TO ANY PERSON WITHOUT THE WRITTEN PERMISSION OF THE PROPERITOR.

Machining Deviation for Open Dimensions (IS:2102−1969)

Dim.									
	Over		6	30	120	315	1000	2000	4000
	Upto & Inc.	6	30	120	315	1000	2000	4000	
Tolerance		±0.1	±0.2	±0.3	±0.5	±0.8	±1.2	±2	+/−2

Surface Roughness Symbols

NEW	N12	N11	N9	N6 N5	N3	N6 GRD	N6 HRD&GRD
OLD	~	▽	▽▽	▽▽▽	▽▽▽▽	○	⊖

For other Roughness Symbols & Values See IS:3073

S.No.	QTY.	DESCRIPTION	FINISHED SIZE	MAT.	SURFACE TREATMENT	FINISH WEIGHT(KG.)

	NAME
DRN.	SUMAN M
CHD.	S.G.
APPD.	S.G.
SCALE	N.T.S
DATE	19.11.2017
ASSLY.QTY. 01	SHEET SIZE A3

ALL DIMNS. ARE IN mm

NAME OF CUSTOMER

M/S. T & R (I) LTD. AHEMEDABAD

TITLE

TANKING ENCLOSURE

(GA DRAWING)

TRANSFORMER & RECTIFIER (I) LTD. AHMEDABAD.

PROJECT NO.

W.NO.−−−

SHEET 1 OF 1

DRG. NO.

20171119/01−01R0