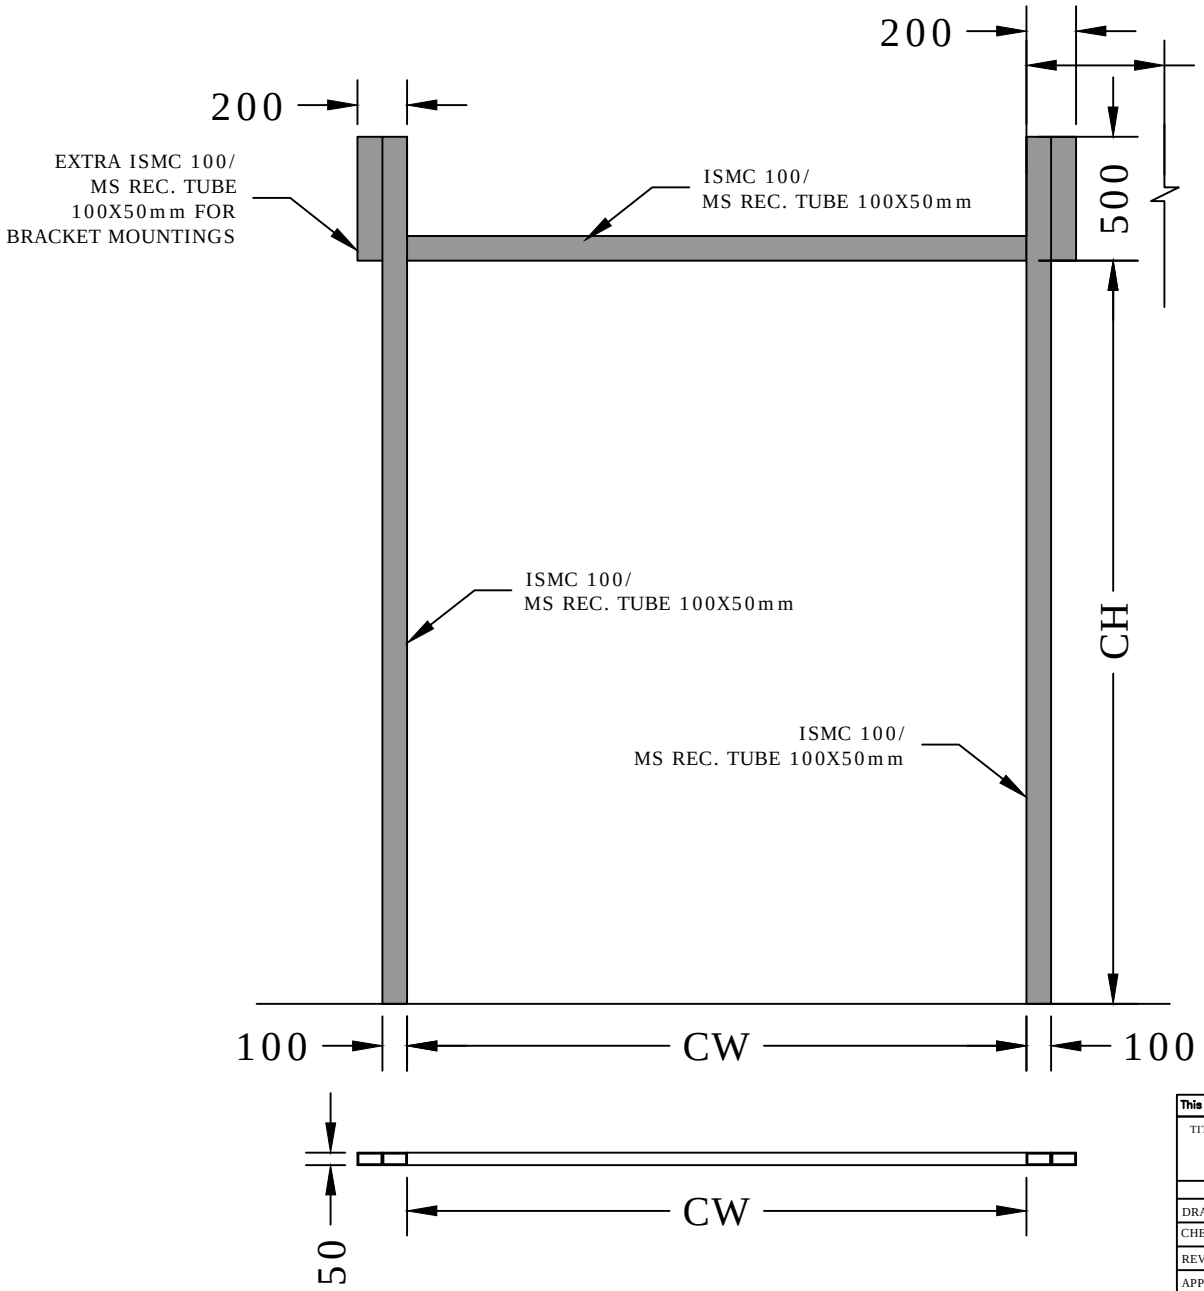


| CLEAR WIDTH (CW) | CLEAR HEIGHT (CH) | QUANTITY |
|---|---|---|
| 2000 mm | 3000 mm | 2 NOS |
| 2500 mm | 3000 mm | 1 NOS |

This drawing & design is the property of NIHVA TECHNOLOGIES. Not to be sold or copied to any other concern.

TITLE: MS STRUCTURE FOR DOUBLE WALL ROLLING SHUTTER 2

NIHVA TECHNOLOGIES PVT. LTD. PUNE
Tel : 020 66304033
Email:- info@nihva.com
Website:- www.nihva.com

| | SIGN | DATE |
|---|---|---|
| DRAWN | OMKAR | 13/10/17 |
| CHECK | SHEKHAR | 13/10/17 |
| REV. | | |
| APPROVAL | SHEKHAR | 13/10/17 |

If any queries contact : projects@nihva.com

ALL DIMENSION ARE IN mm

CLIENT - DHOOT BUILDERS

PROJECT - SKODA AUTO IND.PVT.LTD

SITE - AURANGABAD

DWG. NO. : NIHVA/17-18/0240

SCALE: NTS | WT: | SHEET: 01 OF 01