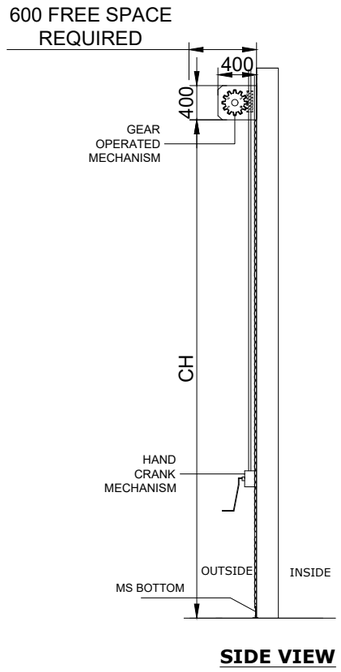
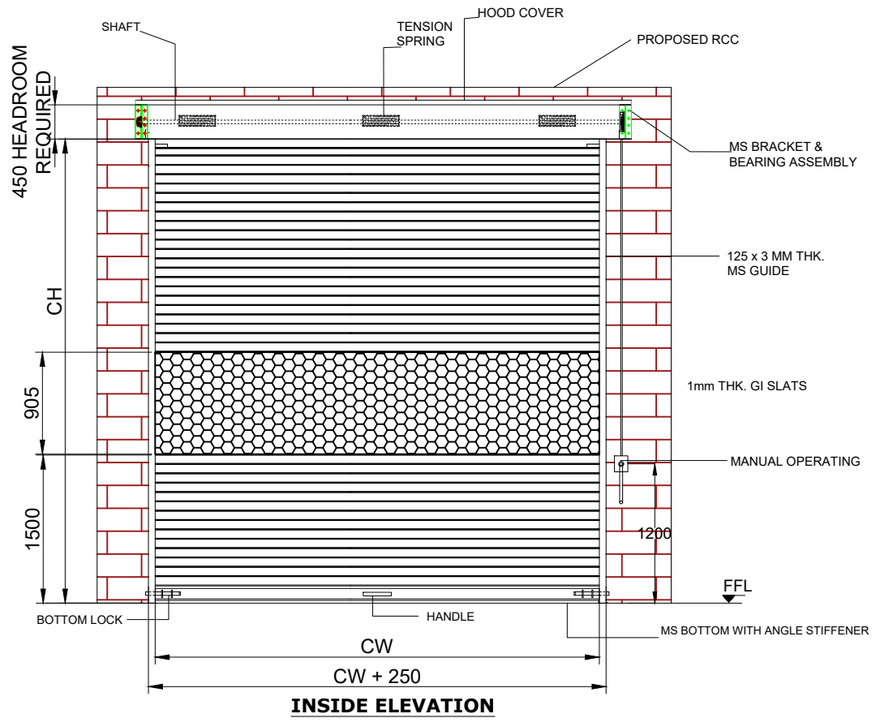


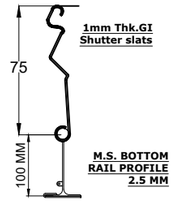

**SIDE VIEW**



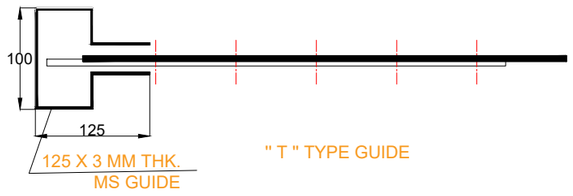

**INSIDE ELEVATION**




**PLAN**




**M.S. BOTTOM RAIL PROFILE 2.5MM**




" T " TYPE GUIDE

NOTE-
1. ALL CIVIL WORK WILL BE CLIENT'S SCOPE.
2.IF STRUCTURE REQUIRED FOR SHUTTER IS IN CLIENT'S SCOPE.

# TECHNICAL SPECIFICATION:-

| SR. | SPECIFICATION | DETAILS |
|---|---|---|
| 1. | DESCRIPTION & DRIVE | GEAR OPERATED SHUTTER |
| 2. | LOCATION AREA | OUTSIDE AREA |
| 3. | MOUNTING SURFACE | SIDE BRACKETS: ON CONCRETE |
| 4. | SLAT | 75 MM WIDE - 1 MM THICK GI |
| 5. | BOTTOM PROFILE | M.S. PLATE 100X2.5 MM THICK WITH ANGLE STIFFNER |
| 6. | GUIDE PROFILE | M.S."T" SHAPE -100X125X3 MM THK . |
| 7. | HOOD COVER & MOTOR COVER | MADE OF GI SHEET THICKNESS 0.9 MM. |
| 8. | MATERIAL FINISH | SYNTHETIC ENAMEL PAINT |

| SR NO | ( CW ) CLEAR WIDTH | ( CH ) CLEAR HEIGHT | QUANTITY |
|---|---|---|---|
| 1 | 3970 | 4120 | 01 NOS |
| 2 | 3930 | 4140 | 01 NOS |
| 3 | 4000 | 4100 | 01 NOS |
| 4 | 4020 | 4170 | 01 NOS |
| 5 | 4000 | 4160 | 01 NOS |
| 6 | 3970 | 4170 | 01 NOS |
| 7 | 4000 | 4180 | 01 NOS |

This drawing & design is the property of NIHVA TECHNOLOGIES. Not to be sold or copied to any other concern.

TITLE
GEAR OPERATED ROLLING SHUTTER

| | NAME | SIGN | DATE |
|---|---|---|---|
| DRAWN | B.S. | | 06.10.2025 |
| CHECK | V.T. | | 06.10.2025 |
| APPRD. | V.T. | | 06.10.2025 |

If any queries contact : design@nihva.com

ALL DIMENSION ARE IN mm

NIHVA
NIHVA TECHNOLOGIES PVT. LTD.
Website:- www.nihva.com
NIHVA TECHNOLOGIES PVT. LTD. PUNE
Tel : 020 66304033
Email:- info@nihva.com

CLIENT - VTP
PROJECT -
SITE LOCATION -
DWG. NO. : NIHVA/21-22/VDR/020 | REV- R00
SCALE: NTS | WT: | SHEET: 01 OF 01