
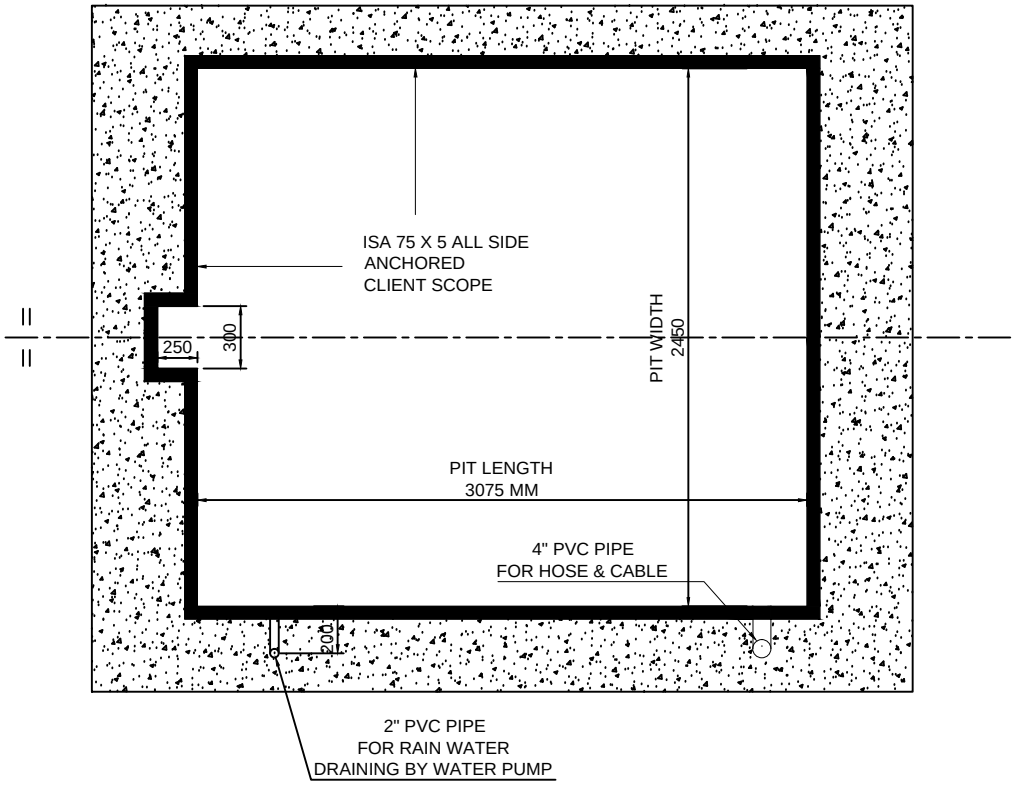


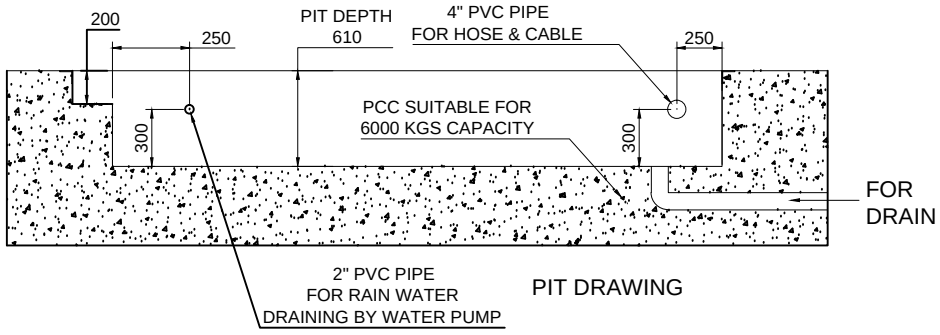

PIT DRAWING

NOTE :

1. HYDRAULIC HOSE LENGTH : 12 MTR
2. ELECTRICAL CABLE : 12 MTR
3. PIT / CIVIL / PVC PIPE WILL BE IN CLIENT SCOPE.
4. COLOR : a. GOLDEN YELLOW.
   b. ULTRA MARINE BLUE.
5. INPUT SUPPLY : 3 PHASE 400 VOLT WITH NEUTRAL.

REV NO	DATE	DRAWN	REMARK
R01	24.01.20	P.A	1. DRAIN ARRANGEMENT ADD

This drawing & design is the property of NIHVA TECHNOLOGIES. Not to be sold or copied to any other concern.

TITLE	ELECTRO HYDRAULIC SCISSOR LIFT PIT DRG		

NIHVA TECHNOLOGIES PVT. LTD.
NIHVA TECHNOLOGIES PVT. LTD. PUNE
Tel : 020 66304033
Email:- info@nihva.com
Website:- www.nihva.com

	NAME	SIGN	DATE
DRAWN	P.V.A		15.11.2019
CHECK	V.M.T		15.11.2019
APPRD.			

CLIENT - IKEA

PROJECT -

SITE LOCATION -

If any queries contact : design@nihva.com

DWG. NO. : NIHVA/19-20/0153/R01 REV- R01

ALL DIMENSION ARE IN mm

SCALE: NTS WT: SHEET: 01 OF 01