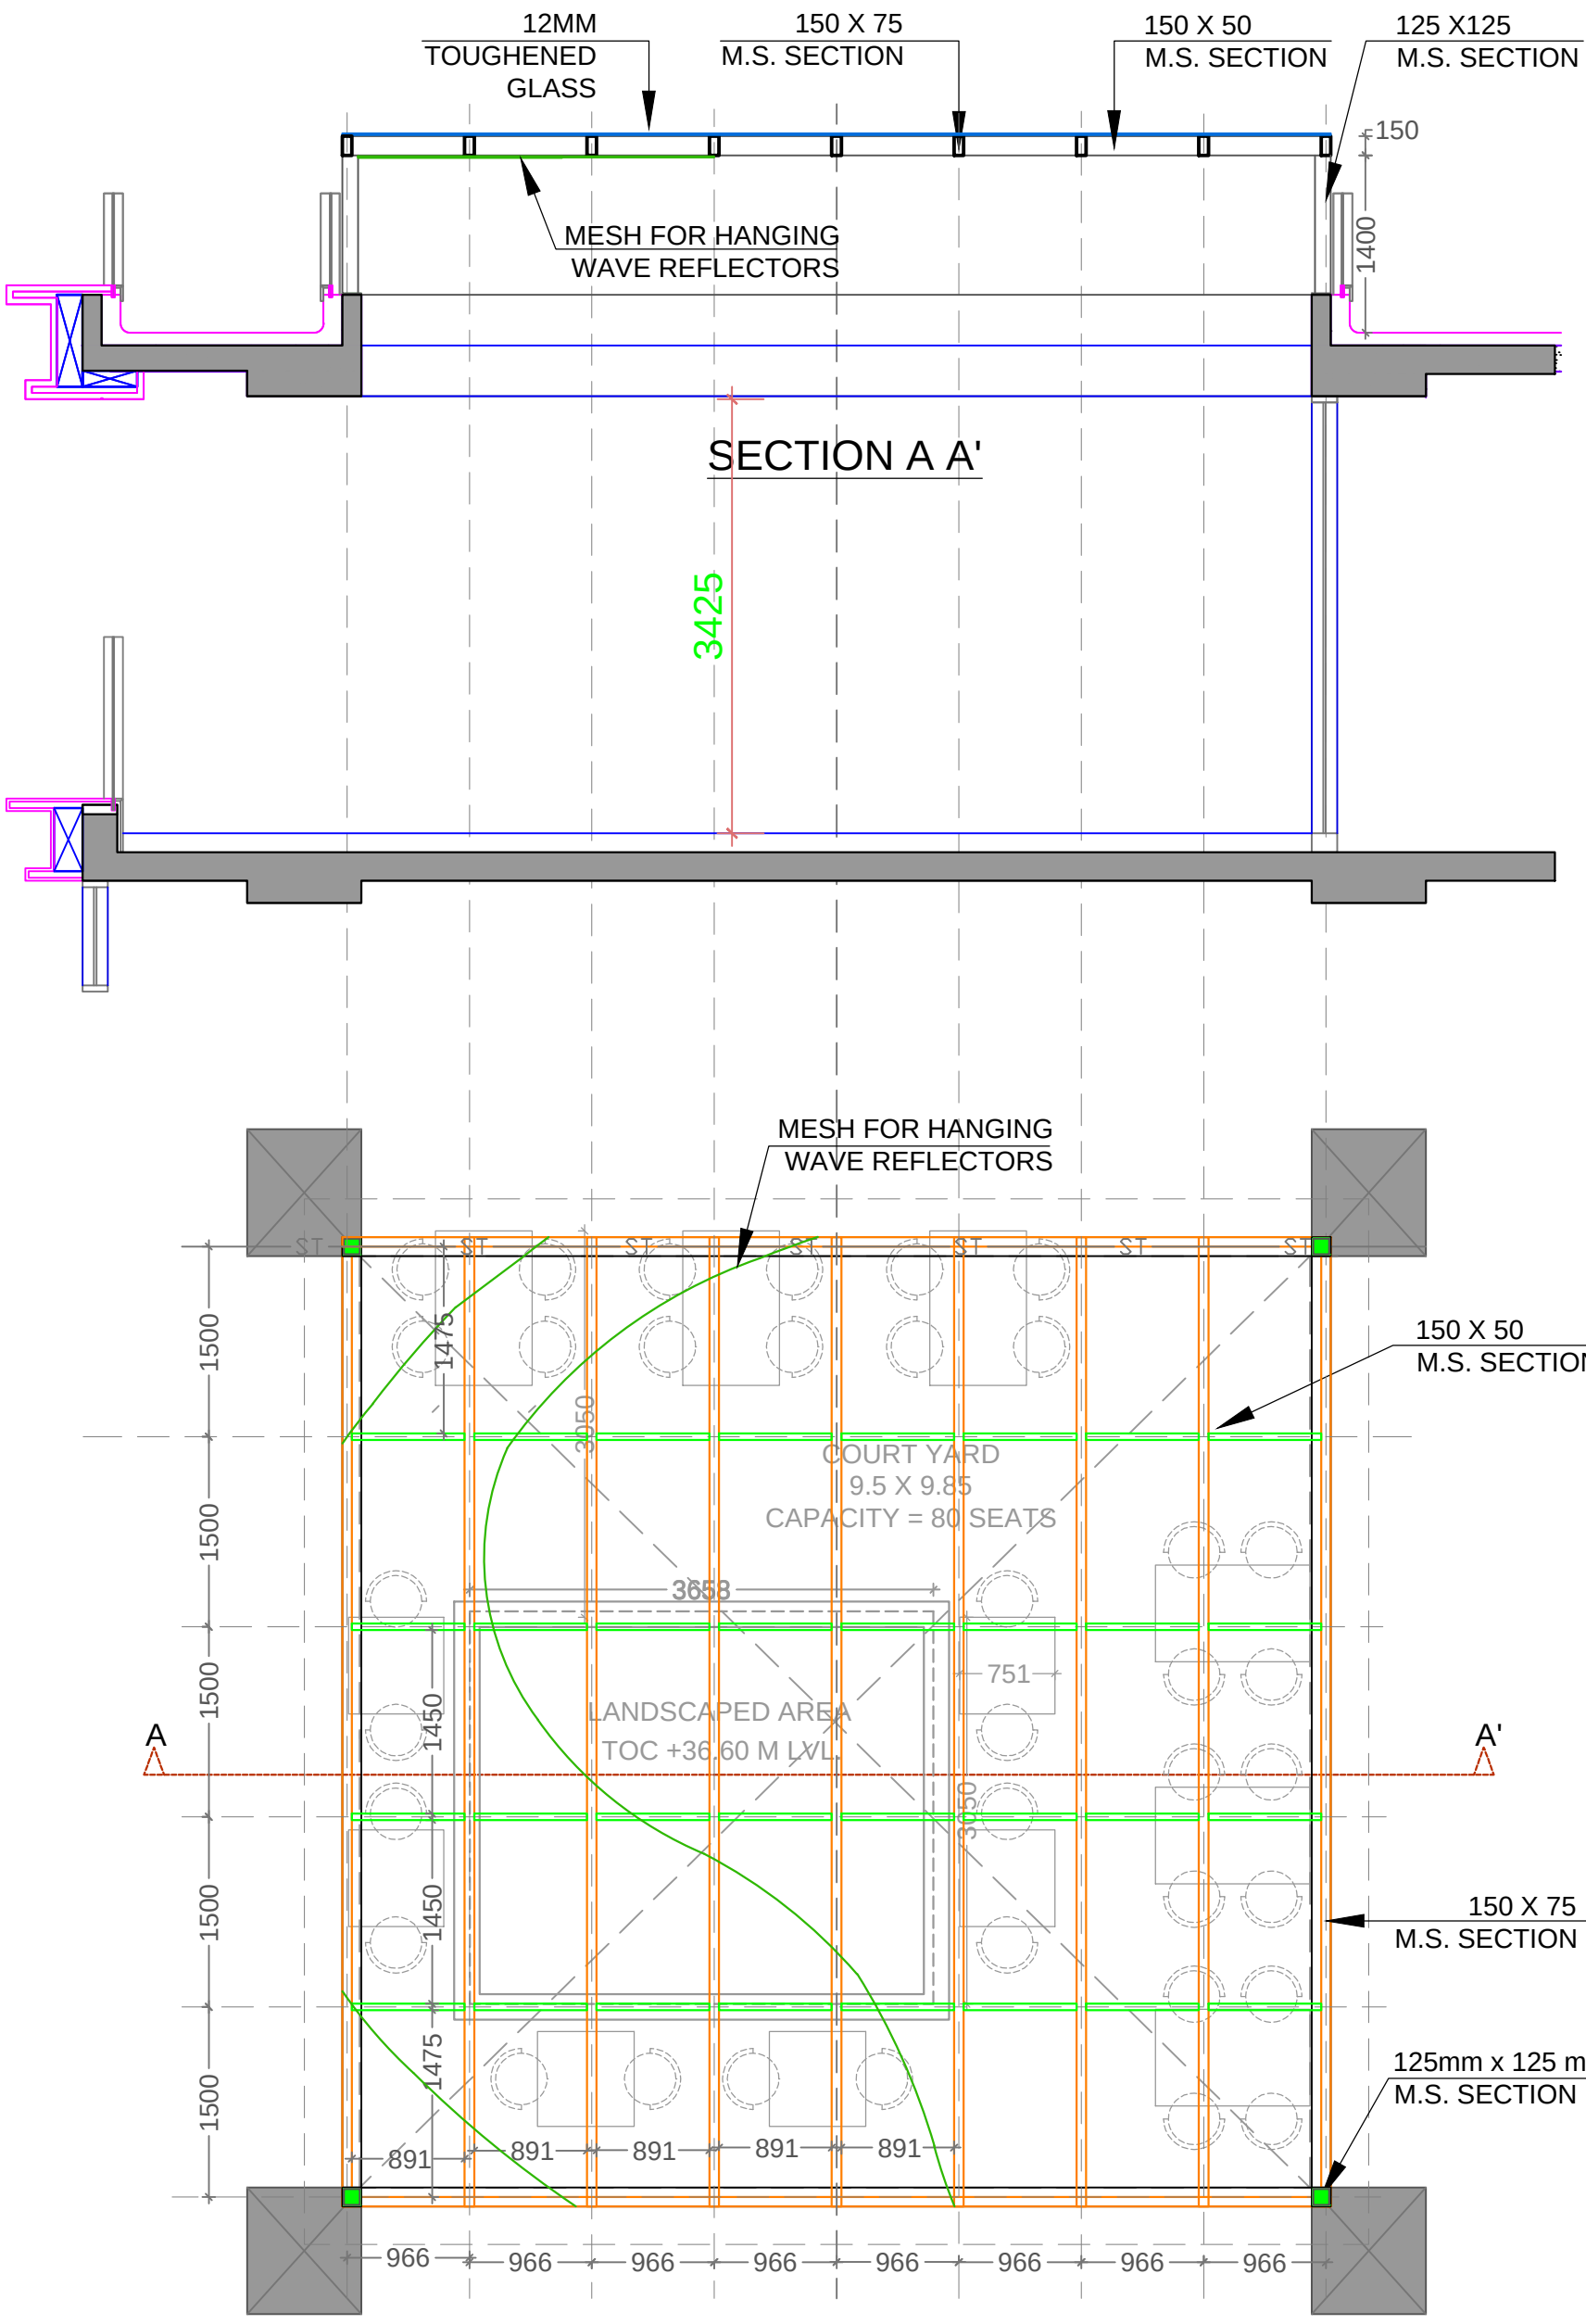


SECTION A A'

PLAN

COURT YARD PERGOLA DETAIL

PROJECT -

PROPOSED INTERIOR LAYOUT
OF 24 K BREWZ
AT BALEWADI HIGH STREET PUNE

14 01 2020

HARSHADA NAIK & ASSOCIATES

ARCHITECTS,LANDSCAPE & INTERIOR DESIGNERS.
306, DATTAWAD RENAISSANCE,
TRADE CENTRE COMPLEX, SHAHUPURI, KOLHAPUR.
TEL : 9158910129