



PLAN

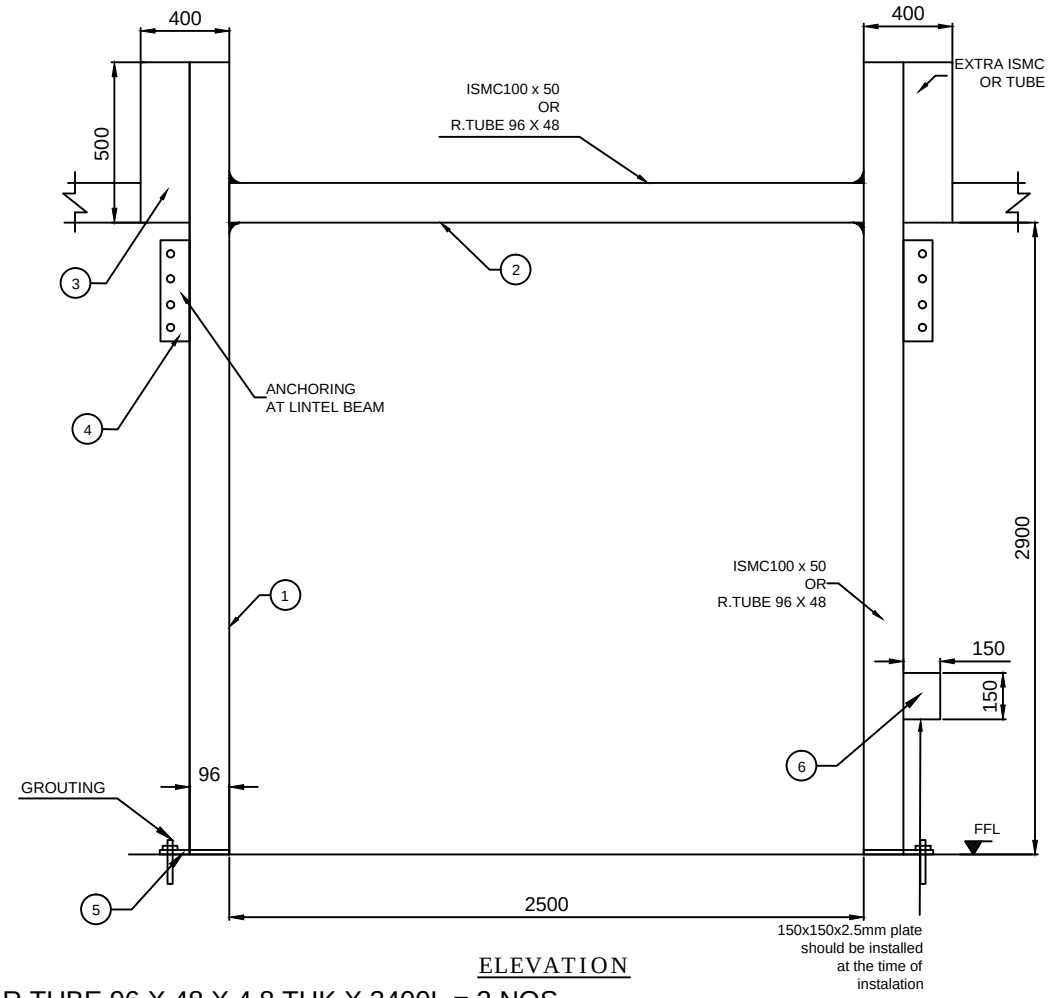


ELEVATION

1. R.TUBE 96 X 48 X 4.8 THK X 3400L = 2 NOS
2. R.TUBE 96 X 48 X 4.8 THK X 2500L = 1 NO
3. R.TUBE 96 X 48 X 4.8 THK X 500L = 6 NOS
4. ISA 75 X 8 X 300L = 2 NOS
5. FLAT 100 X 10 X 150L = 2 NOS
6. FLAT 150 X 6 THK X 150L = 1 NO

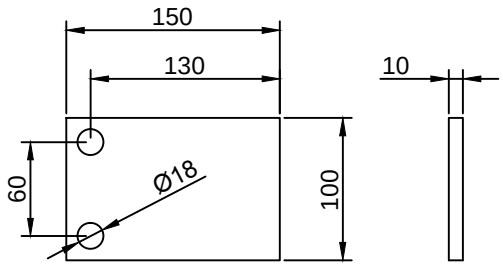

5

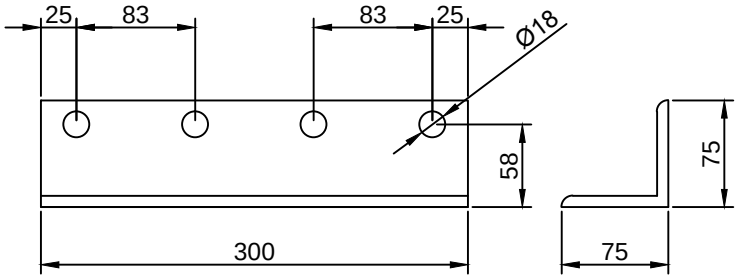

4

TOLERANCE - ±10mm

This drawing & design is the property of NIHVA TECHNOLOGIES. Not to be sold or copied to any other concern.

TITLE: GEAR OPERATED ROLLING SHUTTER STRUCTURE			NIHVA TECHNOLOGIES PVT. LTD. PUNE Tel : 020 66304033 Email:- info@nihva.com Website:- www.nihva.com
	NAME	SIGN	DATE
DRAWN	P.A		30.07.2020
CHECK	G.J		30.07.2020
APPRD.			
CLIENT -			
PROJECT-			
SITE LOCATION -			
If any queries contact : design@nihva.com	DWG. NO. : NIHVA/20-21/VDR/0022		REV- R00
ALL DIMENSION ARE IN mm	SCALE: NTS	WT:	SHEET: 01 OF 01