

DRAWING


ITEM NO.	PART NUMBER	DESCRIPTION	QTY.
1	HWM UNIT WALKWAY-1 W 630X L 13096 MM LONG	MS SQ TUBE SIZE- 30X30X2.6MM THK	4
2	CHEQUERED_MS PLATE_W630 X L1306 MM LONG	MS CHEQURED PLATE SIZE- W 630 X L 1306 X 3 MM THK	4

REV DESCRIPTION	DATE	REV NO
	28-08-2025	REV 00
1.		

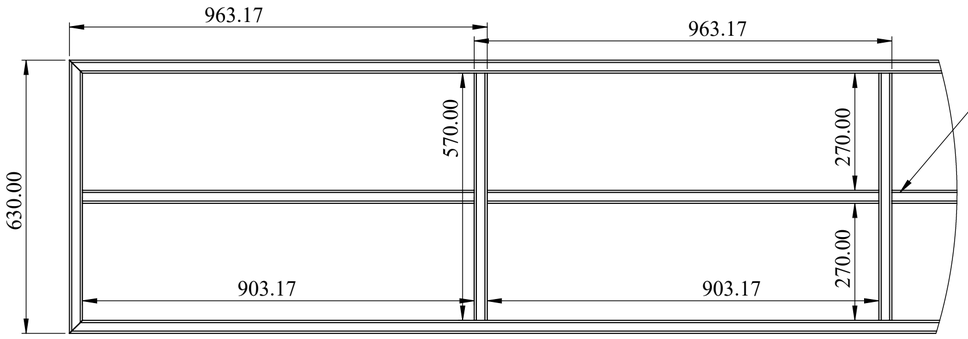

DETAIL A
SCALE 1 : 10

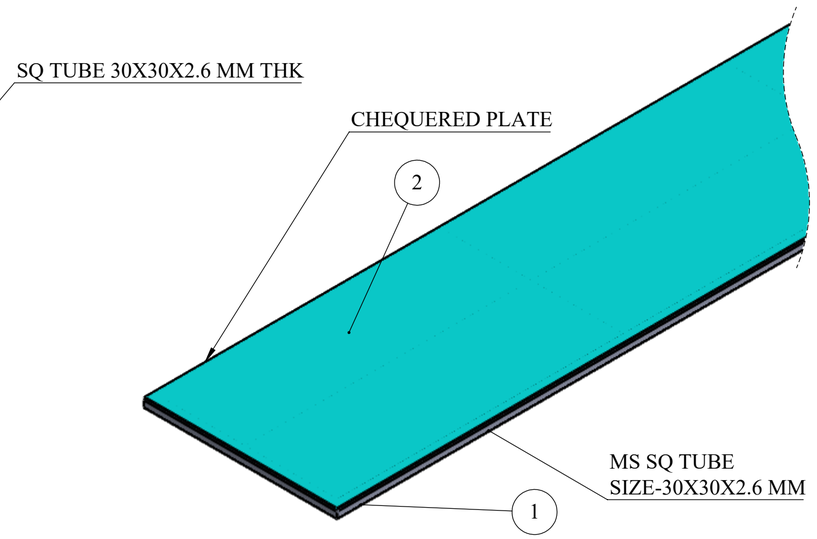

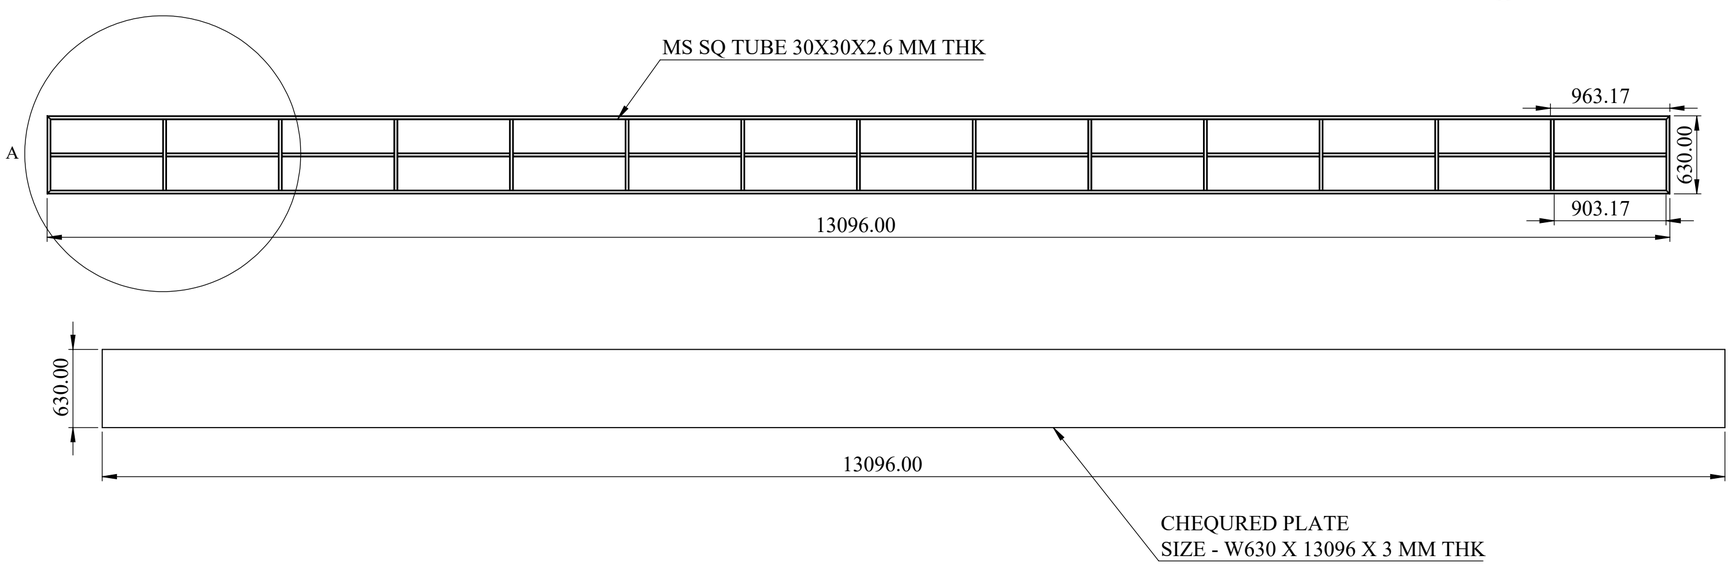

NOTE :

NAME: WALKWAY'S
SIZE : 630x13096 MM LONG
MTL : MS
QTY : 04 NOS

SPECIAL INSTRUCTION'S :

TITLE - ROOF AUTOMATION			
DWG NO - NTPL-244-PM-001-00-00-00			
	NAME	SIGNATURE	DATE
DRAWN	V.W.		28-08-2025
CHK'D	S.P.		04-09-2025
APPV'D	V.T.		05-09-2025
If any queries contact - Design@nihva.com			
ALL DIMENSION ARE IN mm			A2

NIHVA Technologies Pvt. Ltd.
NIHVA TECHNOLOGIES PVT.LTD.PUNE
Website - www.nihva.com

PRODUCT - RETRACTABLE ROOF	
PROJECT NO - NTPL-244-PM	REVISION - 00
SITE LOCATION - GUJARAT	WEIGHT -
MATRIAL -	QTY - 1
PROJECTION METHOD:	SCALE :
	SHEET 2 OF 4