




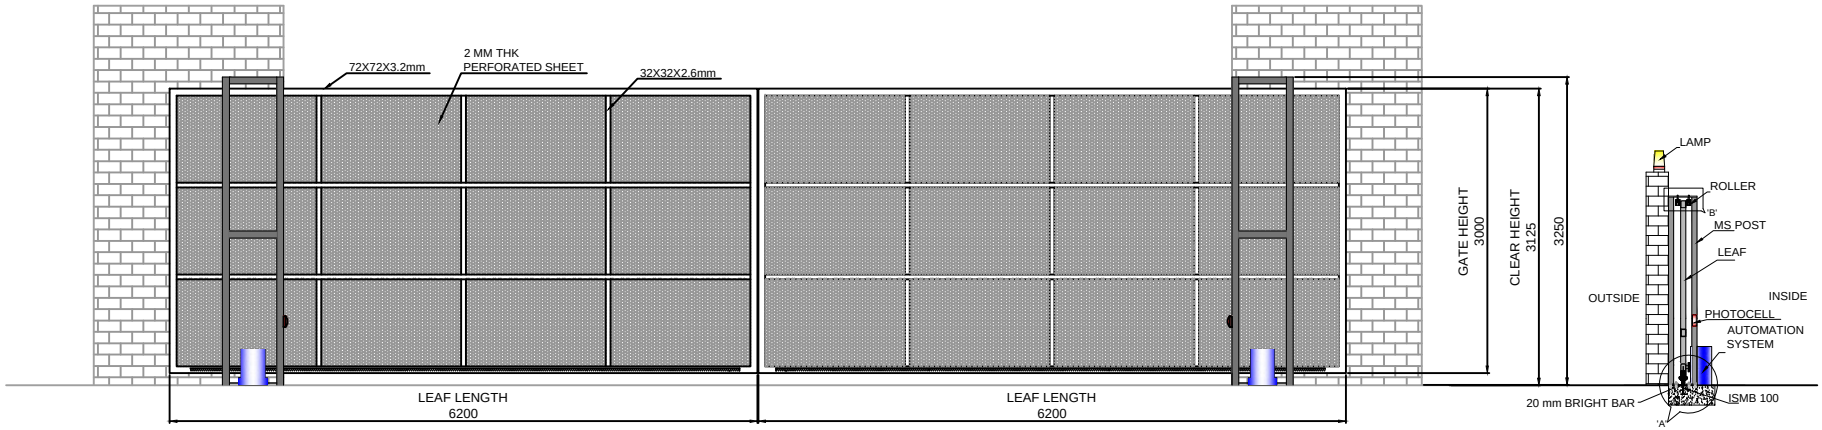


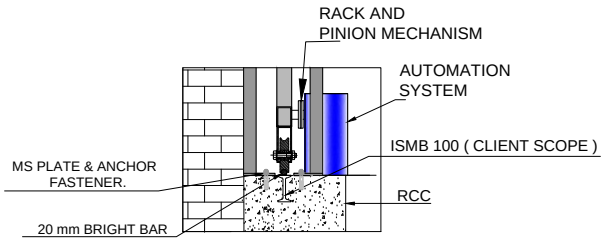

DETAIL VIEW OF A

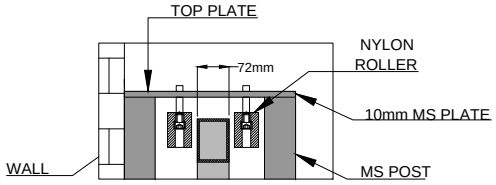


DETAIL VIEW OF B

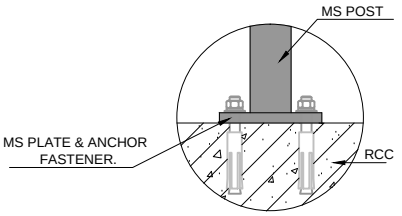


DETAIL VIEW OF C
(FIXING DETAILS)

This drawing & designing is the property of NIHVA TECHNOLOGIES. Not to be sold or copied to any other concern.

| | | | |
|---|---|---|---|
| TITLE: AUTOMATIC BI-PARTING SLIDING GATE | | | NIHVA TECHNOLOGIES PVT. LTD. PUNE<br>Tel : 020 66304033<br>Email:- info@nihva.com<br>Website:- www.nihva.com |
| | NAME | SIGN | DATE |
| DRAWN | P.V.A | | 02.08.19 |
| CHECK | V.M.T | | 02.08.19 |
| APPROVAL | | | |
| CLIENT - INOX | | | |
| PROJECT - | | | |
| SITE LOCATION -BARJORA,WEST BENGAL | | | |
| If any queries contact : design@nihva.com | DWG. NO. : NIHVA/19-20/0070 | | REV.:- R00 |
| ALL DIMENSION ARE IN mm | SCALE: NTS | WT: | SHEET: 01 OF 01 |