
PRODUCED BY AN AUTODESK EDUCATIONAL PRODUCT

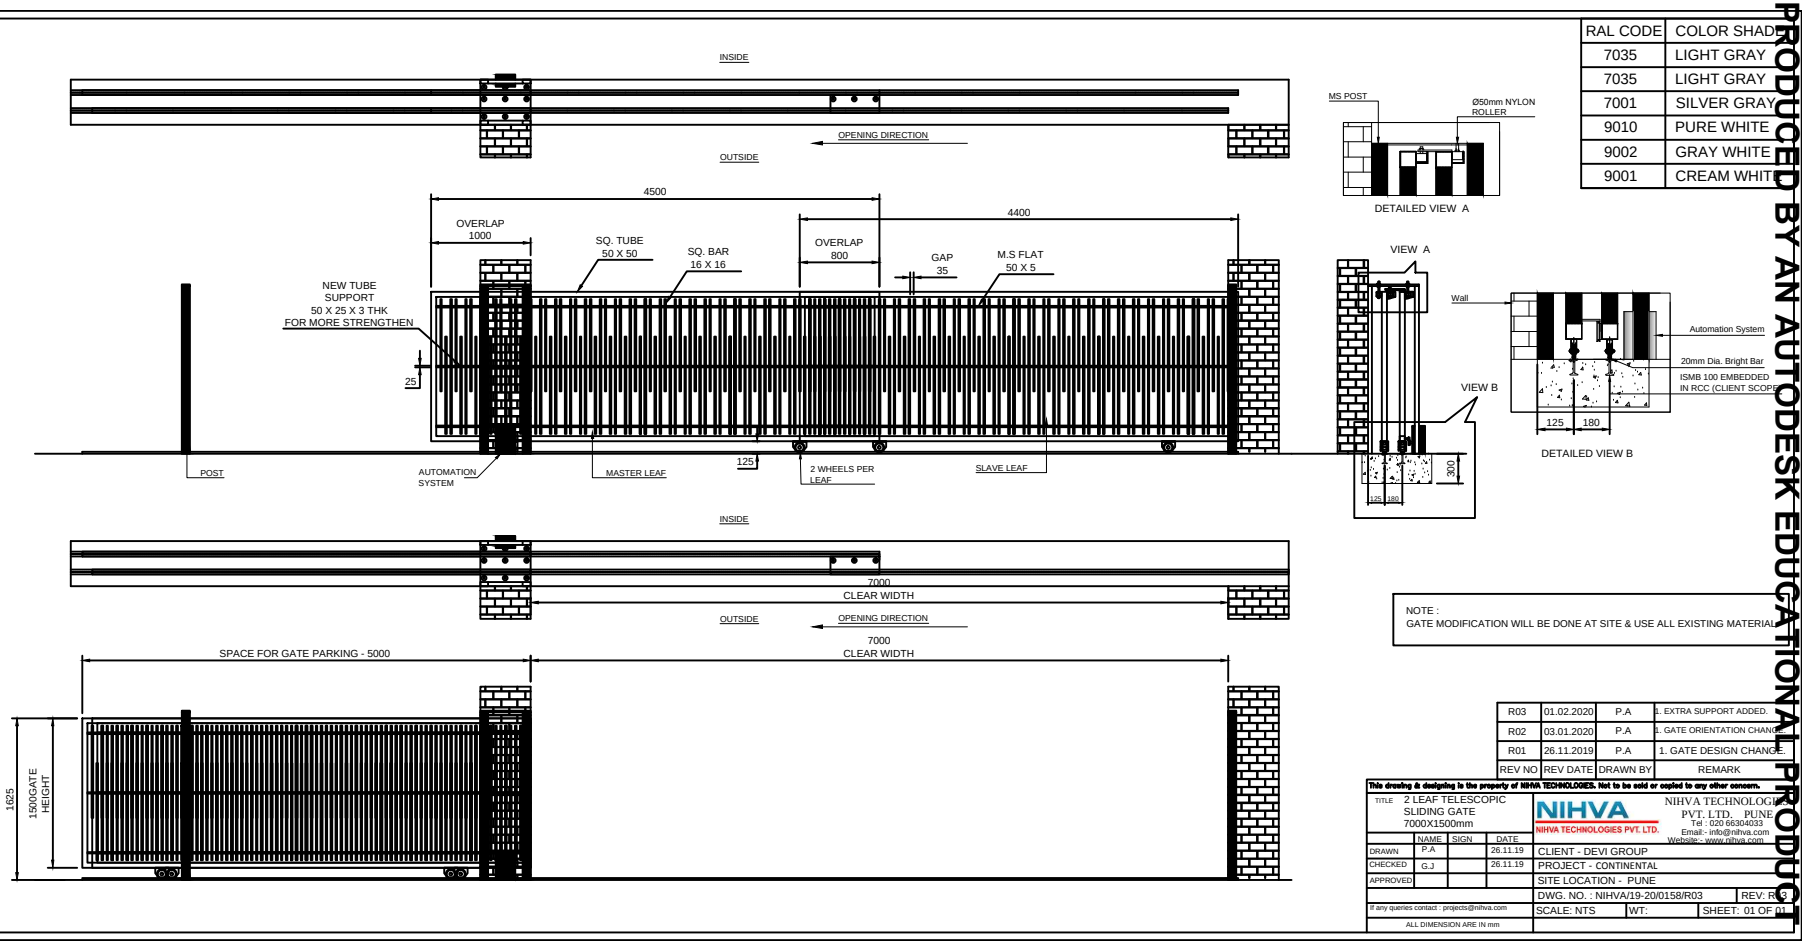

RAL CODE	COLOR SHADE
7035	LIGHT GRAY
7035	LIGHT GRAY
7001	SILVER GRAY
9010	PURE WHITE
9002	GRAY WHITE
9001	CREAM WHITE

NOTE :
GATE MODIFICATION WILL BE DONE AT SITE & USE ALL EXISTING MATERIAL.

REV NO	REV DATE	DRAWN BY	REMARK
R03	01.02.2020	P.A	1. EXTRA SUPPORT ADDED.
R02	03.01.2020	P.A	1. GATE ORIENTATION CHANGE.
R01	26.11.2019	P.A	1. GATE DESIGN CHANGE.

This drawing & designing is the property of NIHVA TECHNOLOGIES. Not to be sold or copied to any other concern.

TITLE: 2 LEAF TELESCOPIC SLIDING GATE 7000X1500mm

NIHVA TECHNOLOGIES PVT. LTD.

NIHVA TECHNOLOGIES PVT. LTD. PUNE
Tel : 020 66304033
Email:- info@nihva.com
Website:- www.nihva.com

	NAME	SIGN	DATE
DRAWN	P.A		26.11.19
CHECKED	G.J		26.11.19
APPROVED			

CLIENT - DEVI GROUP
PROJECT - CONTINENTAL
SITE LOCATION - PUNE
DWG. NO. : NIHVA/19-20/0158/R03 REV: R03
SCALE: NTS WT: SHEET: 01 OF 01

If any queries contact : projects@nihva.com

ALL DIMENSION ARE IN mm

PRODUCED BY AN AUTODESK EDUCATIONAL PRODUCT

PRODUCED BY AN AUTODESK EDUCATIONAL PRODUCT