

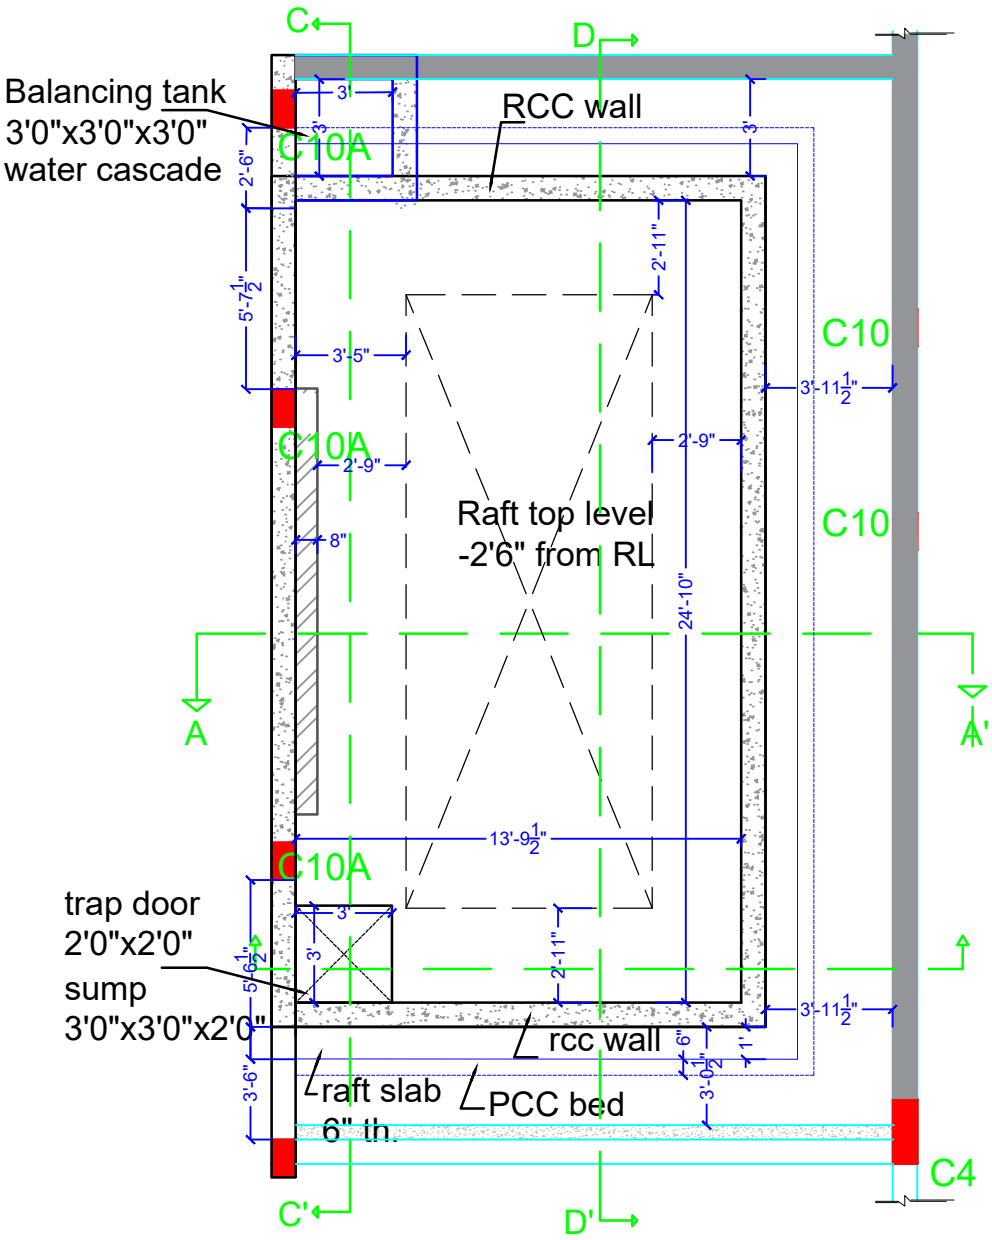


PLAN

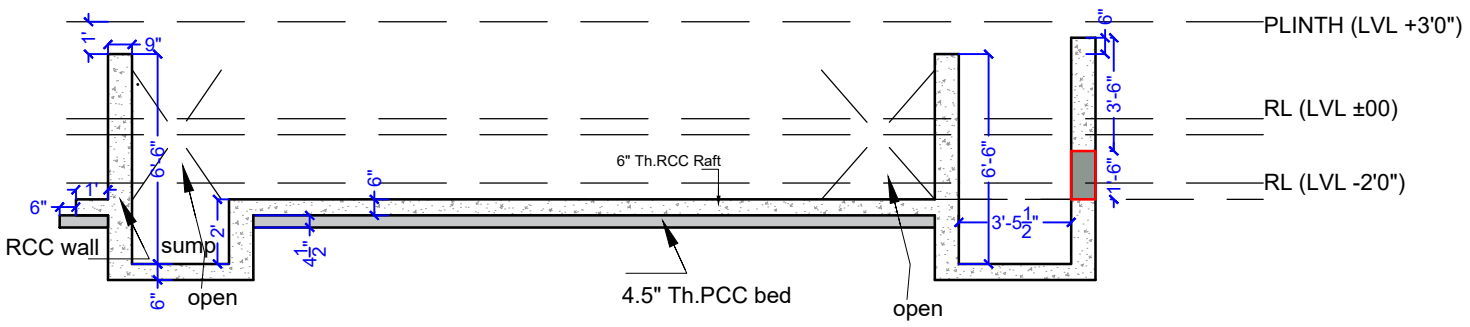

SECTION CC'

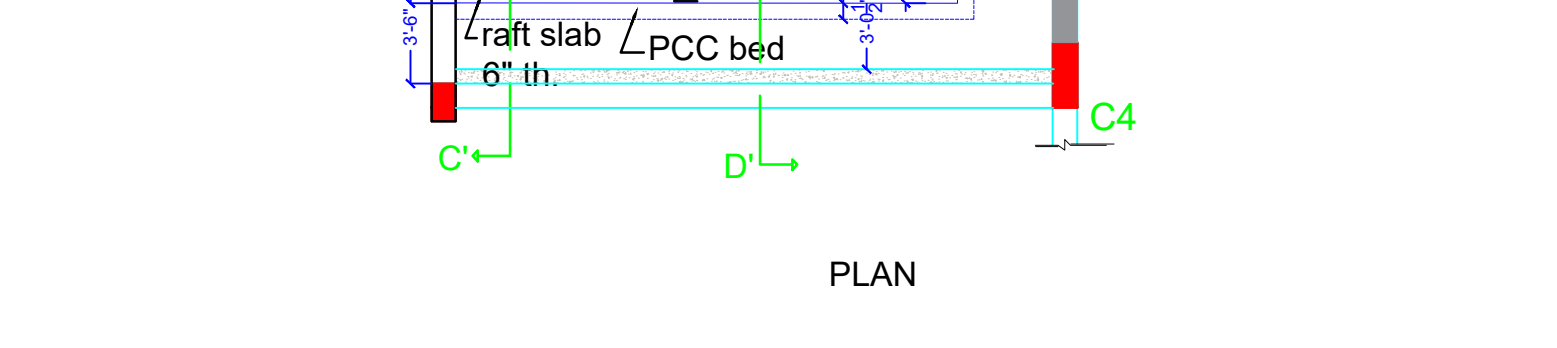

SECTION DD'

BLDG.	RESIDENCE-BUILDING_EAST-FACING
DWG NO :	
TITLE :	WORKING_DRAWING
REV : 00	DATE: R0-26-06-2025
CHK: Mr. N. BAJPAI / DRAWN: NIYATI	SCALE : -

REV	DESCRIPTION	DATE
00		

POOL DETAIL

CLIENT:-

PROPOSED RESIDENCE BUILDING
PLAN FOR - **MR. VISHAL AGRAWAL JI**
PLOT NO.-....., KH.NO.-.....
PH.NO.- , AT-TILDA, (C.G.)
email-

NEERAJ BAJPAI & ASSOCIATES

C-18, RAVI NAGAR, RAIPUR
CHHATTIS GARH .
tel : +91-771-2424495
email: designcell2006@gmail.com