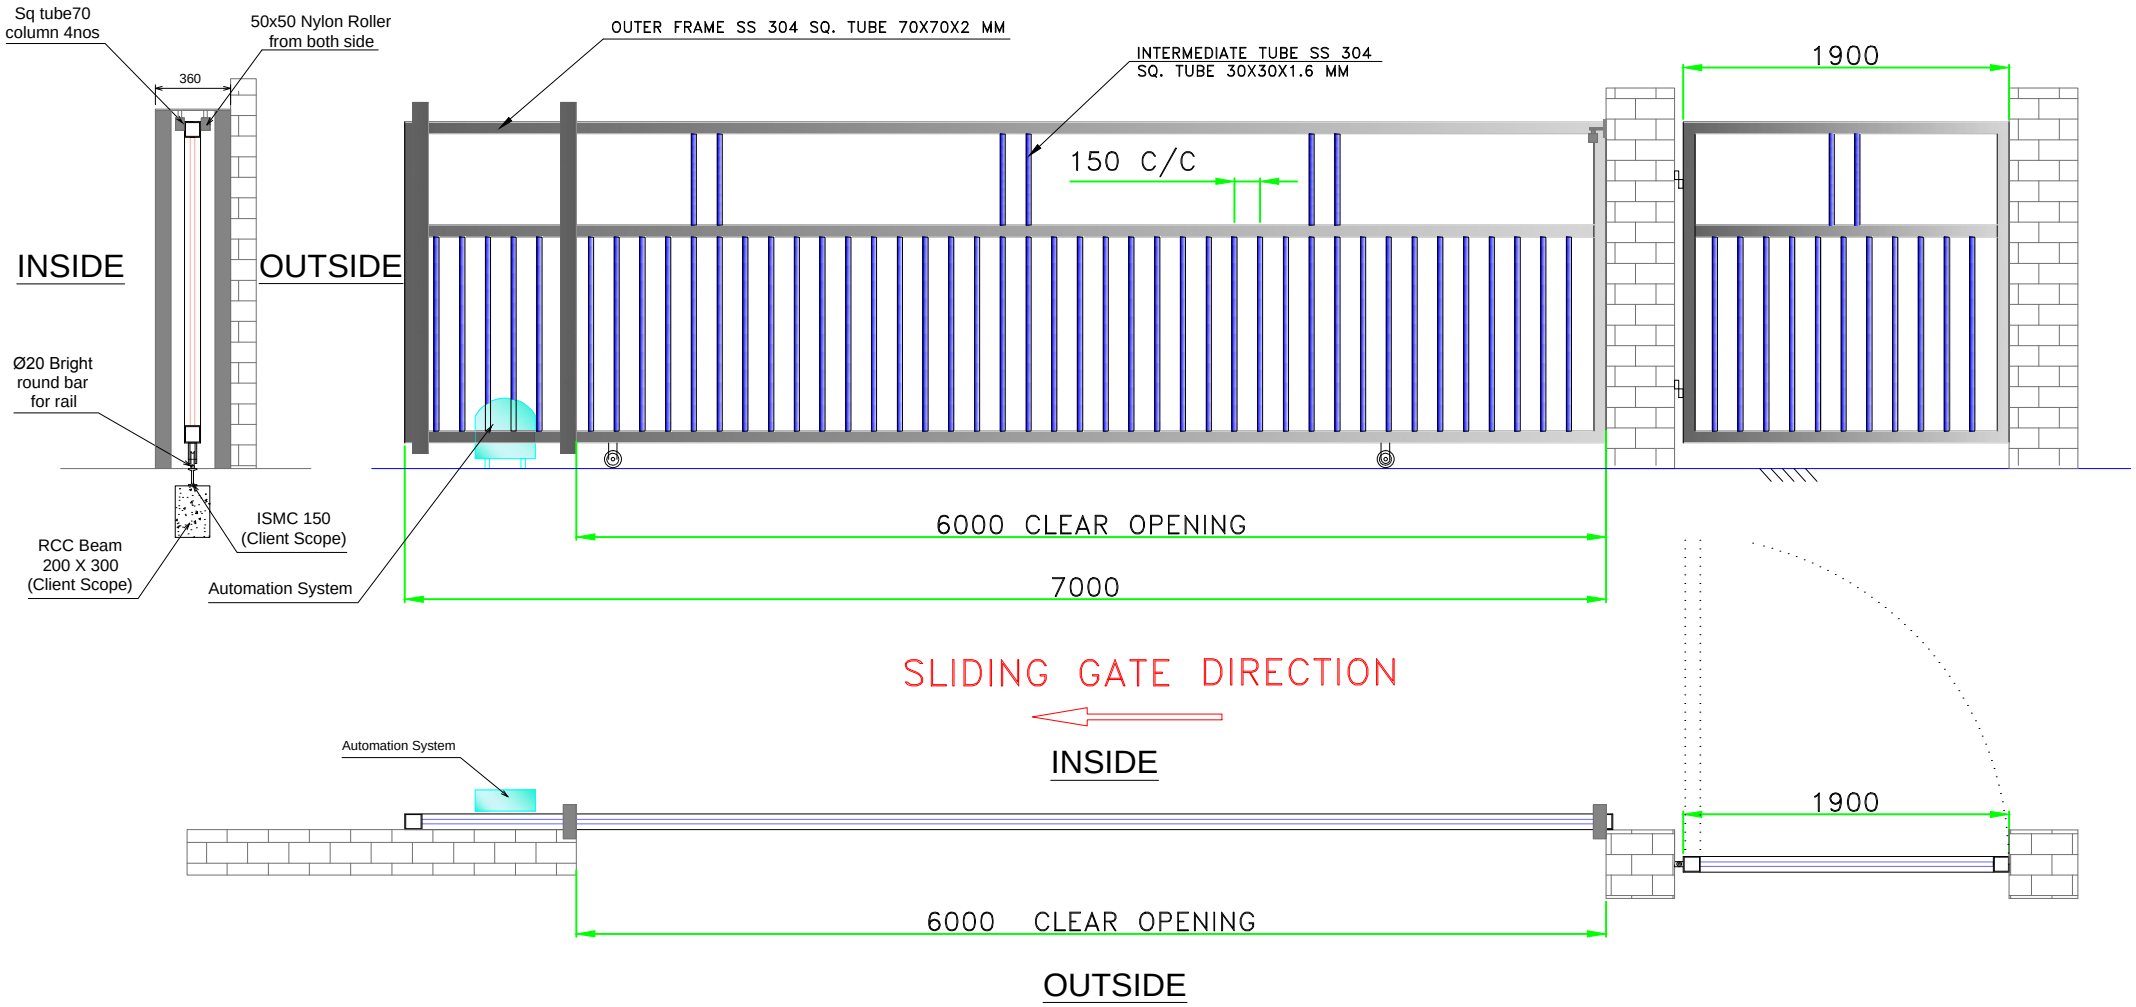


SLIDING GATE SIZE = 7000 (W) X 1800 (H), QTY = 1NOS.
CLEAR OPENING = 6,000 (W) X 1800 (H)
SLIDING GATE WEIGHT = 500 KG.APPROX.
WICKET GATE SIZE = 1900(W) X 1800 (H), QTY = 1NOS.
WICKET GATE W.C.2 WEIGHT= 175KG.APPROX.
OUTER FRAME = 70 X 70 X 2 mm
INNER FRAME = 30 X 30 X 1.6 mm
GAP B/W FRAME = 150 c/c
MATERIAL = SS 304
C' COLUMN VERTICAL SUPPORT = 4 NOS.
ALL DIMENSIONS ARE IN MM

This drawing & designing is the property of NIHVA TECHNOLOGIES. Not be sold or copy to any other concern.

TITLE

SLIDING GATE

CLIENT APPROVAL

ALL DIMENSION ARE IN mm

	SIGN	DATE
DRAWN	ABHIJIT	10/11/14
CHECK	ANIL	10/11/14
REV.	04	
APPRD.		
MFG		
Ref. No.		

NIHVA TECHNOLOGIES PVT. LTD.

NIHVA TECHNOLOGY
PVT. LTD. PUNE
Tel : 020 66304033
Email:- info@nihva.com
Website:- www.nihva.com

CLIENT - JSW
PROJECT -
SITE - KHED
DWG. NO. - NVA/JSW/D1/ 2 of 3
SCALE: 01 | WT: | SHEET: 01
If any queries contact : projects@nihva.com