



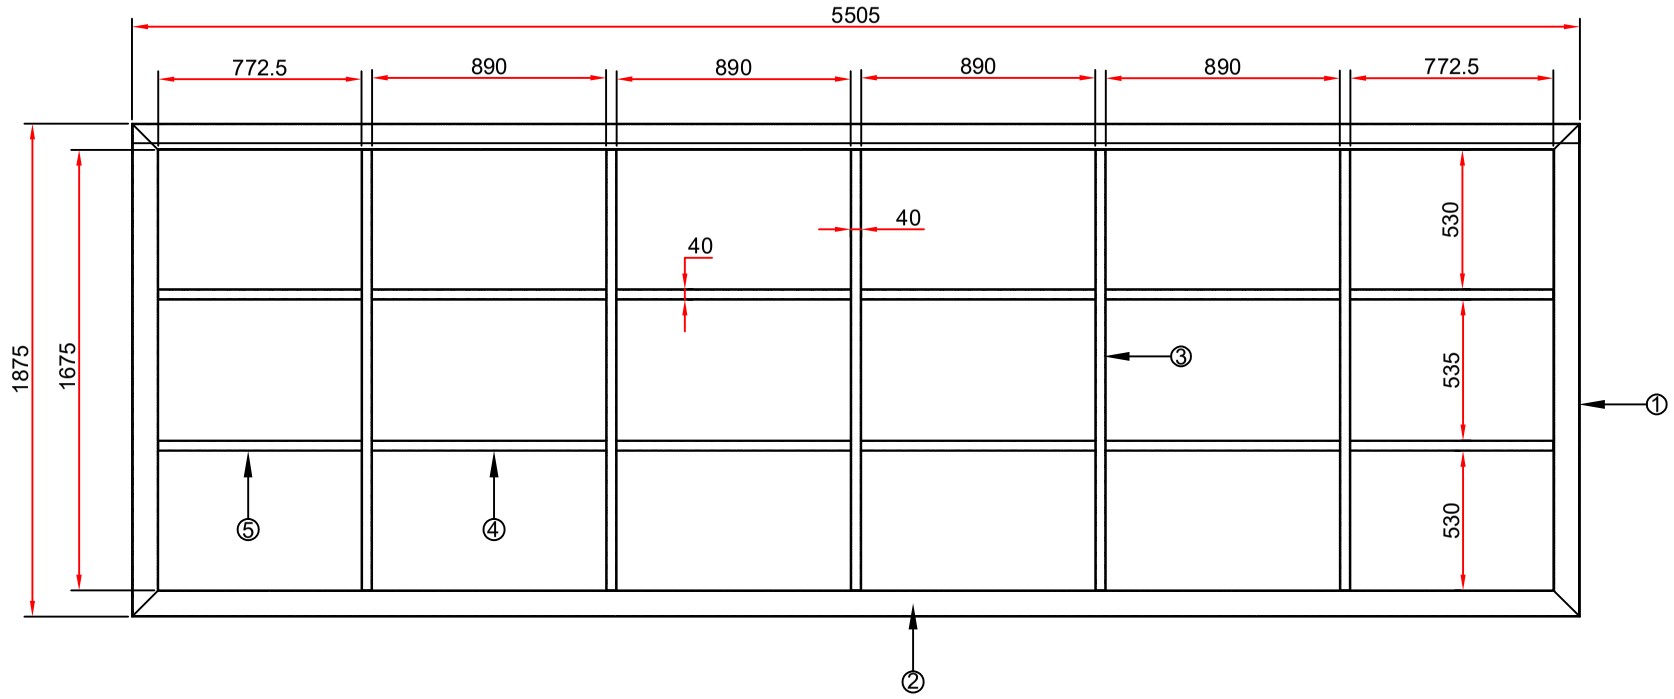

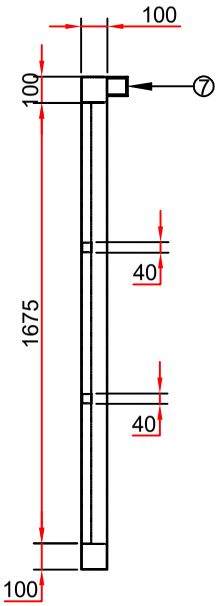

Note:-
1.All Dimension are in MM
2.Kindly Maintain the Given dimension

BOM			
SL NO.	DESCRIPTION	SPECIFICATION	QTY
1	MS SQ. TUBE	100X100X4X1875L	2NOS
2	MS SQ. TUBE	100X100X4X5505L	2NOS
3	MS SQ. TUBE	40X40X3.2X1675L	5NOS
4	MS SQ. TUBE	40X40X3.2X890L	8NOS
5	MS SQ. TUBE	40X40X3.2X772.5L	4NOS
6	MS FLAT	75X8X70L	2NOS
7	MS FLAT	75X8X5505L	1NO

Rev No.	Revision	Date	Revised By

This drawing & design is the property of NIHVA TECHNOLOGIES. Not to be sold or copied to any other concern.

TITLE:- Master Sliding Leaf

NIHVA TECHNOLOGIES PVT. LTD.

NIHVA TECHNOLOGIES PVT. PUNE
Tel : 020 66304033
Email:- info@nihva.com
Website:- www.nihva.com

	NAME	DATE	SIGN
DRAWN	SUJATA	20/07/2022	
CHECK	M.S	20/07/2022	
APPRD.	A.K	20/07/2022	

CLIENT - OC Specialities		
LOCATION - Solapur		
PRODUCT - Master Sliding Leaf		QTY-01
DWG NO:- NIHVA/22-23/CLT/0037		REV-00
SCALE: NTS	SCALE:-- 1:1	SHEET: 01 OF 01

If any queries contact : design1@nihva.com

ALL DIMENSION ARE IN mm