


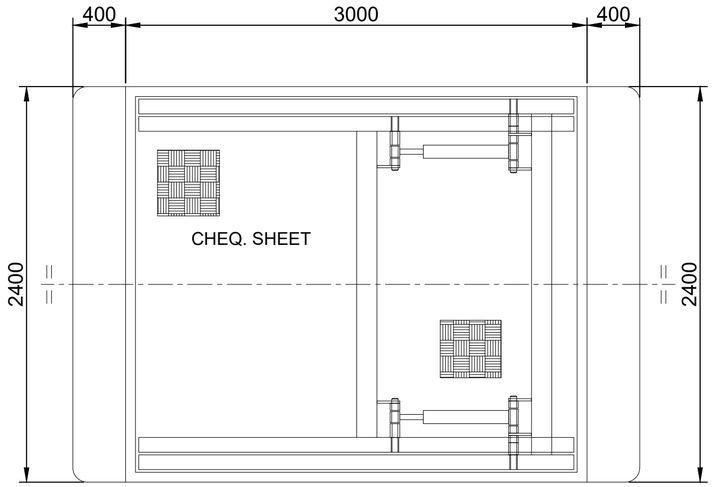


TOP VIEW

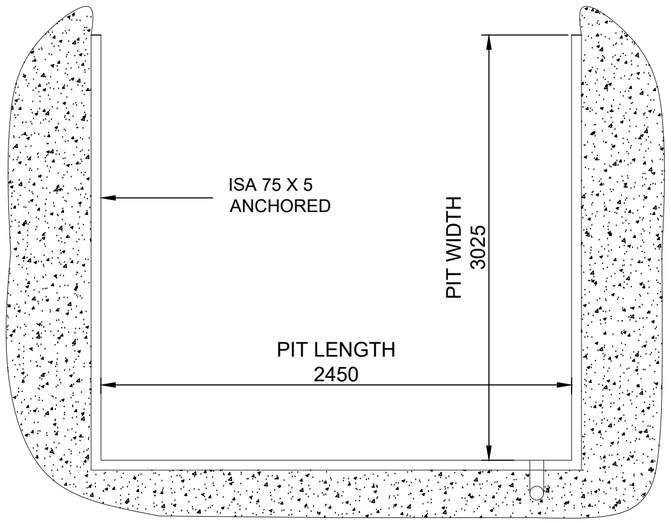


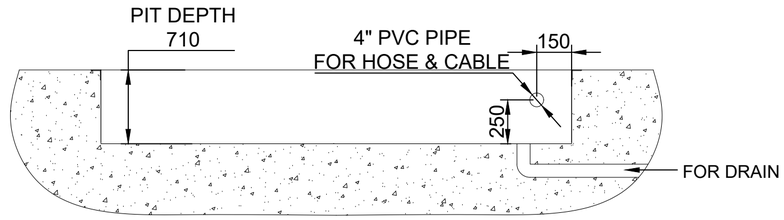

PIT DRAWING

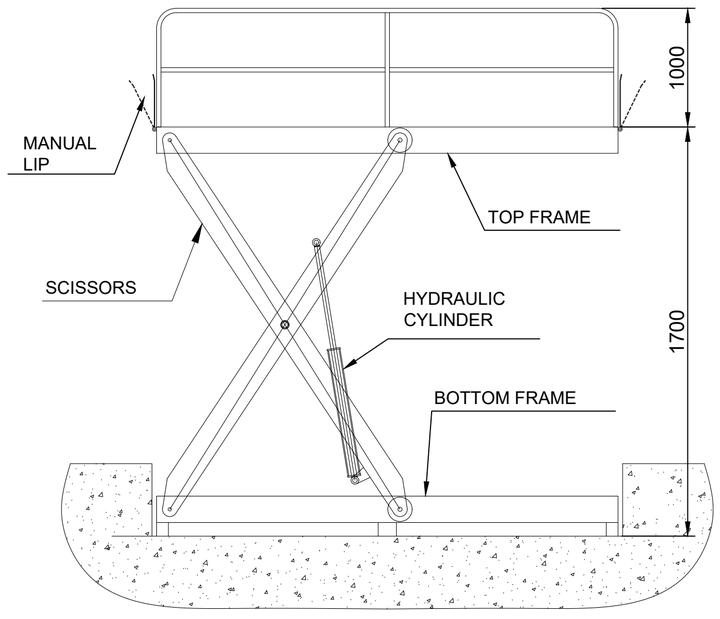

OPEN HEIGHT FRONT VIEW

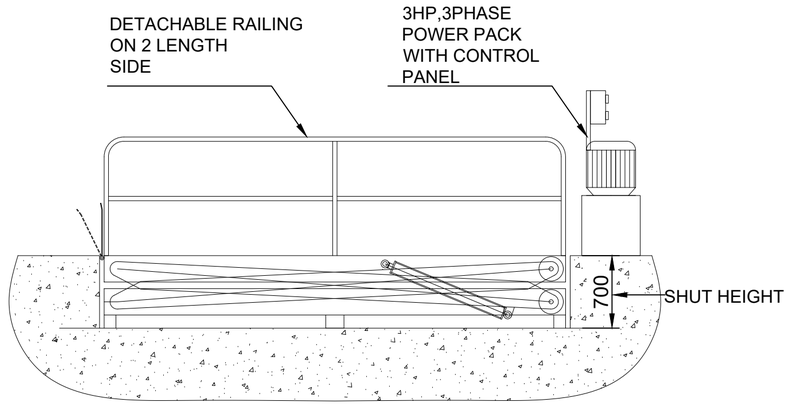

CLOSED HEIGHT FRONT VIEW

NOTE :

1. PIT FOR SCISSORLIFT HAS TO BE DIAGONALLY WITHIN 3-5 MM
2. BASE OF THE PIT HAS TO BE IN WATER LEVEL AND RIGHT ANGLE TO THE VERTICAL SIDE WALLS
3. PROPER ARRANGEMENT FOR ROUTING HOSES AND CABLES HAVE TO BE MADE DEPENDING ON SITE CONDITIONS AND POSITION OF POWER PACK
4. COVERING REQUIRED FOR CABLES AND RELATED CIVIL WORK IS IN CLIENTS SCOPE
5. WATER DRAINAGE AND PIT CLEANING NEEDS TO BE CONSIDERED AND DONE BY CLIENT
6. PIT & ALL CIVIL WORK IS IN CLIENT SCOPE.
7. TOLERANCE ± 10 MM.

SAFETY RAILING	1000 MM HT
POWER PACK	3HP,3PHASE
MAX HT	1700MM
LIFT HT	1000 MM
SHUT HT	700 MM
PLATFORM SIZE	2400W x 3000L
CAPACITY	1.5 TON

REV.	DESCRIPTION	DATE	REVISED By
000	RELEASED GA DRAWING	22/06/2022	MAHESH SUTAR

This drawing & design is the property of NIHVA TECHNOLOGIES. Not to be sold or copied to any other concern.

TITLE:- PIT MOUNTED SCISSOR LIFT

	NAME	DATE	SIGN
DRAWN	MAHESH S.	22/06/2022	
CHECK	MAHESH S.	22/06/2022	
APPRD.		22/06/2022	

NIHVA TECHNOLOGIES PVT. LTD.
NIHVA TECHNOLOGIES PVT. LTD. PUNE
Tel : 020 66304033
Email:- info@nihva.com
Website:- www.nihva.com

CLIENT - MMC DOORTECH SERVICES PVT. LTD.

LOCATION -

PRODUCT - SCISSOR LIFT

If any queries contact : design@nihva.com

DWG NO:- NIHVA/22-23/CLT/0069 REV- 0

ALL DIMENSION ARE IN mm

SCALE: NTS SCALE:-- 1:1 SHEET: 01 OF 01