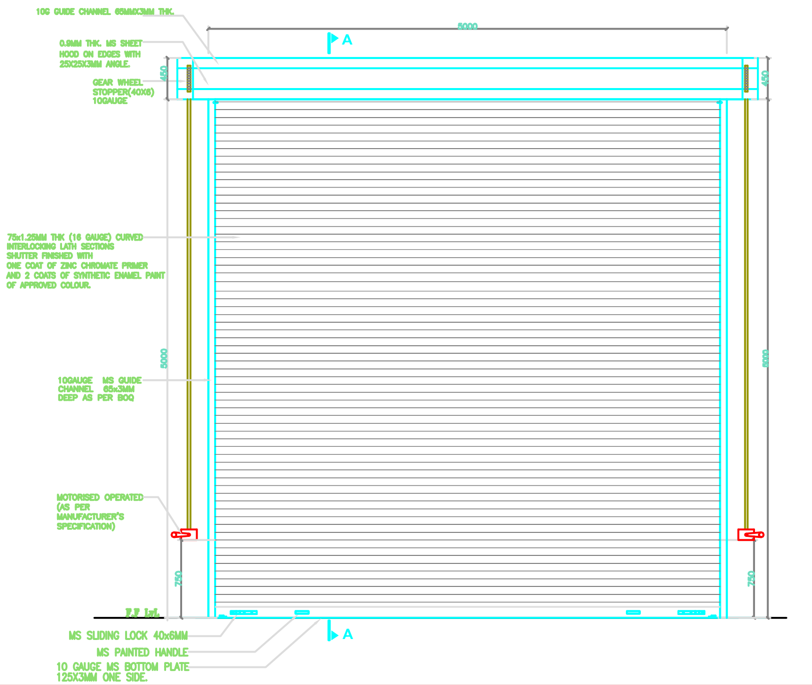
10G GUIDE CHANNEL 65MMX3MM THK.
0.9MM THK. MS SHEET HOOD ON EDGES WITH 25X25X3MM ANGLE.
GEAR WHEEL STOPPER(40X6) 10GAUGE
75x1.25MM THK (16 GAUGE) CURVED INTERLOCKING LATH SECTIONS SHUTTER FINISHED WITH ONE COAT OF ZINC CHROMATE PRIMER AND 2 COATS OF SYNTHETIC ENAMEL PAINT OF APPROVED COLOUR.
10GAUGE MS GUIDE CHANNEL 65x3MM DEEP AS PER BOQ
MOTORISED OPERATED (AS PER MANUFACTURER'S SPECIFICATION)
F.F LVL
MS SLIDING LOCK 40x6MM
MS PAINTED HANDLE
10 GAUGE MS BOTTOM PLATE 125X3MM ONE SIDE.
5000
450
750
A
A

ELEVATION OF RS1 (MOTORISED TYPE)
(5000MM x 5000MM)

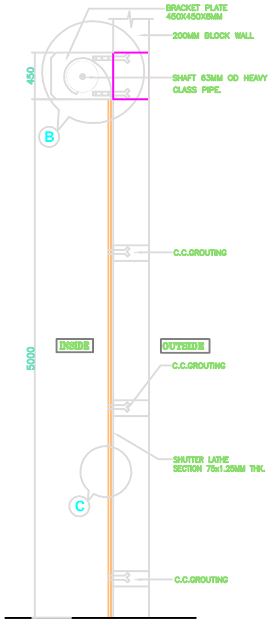
BRACKET PLATE 450X450X6MM
200MM BLOCK WALL
SHAFT 63MM OD HEAVY CLASS PIPE.
C.C.GROUTING
INSIDE
OUTSIDE
C.C.GROUTING
SHUTTER LATHE SECTION 75x1.25MM THK.
C.C.GROUTING
450
5000
B
C

TYPICAL SECTION - AA

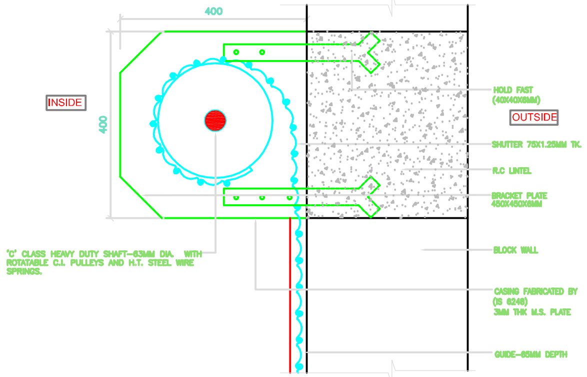
400
400
INSIDE
OUTSIDE
HOLD FAST (40X40X6MM)
SHUTTER 75X1.25MM TK.
R.C LINTEL
BRACKET PLATE 450X450X6MM
BLOCK WALL
CASING FABRICATED BY (IS 6248) 3MM THK M.S. PLATE
GUIDE–65MM DEPTH
'C' CLASS HEAVY DUTY SHAFT–63MM DIA. WITH ROTATABLE C.I. PULLEYS AND H.T. STEEL WIRE SPRINGS.

DETAIL AT B
(SCALE–1:30)

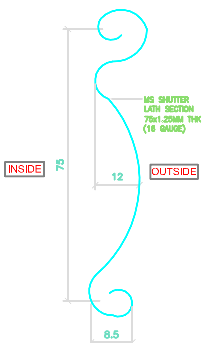

DETAIL AT D
(SCALE–N.T.S)

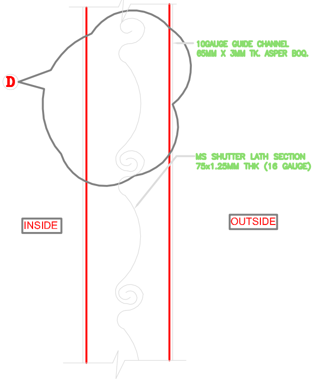
D
10GAUGE GUIDE CHANNEL 65MM X 3MM TK. ASPER BOQ.
MS SHUTTER LATH SECTION 75x1.25MM THK (16 GAUGE)
INSIDE
OUTSIDE

DETAIL AT C
(SCALE–N.T.S)

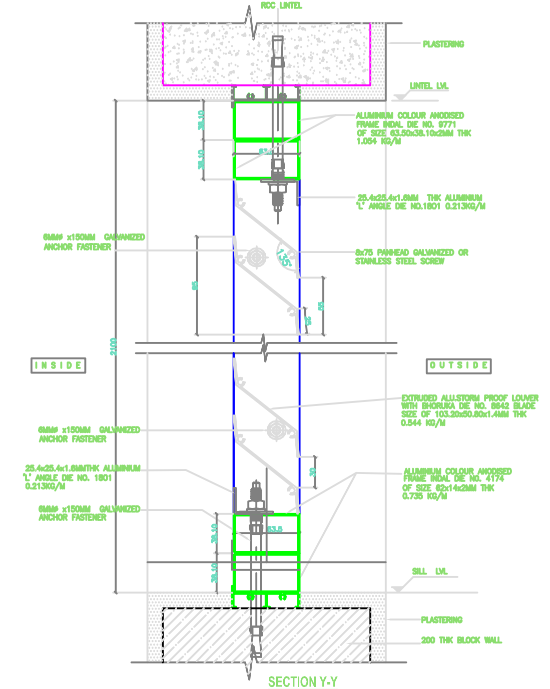
RCC LINTEL
PLASTERING
LINTEL LVL
ALUMINIUM COLOUR ANODISED FRAME INDAL DIE NO. 9771 OF SIZE 63.50x38.10x2MM THK 1.054 KG/M
25.4x25.4x1.6MM THK ALUMINIUM 'L' ANGLE DIE NO.1801 0.213KG/M
6MM⌀ x150MM GALVANIZED ANCHOR FASTENER
8x75 PANHEAD GALVANIZED OR STAINLESS STEEL SCREW
135°
INSIDE
OUTSIDE
2100
EXTRUDED ALU.STORM PROOF LOUVER WITH BHORUKA DIE NO. 8642 BLADE SIZE OF 103.20x50.80x1.4MM THK 0.544 KG/M
6MM⌀ x150MM GALVANIZED ANCHOR FASTENER
25.4x25.4x1.6MMTHK ALUMINIUM 'L' ANGLE DIE NO. 1801 0.213KG/M
ALUMINIUM COLOUR ANODISED FRAME INDAL DIE NO. 4174 OF SIZE 62x14x2MM THK 0.735 KG/M
6MM⌀ x150MM GALVANIZED ANCHOR FASTENER
38.10
63.5
SILL LVL
PLASTERING
200 THK BLOCK WALL

SECTION Y-Y

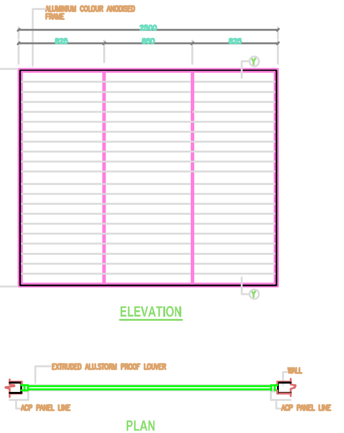
ALUMINIUM COLOUR ANODISED FRAME
2500
825
850
825
2100
Y
Y
EXTRUDED ALU.STORM PROOF LOUVER
WALL
ACP PANEL LINE
ACP PANEL LINE

ELEVATION

PLAN

L -(2500 x 2100)
(LOUVERED WINDOW)

KEY PLAN :-

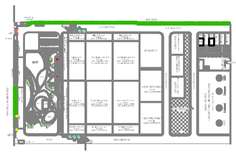

LEGEND :-

N
W
E
S

GENERAL NOTES :

- ALL DIMENSIONS ARE IN MILLIMETERS AND ARE UNFINISHED DIMENSIONS UNLESS OTHERWISE SPECIFIED.
- ALL LEVELS ARE IN METERS AND ARE UNFINISHED LEVELS UNLESS OTHERWISE SPECIFIED.
- DO NOT SCALE DRAWINGS. ONLY WRITTEN DIMENSIONS SHALL BE FOLLOWED, ANY DISCREPANCIES NOTED SHALL BE BROUGHT TO THE NOTICE OF THE ARCHITECT PRIOR TO EXECUTION.
- FOR DETAILS SUCH AS DOORS, WINDOWS, GRILLS, GATES, SKYLIGHT, TOILETS, STAIRCASES, HANDRAIL, RAILING, ETC. REFER RESPECTIVE ARCHITECTURAL DRAWINGS.
- THESE DRAWINGS SHALL BE CORRELATED AND READ IN CONJUNCTION WITH RESPECTIVE CONSULTANT'S APPROVED DRAWINGS FOR STRUCTURAL MEMBERS, SERVICES SUCH AS PLUMBING, SANITARY, ELECTRICAL, AIR-CONDITIONING, VENTILATION, RAINWATER DRAINAGE & WATERPROOFING AND LANDSCAPING. ANY DISCREPANCIES NOTED SHALL BE BROUGHT TO THE NOTICE OF THE ARCHITECT PRIOR TO EXECUTION.
- ALL TOILETS WILL HAVE SUNK FLOORS (UNLESS OTHERWISE SPECIFIED) AS PER RESPECTIVE STRUCTURAL DRAWINGS, AND WATERPROOFING AS PER SPECIFICATION.

SCHEDULE OF JOINERY

TYPE	DESCRIPTION	SIZE
RS	ROLLING SHUTTER	5000 x 5000
FD	FIRE DOOR	1200 x 2400
FD1	FIRE DOOR	2000 x 2400
ST1	STEEL DOOR	2000 x 2400
ST2	STEEL DOOR	900 x 2400
D	GLASS DOOR	3000 x 3000
D1	FLUSH DOOR	1500 x 2400
D2	GLASS DOOR	2000 x 3000
D2A	GLASS DOOR	1500 x 2400
D3	FLUSH DOOR	900 x 2400
D4	GLASS DOOR	1000 x 2400
D5	FLUSH DOOR	1200 x 2400
D6	FLUSH DOOR (TOILET DOOR)	900 x 2100
D7	FLUSH DOOR (TOILET DOOR)	750 x 2100
L	LOUVER	2500 x 2100
V	VENTILATOR	600 x 600

REV.	DESCRIPTION	DATE	BY	CHD.
R1	ISSUED FOR CONSTRUCTION	06-03-14	GB	E.V

AMENDMENT

GRAPHIC SCALE:
0 0.2M 0.6M 1.6M
0.2M 0 0.4M 1.2M 2M

CLIENT:
M/s. Graziano Transmissioni India Pvt. Ltd..

PROJECT:
PROPOSED ODS INDIA NEW PLANT
IN GUJARAT.

DRAWING TITLE:
MAINFACTORY & OFFICE BUILDING
JOINERY DETAILS (SHEET-1)

SCALE : 1 : 25	DRAWN : G.BANU	REV
DATE : 05-03-14	CHKD : E.VALLI	
DRAWING NO: OEN-G-FAC-AR11-GR-02-177144		R1

ARCHITECTURE ● INTERIOR DESIGN ● ENGINEERING ● PLANNING ● CONSTRUCTION MANAGEMENT

CRN
C R NARAYANA RAO
10, KARPAGAMBAL NAGAR,
MYLAPORE, CHENNAI-600 004
B.Tech, (Hons.), M.S., (Ill.), Ph.D., M.Am.Soc. C.E., F.I.E., F.I.V.,
Chartered Engineer – Registered Architect.

WHICH IT HAS BEEN LOANED. AFTER FULFILLING THE PURPOSE OF ISSUE THE DRAWINGS SHALL BE RETURNED TO CRN.