

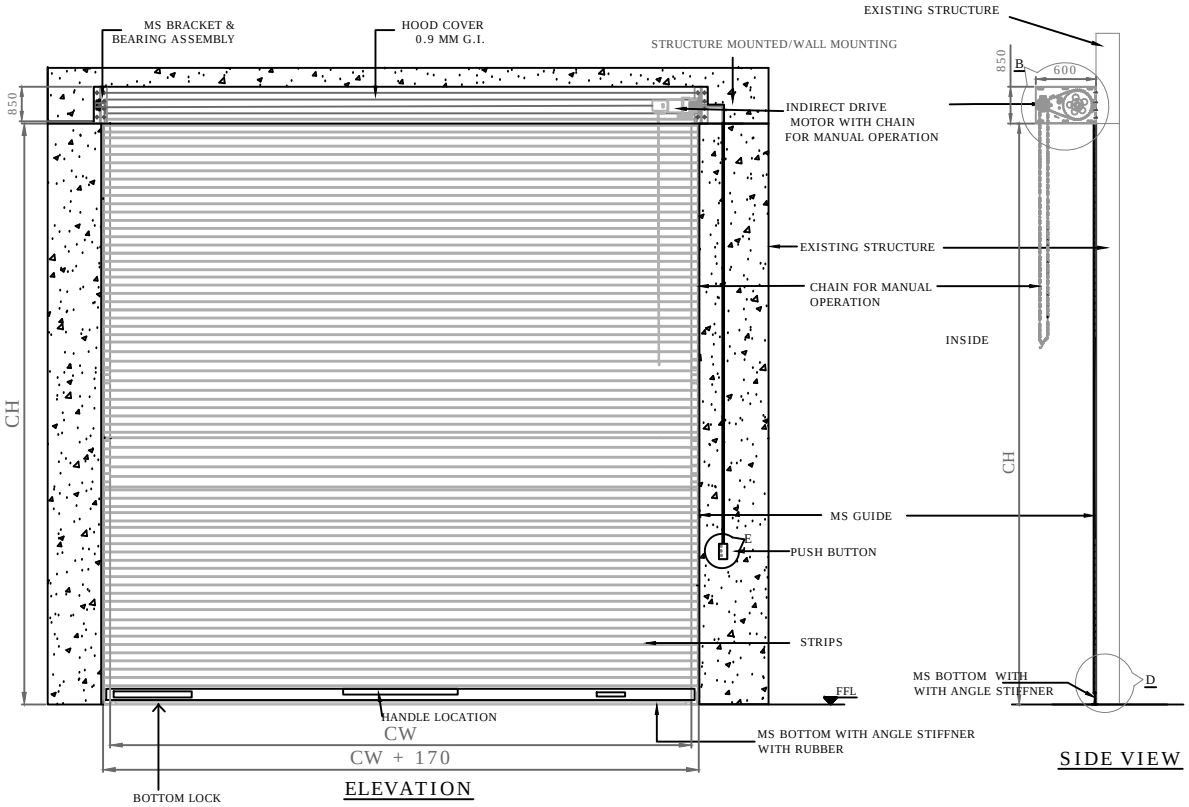



ELEVATION

SIDE VIEW

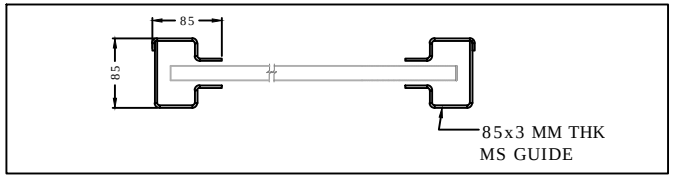


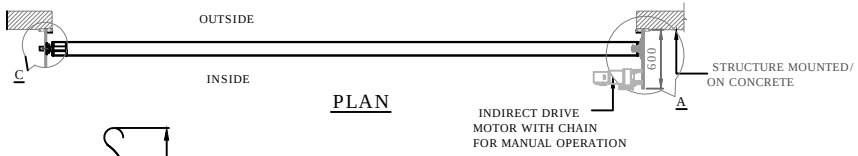


PLAN

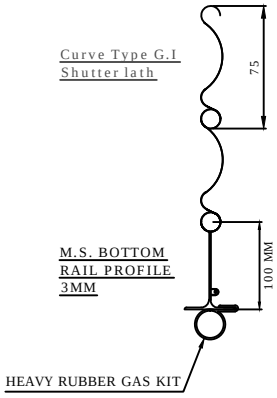

DETAILS : D

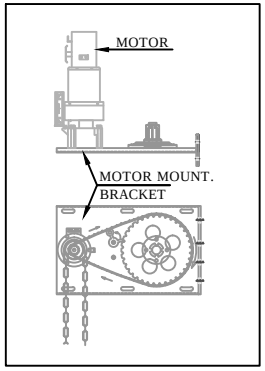

DETAILS : A & B

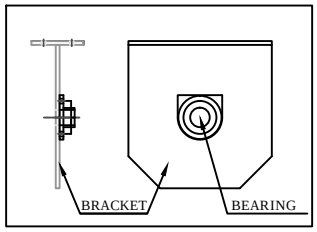

DETAILS : C

		RAL 7001	SILVER GREY
3400	3950	2	RAL 7001
CLEAR WIDTH (CW)	CLEAR HEIGHT (CH)	QUANTITY	RAL COLOR POWDER COATED

This drawing & design is the property of NIHVA TECHNOLOGIES. Not to be sold or copied to any other concern.

TITLE: MOTORIZED ROLLING SHUTTER

NIHVA TECHNOLOGIES PVT. LTD.

NIHVA TECHNOLOGIES PVT. LTD. PUNE
Tel : 020 66304033
Email:- info@nihva.com
Website:- www.nihva.com

	NAME	SIGN	DATE
DRAWN	S.M.S.		9.11.2020
CHECK	K.P.		9.11.2020
APPRD.			

CLIENT -

PROJECT -

SITE LOCATION - PUNE

If any queries contact : projectsupport@nihva.com

DWG. NO. : NIHVA/20-21/VDR/0075 REV- R00

ALL DIMENSION ARE IN mm

SCALE: NTS WT: SHEET: